Ny hal, facader

Vægge: sorte, matte sandwichpaneler, vandrette, 1 m høje. Tag: sorte sandwichpaneler, 30°. Sokkel: beton 0,4 m over terræn; gulv i soklens overkant. Sidehøjde 4,0 m over sokkel. Højder i meter over terræn.

Facade mod nord (port og dør mod ridebanen)

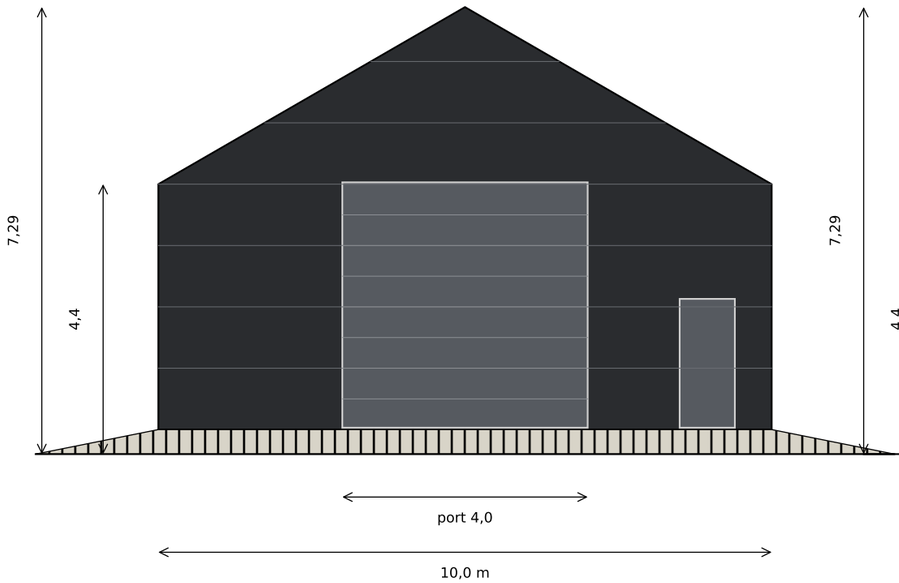

Facade mod øst

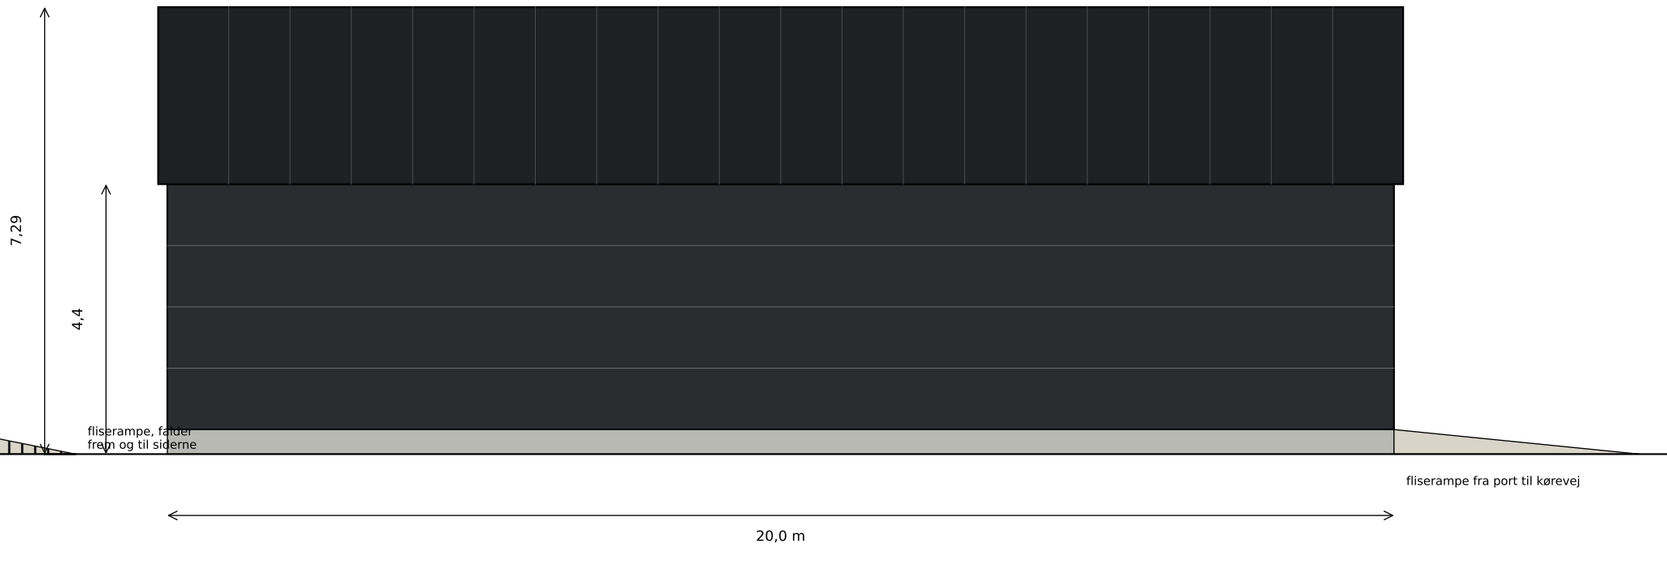

Facade mod syd (ingen åbninger)

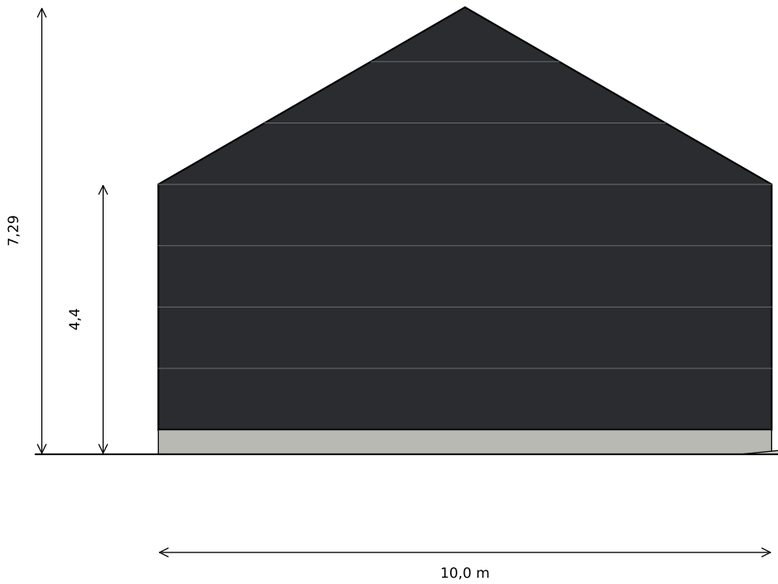

Facade mod vest

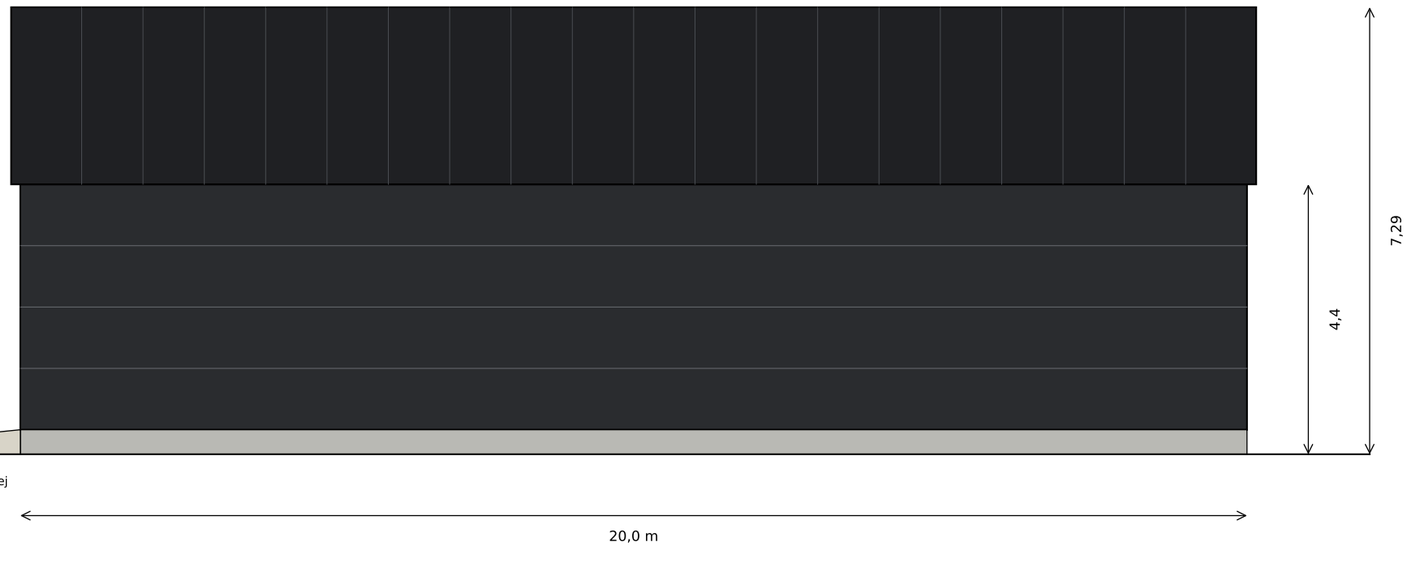

Terræn er forudsat vandret. Panelernes dækbredde (FALK 1060 WB er 1,06 m) og portens endelige højde fastlægges i byggeansøgningen.

BYGGESAG: Nældevej 42, 9000 Aalborg		**A1.2**
EMNE: Ny hal, facader	DATO: 11.10.2026	
UDFØRT AF: JB	MÅL: 1 : 100 (A3)	LANDZONEANSØGNING