
Snit B-B gennem soveværelset (set mod nord)

Tal på stængerne: normalkraft i kN for sne på hele taget (K1). Rød = tryk, blå = træk.

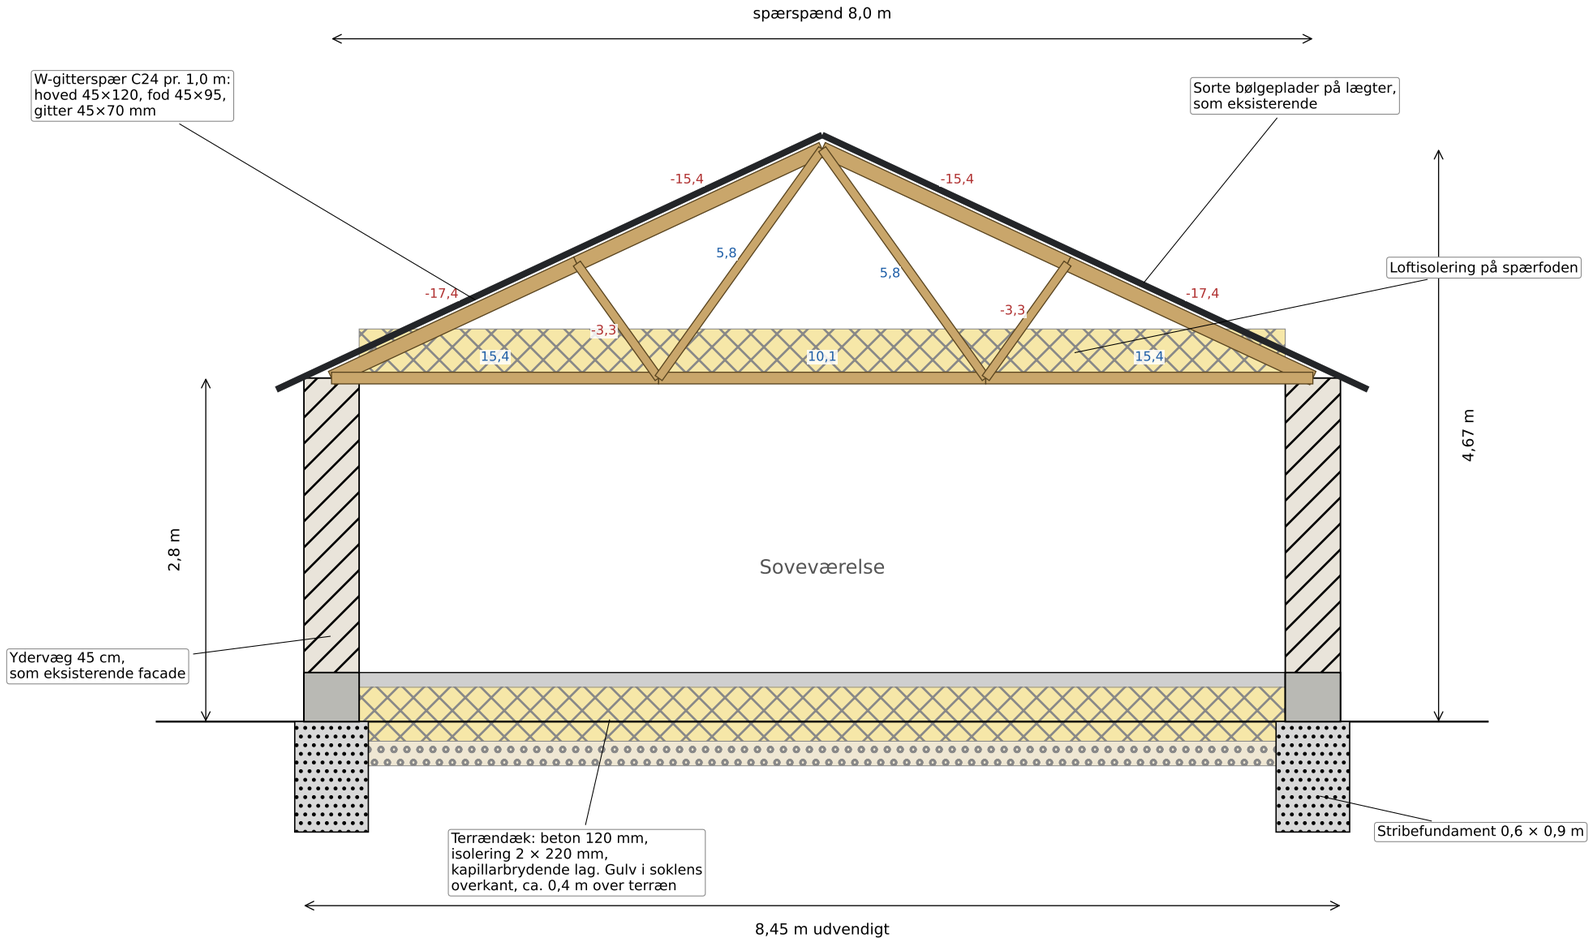

OVERSLAGSBEREGNING, hovedresultater

Spær: W-gitterspær C24, spænd 8,0 m, afstand 1,0 m

Sne: s_k = 1,0 kN/m², μ = 0,8 og 1,2 (ophobning vest)

Egenlast tag 0,35 og loft 0,35 kN/m², opbevaring 0,5 kN/m²

Udnyttelse spærhoved: 0,88

Udnyttelse spærfod: 0,80

Udnyttelse gitterstænger: 0,28

Lodret last pr. spær: 9,8 kN (9,8 kN/m væg)

Løft fra vind pr. spær: 1,4 kN

Linjelast på fundament: ca. 17,8 kN/m

Ikke eftervist: tandpladesamlinger, bæring på husets gavl, skotrender, stabilitet, jordens bæreevne.

Se bilag A2.4.

Overslagsberegning. Spær dimensioneres og leveres af spærfabrik. Vægopbygning, gulv og fundament er principielle og fastlægges i byggeansøgningen.

BYGGESAG: Nældevej 42, 9000 Aalborg		**A2.3**
EMNE: Tilbygning, snit B-B og overslag	DATO: 11.10.2026	LANDZONEANSØGNING
UDFØRT AF: JB	MÅL: 1 : 50 (A3)	