Ansøgning: ny hal og tilbygning til stuehus

Nældevej 42, 9000 Aalborg. Matr.nr. 1cc Restrup Hgd., Sønderholm m.fl. BFE-nr. 1416157 m.fl.

Til Aalborg Kommune, By og Land, Byggeri, att. Kirstine Reese. [dato].

Ansøgere og ejere: [navne], Nældevej 42, 9000 Aalborg. Telefon [nr.], e-mail [adresse].

1. Hvad ansøgningen omfatter

Ansøgningen følger op på mødet den [dato] og jeres mail med gennemgang af praksis. Den har to dele, som vi beder kommunen behandle samlet, fordi de tilsammen viser, hvordan ejendommens bebyggelse kommer til at se ud:

Del A: Ny hal	200 m² hal til maskiner til ejendommens drift og til privat opbevaring. Vi søger landzonetilladelse efter planlovens § 35, stk. 1. Hallen opføres først
Del B: Tilbygning	123 m² tilbygning til stuehuset, så boligen bliver ca. 246 m². Vi mener ikke, den kræver landzonetilladelse, jf. planlovens § 36, stk. 1, nr. 10, og beder kommunen bekræfte det. Tilbygningen opføres senere

Byggetilladelse til begge dele søges særskilt.

2. Ejendommen

Areal	39.130 m² (ca. 3,9 ha): matr.nr. 1cc (19.977 m²), 1rp (5.516 m²) og 57b (13.637 m²)
Zone og notering	Landzone. [Noteret som landbrugsejendom / ikke landbrugsnoteret: bekræftes]
Anvendelse	Bolig med hestehold: [antal] heste, stald med 4 hestebokse, 2 ponybokse og løsdrift, ridebane og folde
BBR-bygning 4	Stuehus, 123 m², opført 1992. Én boligenhed
BBR-bygning 2	Bygning til træning og opstaldning af heste, 284 m²
Øvrigt	Skur ved stalden, ca. 23 m², opført efter byggesag S2021-530504 (2020-1967) [BBR-registrering bekræftes]. Ridebane ca. 20 × 39 m med omfangsdræn og pumpe
Forsyning	Privat vandforsyning, jordvarme, privat fællesvej. Spildevand: mekanisk rensning med udledning

3. Planforhold og udpegninger

Vi har slået begge placeringer op i Plandata og Danmarks Arealinformation den 10. oktober 2026. Hvor intet andet er nævnt, gælder oplysningen både hal og tilbygning:

Plangrundlag	Landzone. Ingen lokalplan og ingen kommuneplanramme
Kommuneplan 2021	Større sammenhængende landskab. Potentielt naturområde og potentiel økologisk forbindelse (Tostrup og Hasseris Ådal samt Restrup og Sønderholm Skove). Hallens placering ligger desuden i et område, der kan blive udsat for oversvømmelse; det gør tilbygningens ikke
Landskabskarakter	Nørholm Fjordlandskab, jf. kommunens afgørelse for naboejendommen Nældevej 30 (sag S2023-8926) [bekræftes for nr. 42]
Ikke udpeget som	Bevaringsværdigt landskab, lavbundsareal, værdifuldt kulturmiljø, værdifuldt landbrugsområde, skovrejsningsområde eller geologisk bevaringsværdi
Kystnærhedszonen	Ejendommen ligger i kystnærhedszonen, uden for udviklingsområde
Skovbyggelinje	Begge placeringer ligger inden for skovbyggelinjen fra skoven mod øst. Hallen ligger ca. 35 m fra skovbrynet, tilbygningen ca. 80 m. Gives der landzonetilladelse, gælder forbuddet i naturbeskyttelseslovens § 17 ikke, jf. § 17, stk. 2, nr. 5
Øvrige linjer	Uden for sø- og åbeskyttelseslinje, kirkebyggelinje og fredninger. Ingen beskyttede sten- og jorddiger på stedet
Beskyttet natur (§ 3)	Nærmeste er en sø ca. 170 m fra hallen og ca. 210 m fra tilbygningen. Nærmeste beskyttede vandløb ca. 300 m
Natura 2000	Nærmeste område er Nibe Bredning, Halkær Ådal og Sønderup Ådal (habitatområde, fuglebeskyttelses- og Ramsarområde), ca. 1,8 km væk
Bilag IV-arter	Kommunen har i nyere afgørelser på Nældevej (S2024-1080 og S2025-2936) oplyst kendskab til spidssnudet frø, odder, strandtudse, stor vandsalamander og flagermus inden for 2 km. Se afsnit A2

Del A: Ny hal på 200 m²

A1. Det ansøgte

Bygning	Hal 20,0 × 10,0 m = 200 m², én etage, sadeltag 30° med kip nord-syd. Sidehøjde 4,0 m over soklen, som går 0,4 m over terræn. Kiphøjde 7,3 m over terræn
Materialer	Stålrammer på gennemgående betonsokkel med overkant ca. 0,4 m over terræn, i samme højde som stuehusets sokkel. Facader og tag i sorte, matte sandwichpaneler, som de sorte tage på hus og stald
Åbninger	Port 4,0 × 4,0 m og en gangdør i nordgavlen, mod ejendommens egne bygninger. Ingen åbninger i øvrige facader
Placering	I folden umiddelbart øst for haven, 11,3 m fra stuehuset og 11,4 m fra skuret ved stalden. Parallelt med stalden
Maskiner til ejendommens drift, ca. 110 m²	Traktor med frontlæsser, balletrailer, møgvogn, [harve/slæbeplanke til ridebane, brakpudser, græsslåmaskine: listen bekræftes] og kørebane. Bruges til foder og strøelse (ca. 25 rundballer om året), udmugning, kørsel til møddingen og pasning af folde og ridebane
Privat opbevaring, ca. 90 m²	Lukket rum på 40 m² med toilet, plads til tre trailere og en lift til hjulskift og vedligehold af husstandens egne biler
Eksisterende udhuse	Ejendommens eneste udhus er skuret på ca. 23 m², som er fyldt med åbnede wrapballer, der skal stå tørt. Der er ingen garage, carport eller maskinhus. Stalden på 284 m² er i brug til hestene: bokse, løsdrift og sadelrum (bilag A3.1)
Tagvand	Tagvand fra hallen (ca. 210 m² tagflade) ledes i lukket rør via en forsinkelsesbrønd til ridebanens eksisterende omfangsdræn og pumpebrønd (ca. 200 l/min), som pumper vandet væk fra arealet [udløbssted oplyses]. Vi søger særskilt om tilladelse, hvis tilslutningen kræver det
Opvarmning og afløb	Uopvarmet hal [bekræftes]. Toilettet tilsluttes [ejendommens eksisterende spildevandsanlæg: afklares]
Forplads	Foran port og dør lægges fliser 50 × 50 cm, som ejendommens øvrige belægning, som en rampe fra gulvhøjde ved gavlen skråt ned til kørevejen, ca. 4 m lang, med fald ud til siderne
Adgang	Ad ejendommens eksisterende kørevej fra Nældevej øst om stalden. Der etableres ikke ny overkørsel til Nældevej

Plantegningen (bilag A1.1) viser, hvad hver maskine og hver funktion fylder. De eksisterende bygninger kan ikke rumme maskinerne: stalden er i brug til hestene rum for rum, som vist på bilag A3.1, løsdriften bruges med dybstrøelse, og ingen af bygningerne har en port, en traktor kan køre ind ad. Maskiner og trailere står i dag udendørs. Der drives ikke erhverv fra hallen, og der indrettes ikke bolig.

Vi søger landzonetilladelse til hele bygningen, så kommunen kan vurdere den samlet. Mener kommunen, at maskindelen kan anmeldes som erhvervsmæssigt nødvendig efter § 36, stk. 1, nr. 3, og § 38, stk. 2, beder vi om at få det oplyst.

A2. Begrundelse

Behovet og bygningens størrelse

- Ejendommen er på 3,9 ha med hestehold, ridebane og folde. Pasningen kræver traktor, balletrailer, møgvogn og redskaber, som bør stå under tag. Hestehold er hjemmehørende i landzonen, og kommunen har flere gange lagt vægt på netop det, senest i sag S2025-326 og i sag S2022-171976 (Nibevej 384), hvor en lade på 98 m² til traktor, redskaber, halm og hø blev fundet passende til en ejendom på 1,87 ha med tre heste.

- Vi ved, at kommunen normalt giver tilladelse til udhuse på 50-100 m² og kun til større, når der er særlige omstændigheder. Kommunen ser efter sine afgørelser på ejendommens størrelse, omfanget af eksisterende udhuse og placeringen. Hos os er ejendommen på 3,9 ha, det eneste udhus er et skur på ca. 23 m², og behovet er vist maskine for maskine på bilag A1.1.
- Kommunen har i nærområdet givet tilladelse til tre bygninger af samme art: S2025-326 (Nørholmsvej 149, 16. juni 2025): udhus på 148 m² på 2,5 ha med privat hestehold, 104 m² til maskiner og 44 m² til privat værksted. S2025-10959 (Duedal 93, 21. maj 2026): uopvarmet hal på 150,7 m² med 6,7 m til kip på 1,65 ha, og samtidig en garage på 50 m² ved siden af, fordi der ikke var andre udhuse, og behovet var dokumenteret. S2023-4703 (Nørholmsvej 222, 20. april 2023): en samlet bygning på 198 m² på 6,3 ha, heraf 120 m² maskinhus og 78 m² udhus.
- Vores hal svarer i opdeling og størrelse til den sidste: ca. 110 m² til maskiner og ca. 90 m² til privat opbevaring. Maskindelen svarer til de 104 m², der blev godkendt i S2025-326 på en mindre ejendom, og den private del ligger inden for de 50-100 m².
- Ved at samle maskiner og privat opbevaring under ét tag undgås to fritliggende bygninger, og udendørs oplag af maskiner og trailere forsvinder. Kommunen lagde i S2023-4703 afgørende vægt på, at sammenbygningen undgår spredt bebyggelse og påvirker landskabet mindre.

Placering og landskab

- Hallen ligger i direkte tilknytning til ejendommens samlede bebyggelse, ca. 11 m fra stuehus og skur, og nås ad den eksisterende kørevej. Det er godt inden for de ca. 20 m, kommunen normalt regner som tilknytning (S2025-6024), og bygninger og færdselsarealer bliver ved med at være én enhed.
- I Nørholm Fjordlandskab bør ny bebyggelse efter kommuneplanen knyttes til de eksisterende bebyggelser og understøtte strukturen af mindre gårde og husmandssteder langs vejene, og det åbne, flade kystlandskab bør bevares. Hallen lægges inde i en eksisterende gårdbebyggelse ved Nældevej, mellem stuehus, stald og skov, og ikke ud i det åbne land.
- Set fra Nældevej og fra fjorden mod nord ligger hallen bag stald, ridebane og læbælte. Mod vest skærmer læbæltet langs skellet og mod øst skoven. Hallen slører derfor ikke landskabssammenhængene i det større sammenhængende landskab.
- Kiphøjden på 7,3 m over terræn er under bygningsreglementets 8,5 m og 0,6 m over de 6,7 m, kommunen godkendte i S2025-10959; forskellen er soklen, som følger stuehusets, og hallens større bredde. Sidehøjden på 4,0 m over gulv er bestemt af porten og af frihøjden over traktor med frontlæsser. Facader og tag er sorte og matte, uden reflekser. Vi planter gerne et læbælte af hjemmehørende arter syd for hallen, hvor den står frit, og holder det i mindst 3 m højde.

Kystnærhedszonen

- Hallen opføres inde i en bestående bebyggelse knap 2 km fra kysten, bag eksisterende bygninger og beplantning set fra kysten, og den ændrer ikke kystlandskabet. Vi mener derfor, at den har helt underordnet betydning for de nationale planlægningsinteresser i kystområderne, jf. planlovens § 35, stk. 3. Kommunen har givet tilladelse til udhuse, garager og carporte i samme del af kystnærhedszonen, uden for udviklingsområde, i sagerne S2023-8926 (Nældevej 30), S2024-19470 (Nældevej 55), S2024-1080 (Nældevej 9) og S2025-326.

Natur

- Hallen opføres på en afgræsset fold tæt ved bygninger, kørearealer og ridebane. Der fældes ingen træer og fjernes ingen hegn eller diger. Med 1,8 km til nærmeste Natura 2000-område og hallens begrænsede omfang kan den ikke påvirke området.
- Bilag IV-arter: Byggefeltet er en tæt afgræsset hestefold uden vandhuller, grøfter, gamle træer eller bygninger, og der er daglig færdsel. Det er ikke egnet som yngle- eller rasteområde for padder, odder eller flagermus. Nærmeste sø ligger ca. 170 m væk. Der fældes ingen træer og nedrives ingen bygninger, så flagermus mister ikke levesteder, og en bygning på 200 m² inde i bebyggelsen spærrer ikke for dyrs vandring.
- Skovbrynet berøres ikke: der er ca. 35 m fra hallen til skoven, og hallen ligger ikke mellem skoven og åbent land, men ind mod ejendommens bygninger. Den tager derfor ikke udsynet til skoven fra vej eller nabo. Hele ejendommens bebyggelse ligger inden for skovbyggelinjen, så hallen kan ikke placeres uden for den.

- Den potentielle økologiske forbindelse følger ådalen og skovene. Hallen optager 200 m² af en fold midt i bebyggelsen og spærrer ikke for forbindelsen.

Oversvømmelse

- Hallen er et uopvarmet maskinhus uden beboelse. Soklens overkant og hallens gulv lægges ca. 0,4 m over terræn, i samme højde som stuehusets sokkel [terrænkote indsættes], og kommunen er velkommen til at stille vilkår om sokkelhøjde. Terrænet ændres ikke uden om hallen, og tagvandet ledes til ejendommens eksisterende afløb med pumpe, så der ikke ledes vand mod naboer.

Naboer

- Hallen har ingen åbninger mod naboer. Nærmeste bygning på naboejendom ligger ca. 50 m fra hallen mod sydøst [afstand til nabobeboelse bekræftes], og hallen holder [afstand] m til skel. Naboerne har skriftligt erklæret, at de godkender byggeriet (bilag B2).

A3. Vilkår, vi kan acceptere

Hallen bruges ikke til erhverv eller beboelse. Der er ikke udendørs oplag af maskiner, trailere og redskaber. Facader og tag holdes i mørke, ikke-reflekterende farver. Der plantes og vedligeholdes afskærmende beplantning af hjemmehørende arter syd for hallen i mindst 3 m højde, og de eksisterende læbælter bevares. Vilkårene kan tinglyses på ejendommen.

Del B: Tilbygning til stuehuset

B1. Det ansøgte

Bygning	Tilbygning på 123 m² mod vest på stuehuset, én etage. 8,0 m bred og 15,0 m lang; den går 7,0 m forbi husets sydfacade
Indhold	Garage til to biler (45 m²), bad, garderobe, gang og soveværelse (i alt ca. 71 m² opvarmet bolig). Intet køkken
Sammenbygning	Tilbygningen bruger husets vestgavl som fælles væg og har døre til stuen og til bryggerset. Den er en udvidelse af den ene eksisterende bolig
Udseende	Nøjagtig samme stil som huset: hvide vægge, sort bølgepladetag med samme taghældning og kiphøjde (ca. 4,7 m over terræn), samme grå sokkel (ca. 0,4 m), sorte vinduer i husets mål
Samlet bolig	123 m² + 123 m² = ca. 246 m² bruttoetageareal, inklusive den integrerede garage
Placering	Ca. 6,7 m fra skel mod vest [skel bekræftes]. Garageportene vender mod den eksisterende gårdsplads. Garagens gulv ligger i sokkelhøjde som resten af huset, og gruset føres jævnt op til portene
Afløb	Det nye bad tilsluttes [ejendommens eksisterende spildevandsanlæg: afklares]
Tidsplan	Hallen opføres først. Tilbygningen opføres derefter, senest [år]

B2. Hvorfor vi mener, at tilbygningen ikke kræver landzonetilladelse

Efter planlovens § 36, stk. 1, nr. 10, kræves der ikke landzonetilladelse til til- og ombygning af helårshus, når husets samlede bruttoetageareal ikke overstiger 500 m²:

- Huset er et fritliggende helårshus med én boligenhed, opført 1992 og løbende renoveret.
- Det samlede areal bliver ca. 246 m², under halvdelen af grænsen på 500 m², også når garagen regnes med.
- Der er tale om en tilbygning, som er sammenbygget med huset og deler væg og tag med det. Der indrettes ikke en ekstra bolig; tilbygningen har intet køkken.

Vi beder kommunen bekræfte, at tilbygningen er omfattet af § 36, stk. 1, nr. 10. Mener kommunen, at den kræver landzonetilladelse, beder vi om, at denne ansøgning også behandles som ansøgning herom.

B3. Forholdet til omgivelserne

- Tilbygningen ligger op ad huset inde i ejendommens bebyggelse, bag læbæltet mod vest, og har samme højde, form og farver som huset. Den ændrer ikke bebyggelsens fremtræden i landskabet.
- Den opføres på eksisterende græsplæne og grus. Der fældes ingen træer. Placeringen ligger ikke i det område, der kan blive udsat for oversvømmelse.
- Vi er opmærksomme på, at vi selv skal sikre, at tilbygningen overholder bygningsreglementets afstands- og højdekrav, og at ejendommens jordvarmeslanger i haven mod vest skal respekteres eller lægges om.

B4. Rækkefølge

Vi ønsker at bygge hallen først og tilbygningen senere. Vi beder kommunen oplyse, om tilbygningen kan indgå i samme byggetilladelse, eller om vi skal søge byggetilladelse til den, når vi er klar.


Bilag

A0.1	Situationsplan 1:500 med hal og tilbygning
A0.2	Situationsplan på luftfoto (ubebyggede arealer)
A1.1	Hal, plan og indretning 1:100

A1.2	Hal, facader 1:100
A1.3	Hal, snit 1:50
A2.1	Hus med tilbygning, plan 1:100
A2.2	Hus med tilbygning, facader 1:100
A2.3	Tilbygning, snit 1:50
A3.1	Stald, eksisterende indretning og brug 1:100
B1	Rumlige skitser fra fire hjørner
B2	Naboernes skriftlige accept [vedlægges]

Med venlig hilsen

[navne]

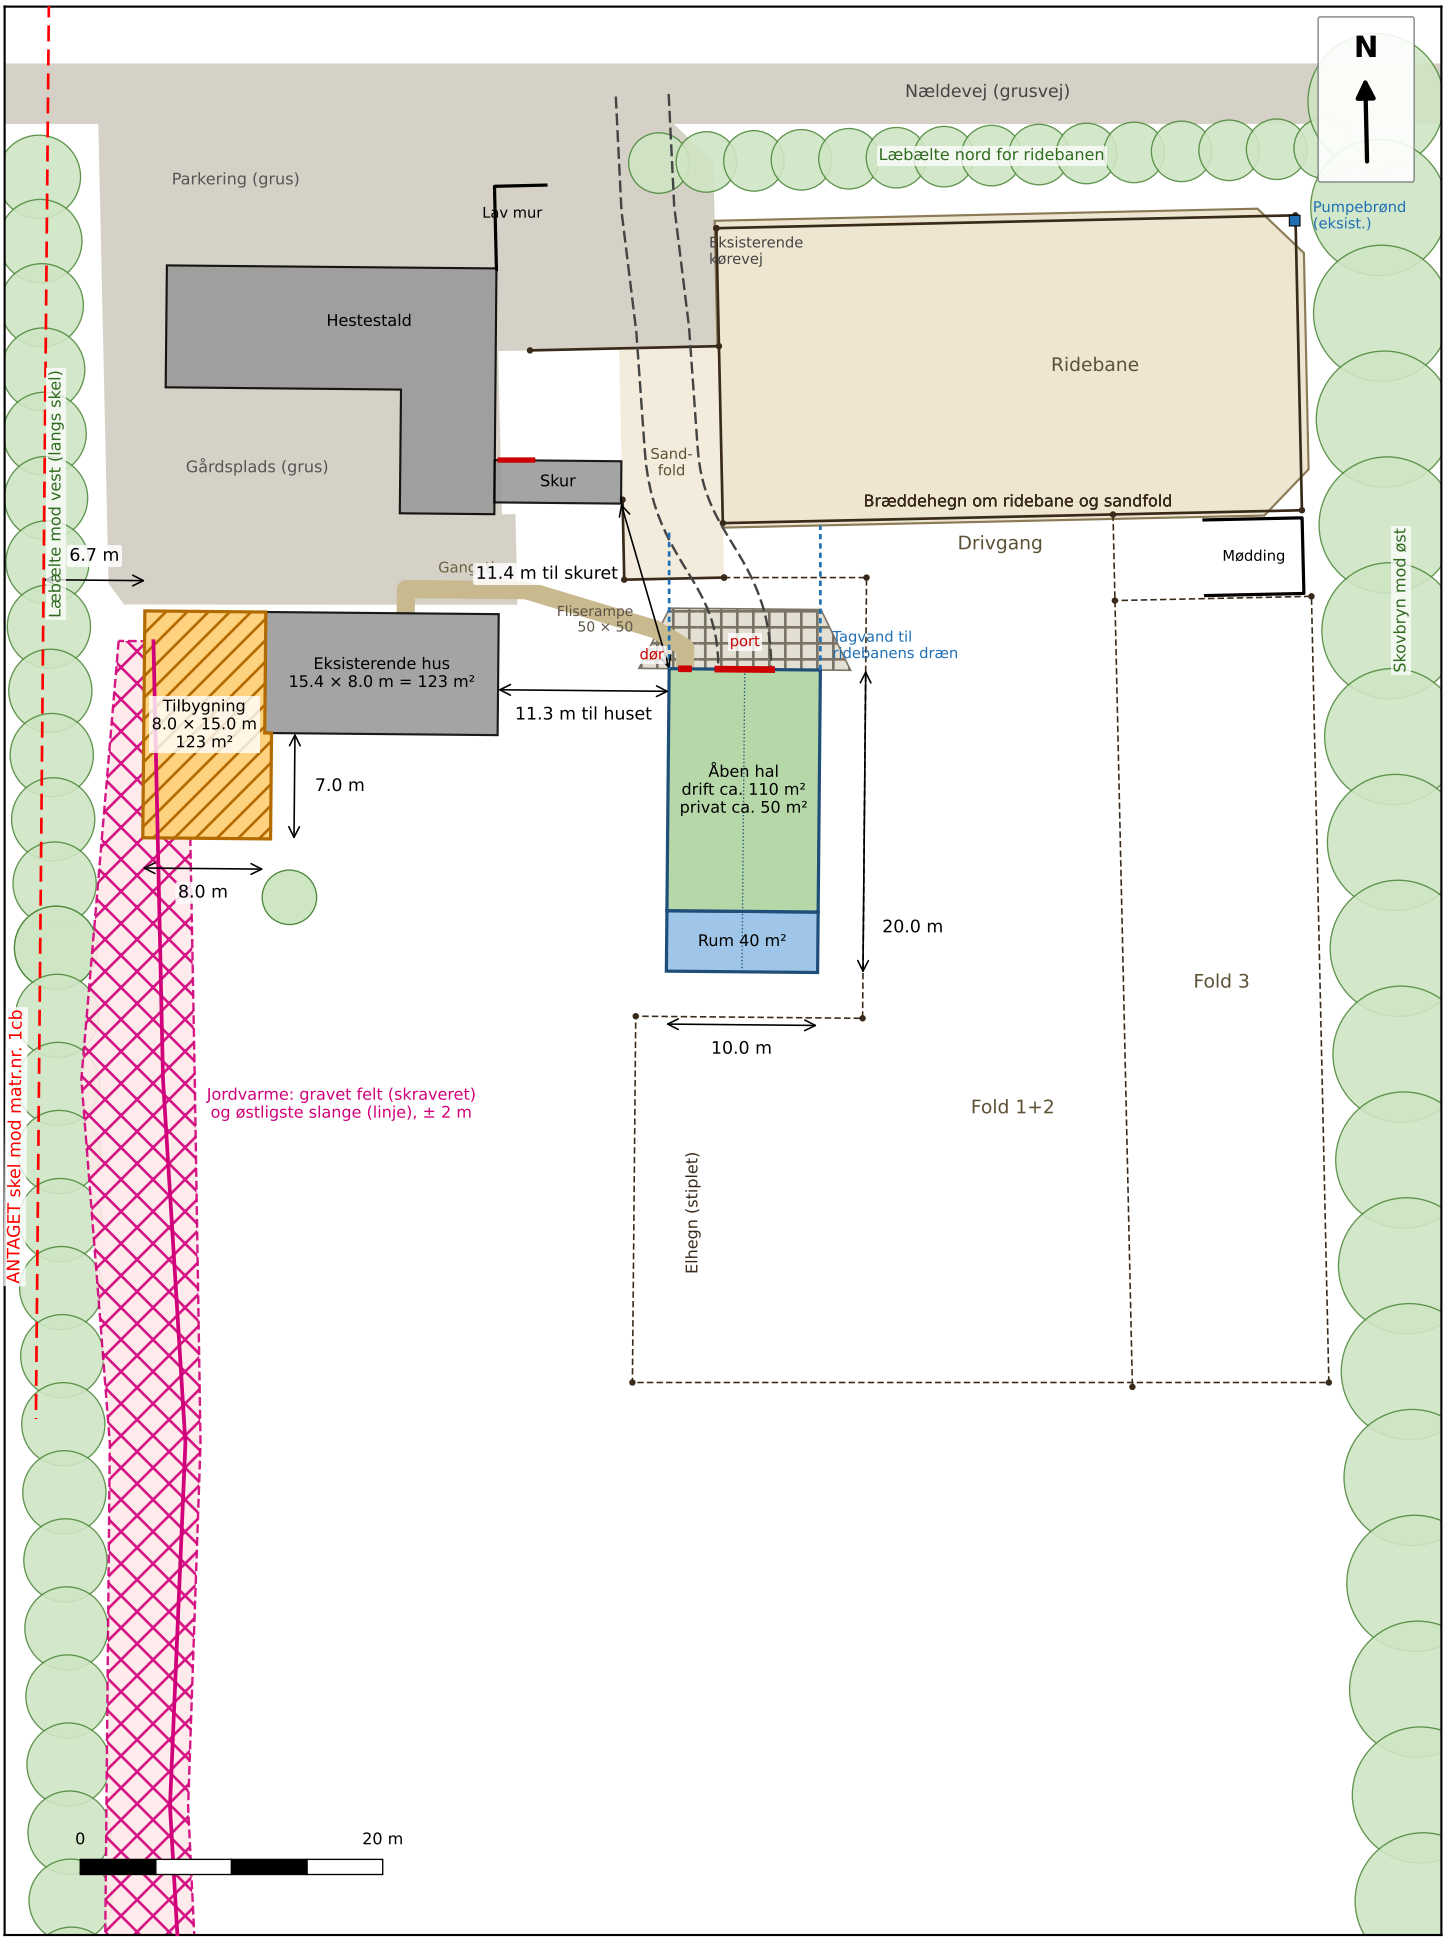

Situationsplan, Nældevej 42, 9000 Aalborg

Målestok 1:500 (A4) · Tilbygning til hus og ny hal 20 × 10 m

FORELØBIG SKITSE. Skel er antaget ud fra luftfoto.
Jordvarmezonen er anslået. Husets mål følger mæglerens plan (2024).

Bygningsomrids og vej: © OpenStreetMap-bidragydere (GeoDanmark).

BYGGESAG: Nældevej 42, 9000 Aalborg		**A0.1**
EMNE: Situationsplan	DATO: 10.10.2026	
UDFØRT AF: JB	MÅL: 1 : 500 (A4)	FORELØBIG




Situationsplan, Nældevej 42, 9000 Aalborg

Målestok 1:500 (A4) · Tilbygning til hus og ny hal 20 × 10 m

FORELØBIG SKITSE. Skel er antaget ud fra luftfoto.
Jordvarmezonen er anslået. Husets mål følger mæglerens plan (2024).

Bygningsomrids og vej: © OpenStreetMap-bidragydere (GeoDanmark). Luftfoto: Apple Kort, kun arbejdskort.

BYGGESAG: Nældevej 42, 9000 Aalborg		**A0.1**
EMNE: Situationsplan	DATO: 10.10.2026	
UDFØRT AF: JB	MÅL: 1 : 500 (A4)	FORELØBIG

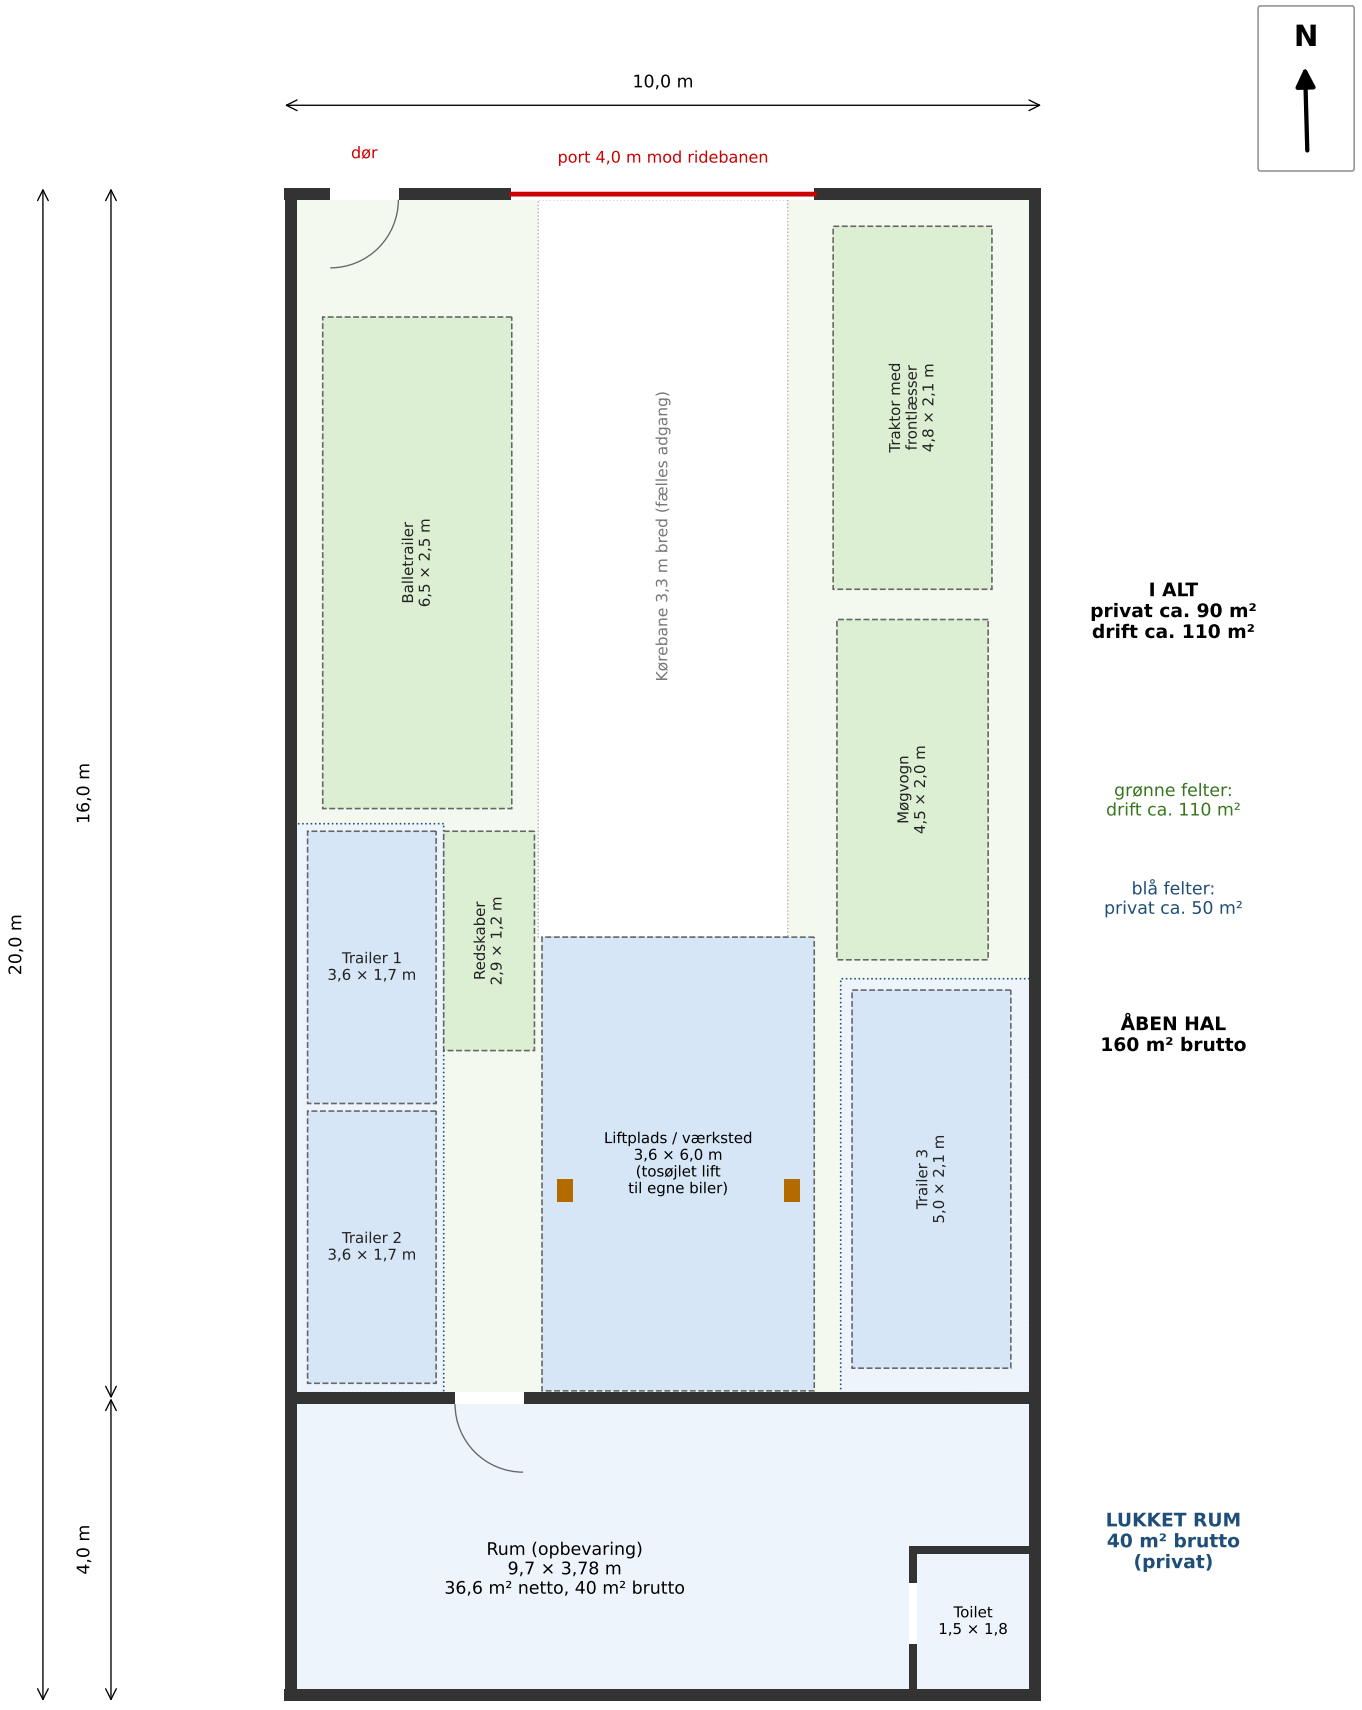

Hal, plan og indretning, Nældevej 42, 9000 Aalborg

Målestok 1:100 (A4) · Udvendigt 10,0 × 20,0 m = 200 m² · Sidehøjde 4,0 m over sokkel (sokkel 0,4 m), taghældning 30°, kip nord-sy


FORELØBIG SKITSE. Stiplede felter viser maskinernes og trailernes egne mål, som er antaget og skal erstattes med de faktiske. Vægtykkelse 15 cm er antaget. Rammernes søjler er ikke vist.

BYGGESAG: Nældevej 42, 9000 Aalborg		**A1.1**
EMNE: Ny hal, plan og indretning	DATO: 10.10.2026	FORELØBIG
UDFØRT AF: JB	MÅL: 1 : 100 (A4)	


Ny hal, facader

Vægge: sorte, matte sandwichpaneler, vandrette, 1 m høje. Tag: sorte sandwichpaneler, 30°. Sokkel: beton 0,4 m over terræn; gulv i soklens overkant. Sidehøjde 4,0 m over sokkel. Højder i meter over terræn.


Facade mod nord (port og dør mod ridebanen)

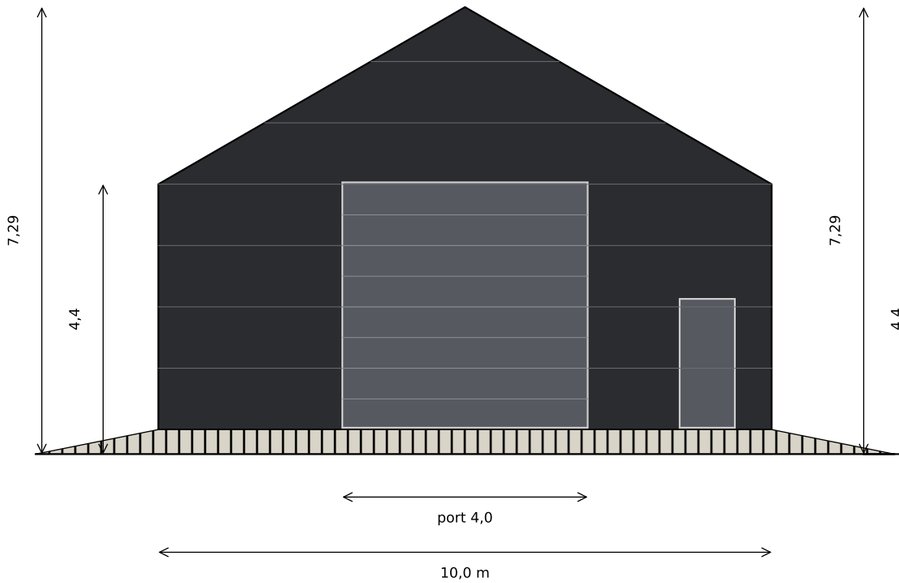


Facade mod øst

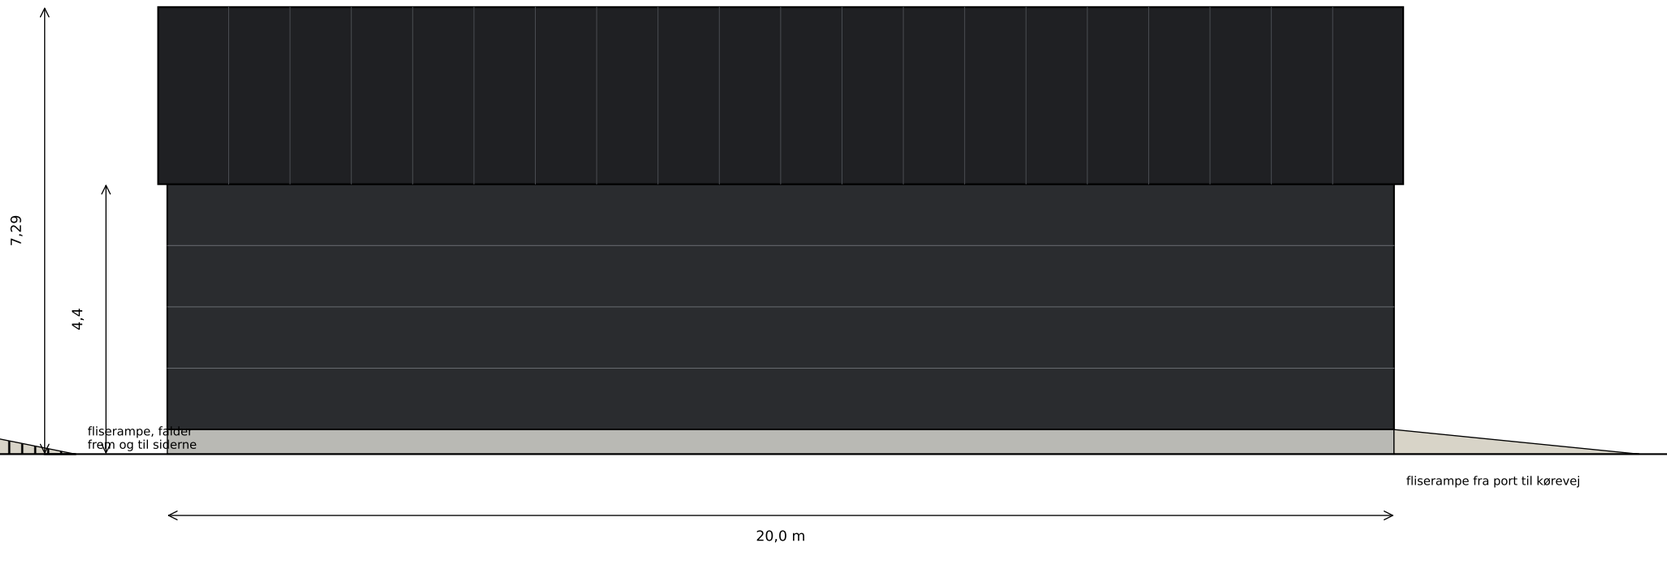

Facade mod syd (ingen åbninger)

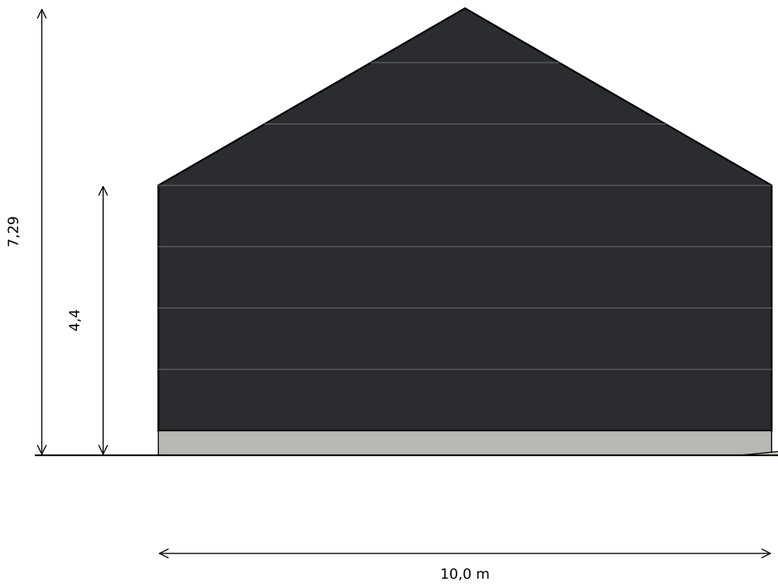


Facade mod vest

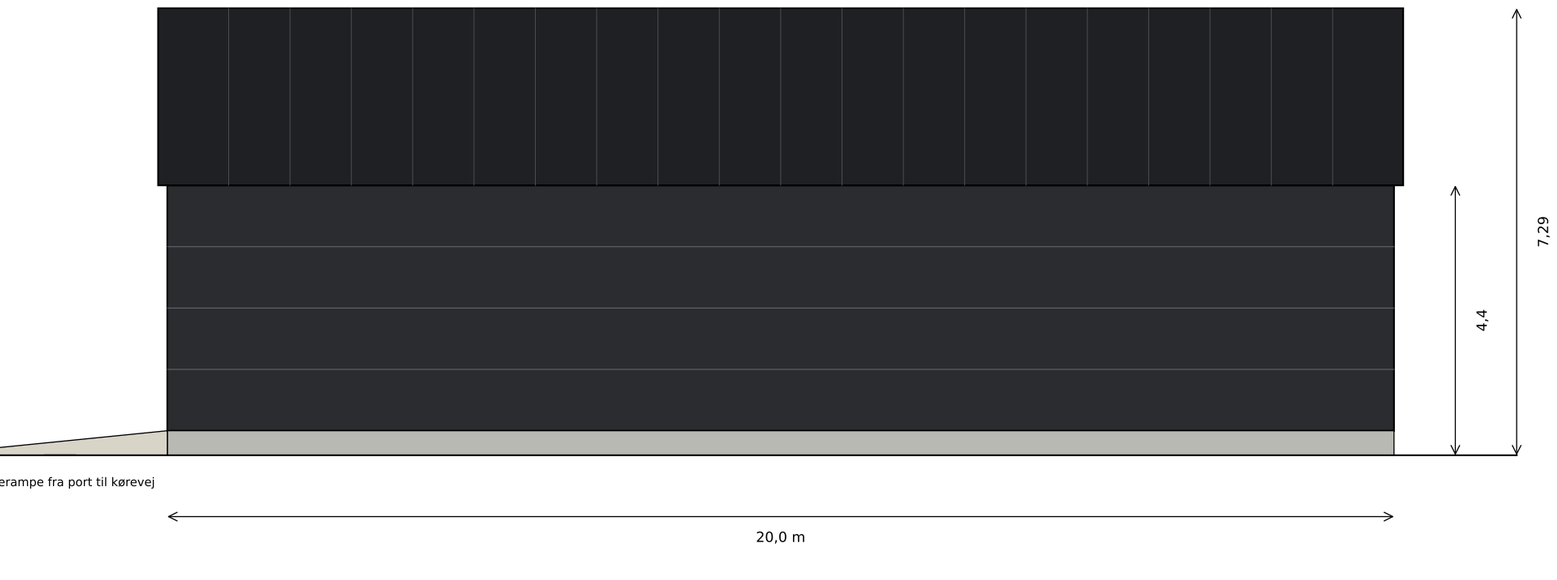

FORELØBIG TEGNING. Terræn er forudsat vandret. Panelernes dækbredde (FALK 1060 WB er 1,06 m) og portens endelige højde er ikke fastlagt.

BYGGESAG: Nældevej 42, 9000 Aalborg		**A1.2**
EMNE: Ny hal, facader	DATO: 10.10.2026	
UDFØRT AF: JB	MÅL: 1 : 100 (A3)	FORELØBIG

Snit A-A gennem en mellemramme (set mod nord)

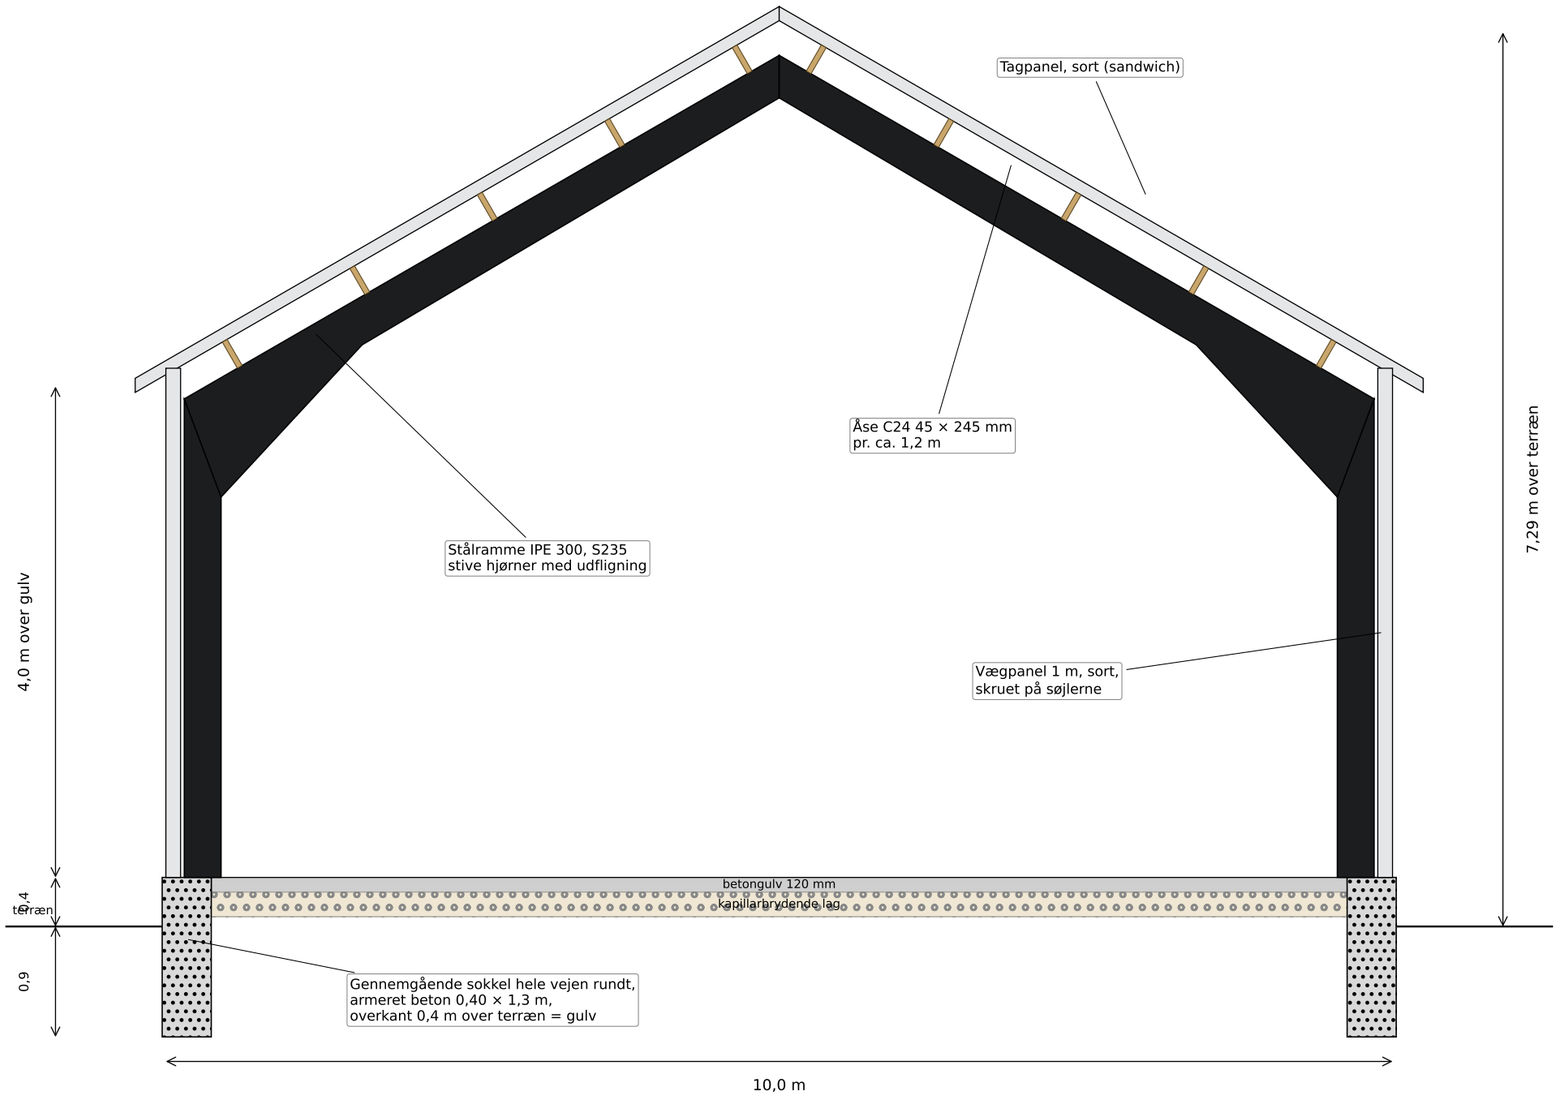

OVERSLAGSBEREGNING, hovedresultater

Ramme: IPE 300 S235, rammeafstand 5,0 m

Sne: s_k = 1,0 kN/m², μ = 0,8 (jævn) og 1,2 (ophobning vest)

Vind: q_p = 0,78 kN/m²

Største moment i rammehjørne: 52,3 kNm

Største moment i kip: 19,7 kNm

Udnyttelse tværsnit / søjle / spær: 0,50 / 0,56 / 0,56

Nedbøjning kip (sne): 7 mm (krav 50 mm)

Udbøjning tagfod (vind): 25 mm (krav 27 mm)

Fundament: gennemgående sokkel 0,40 × 1,3 m

Reaktioner pr. rammefod (regningsmæssige):

tryk 54,5 kN, løft 16,4 kN, vandret 18,9 kN


Åse: C24 45 × 245 mm ved 5 m spænd

Vægkryds: træk 20,4 kN i diagonal

Ikke eftervist: kipning, samlinger, gavlrammer, port,

jordens bæreevne. Se docs/hal-statik-overslag.md.

Momentkurve, K2 (sneophobning på vestlig tagflade)
største moment 52,3 kNm

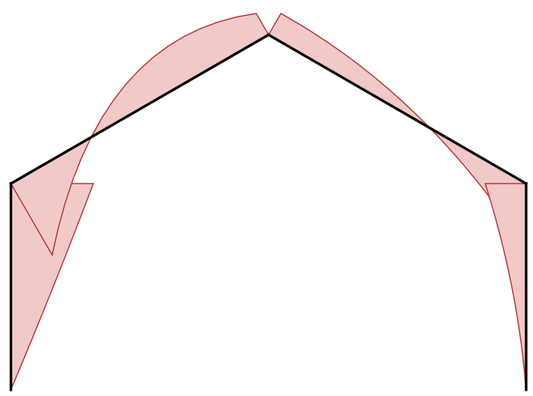

FORELØBIG TEGNING med overslagsberegning. Profiler, åse og fundamenter er vejledende og skal fastlægges af den projekterende.

BYGGESAG: Nældevej 42, 9000 Aalborg		**A1.3**
EMNE: Ny hal, snit A-A og overslag	DATO: 10.10.2026	FORELØBIG
UDFØRT AF: JB	MÅL: 1 : 50 (A3)	



Tilbygning og eksisterende hus, plan, Nældevej 42, 9000 Aalborg

Målestok 1:100 (A3) · Tilbygning 15,0 m lang, 7,55 m bred indvendigt, 123 m² brutto, heraf omkring 71 m² opvarmet bolig

FORELØBIG SKITSE. Det eksisterende hus er tegnet efter ejendomsmæglerens vejledende plantegning fra 2024 (ikke målfast) og skal måles op. Vægtykkelser i tilbygningen er antaget:


ydervæg 45 cm, væg garage/bolig 15 cm, indervægge 10 cm. Brandadskillelse mellem garage og bolig (herunder døren til bryggerset) er ikke dimensioneret. Bryggersets vindue i vestgavlen forsvinder. Langs huset bruges husets eksisterende vestgavl som fælles væg.

BYGGESAG: Nældevej 42, 9000 Aalborg		**A2.1**
EMNE: Hus med tilbygning, plan	DATO: 10.10.2026	FORELØBIG
UDFØRT AF: JB	MÅL: 1 : 100 (A3)	

Hus med tilbygning, facader


Tilbygningen (gul) udføres i samme stil som huset: hvide vægge, sort bølgepladetag, sorte vinduer i husets standardmål. På tegningen er den fremhævet med gul væg. Grå sokkel ca. 0,4 m som på huset. Højder i meter over terræn.

Facade mod nord

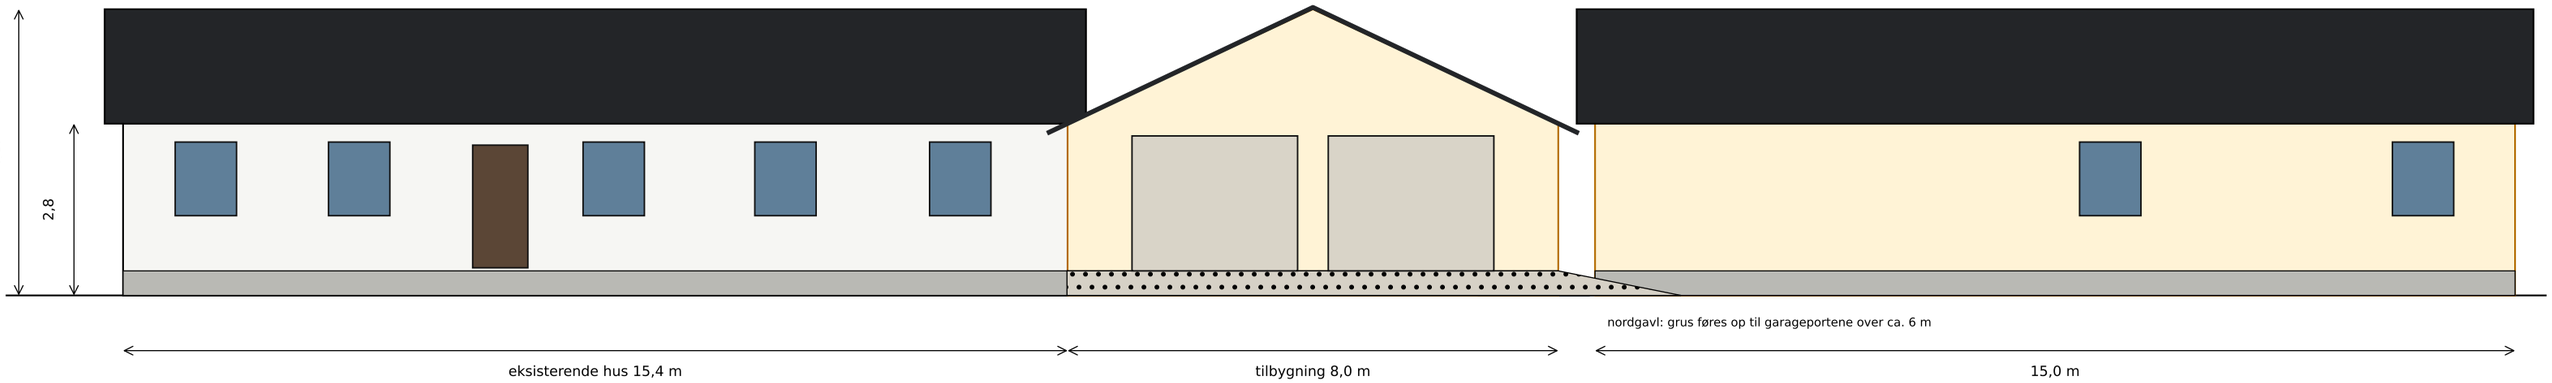

Facade mod vest (tilbygning)

Facade mod syd

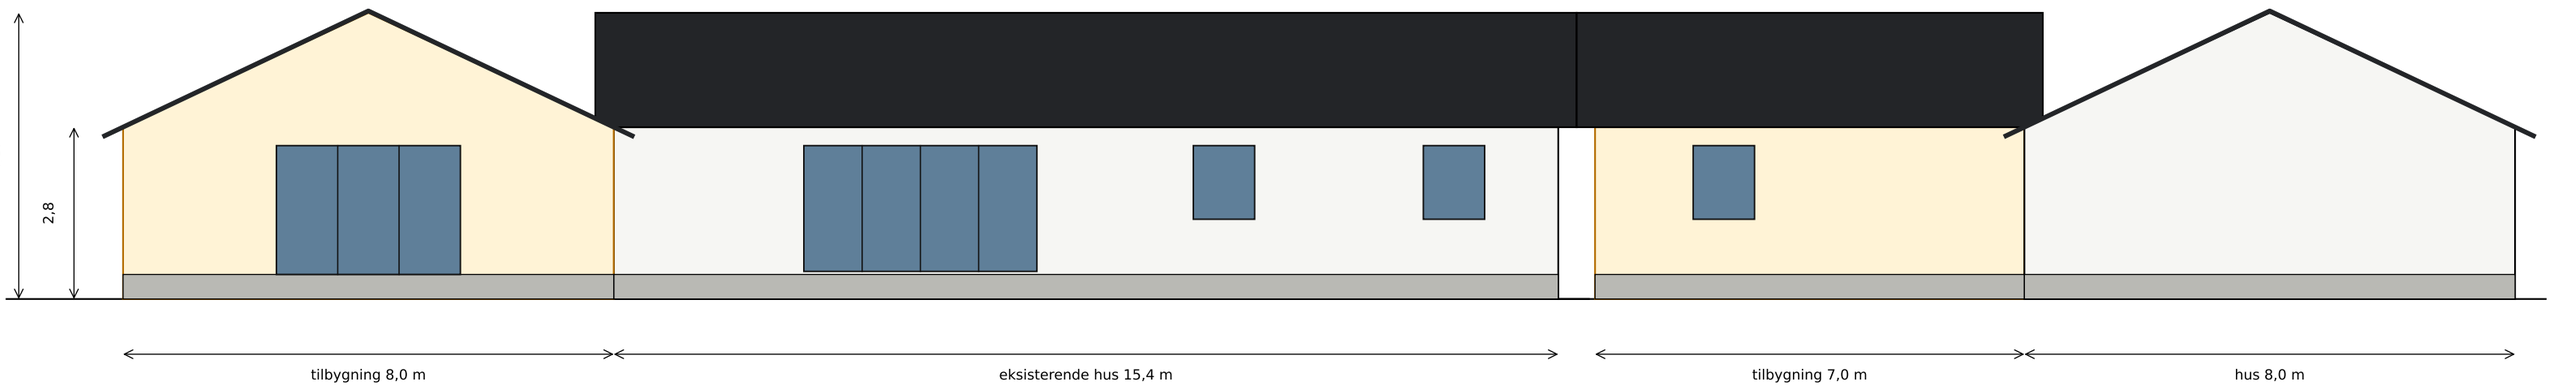

Facade mod øst


FORELØBIG TEGNING. Husets højder (tagfod 2,8 m over terræn, sokkel 0,4 m, 25°) og åbninger er anslået fra fotos og mæglerens plan og skal måles op.

Stald og skur er ikke vist. Springet på 45 cm i tilbygningens østvæg er ikke vist.

BYGGESAG: Nældevej 42, 9000 Aalborg		**A2.2**
EMNE: Hus med tilbygning, facader	DATO: 10.10.2026	
UDFØRT AF: JB	MÅL: 1 : 100 (A3)	FORELØBIG

Snit B-B gennem soveværelset (set mod nord)

Tal på stængerne: normalkraft i kN for sne på hele taget (K1). Rød = tryk, blå = træk.

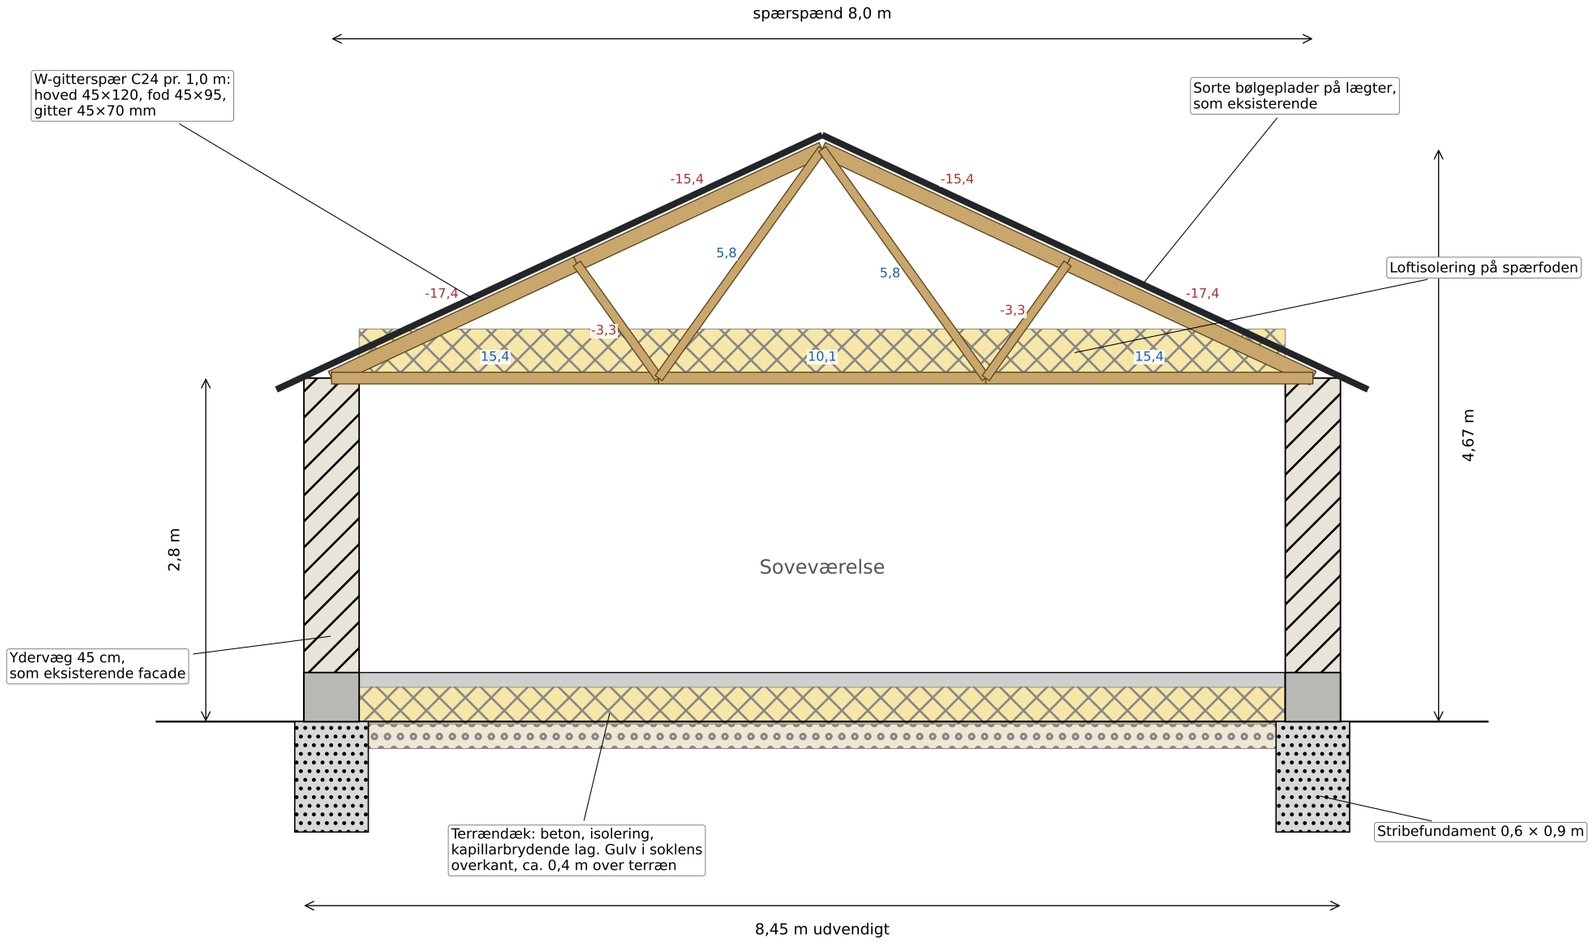

OVERSLAGSBEREGNING, hovedresultater

Spær: W-gitterspær C24, spænd 8,0 m, afstand 1,0 m

Sne: s_k = 1,0 kN/m², μ = 0,8 og 1,2 (ophobning vest)

Egenlast tag 0,35 og loft 0,35 kN/m², opbevaring 0,5 kN/m²

Udnyttelse spærhoved: 0,88

Udnyttelse spærfod: 0,80

Udnyttelse gitterstænger: 0,28

Lodret last pr. spær: 9,8 kN (9,8 kN/m væg)

Løft fra vind pr. spær: 1,4 kN

Linjelast på fundament: ca. 17,8 kN/m

Ikke eftervist: tandpladesamlinger, bæring på husets gavl, skotrender, stabilitet, jordens bæreevne.


Se docs/tilbygning-statik-overslag.md.

FORELØBIG TEGNING med overslagsberegning. Spær dimensioneres og leveres af spærfabrik. Vægopbygning, gulv og fundament er principielle.

BYGGESAG: Nældevej 42, 9000 Aalborg		**A2.3**
EMNE: Tilbygning, snit B-B og overslag	DATO: 10.10.2026	FORELØBIG
UDFØRT AF: JB	MÅL: 1 : 50 (A3)	

Stald, BBR-bygning 2: eksisterende indretning og brug

Alle rum er i brug: stald, sadelrum og bad til hesteholdet og vestenden med det gamle stuehus til gæsteværelser. Der er ingen ledige rum til maskiner, trailere eller opbevaring.

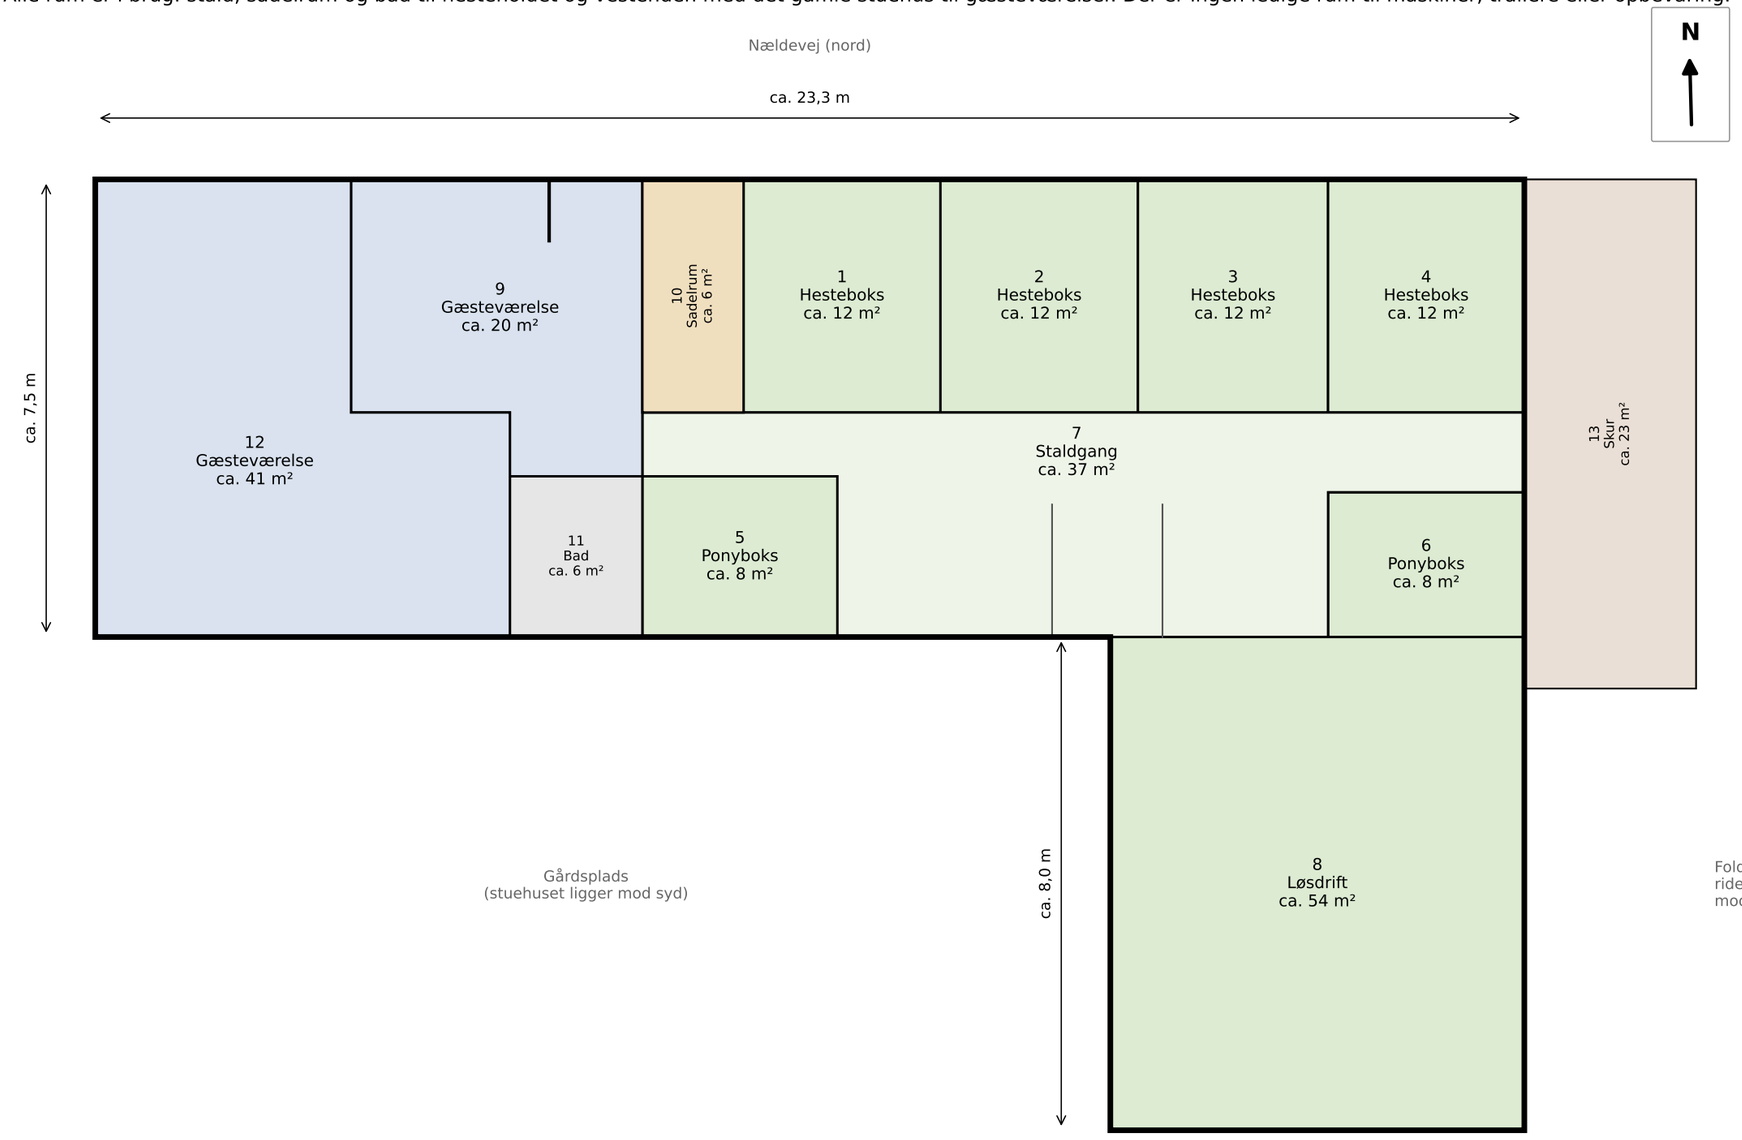

Nr.	Rum, areal og brug
1	**Hesteboks, ca. 12 m²**
	Opstaldning af ejendommens heste
2	**Hesteboks, ca. 12 m²**
	Opstaldning af ejendommens heste
3	**Hesteboks, ca. 12 m²**
	Opstaldning af ejendommens heste
4	**Hesteboks, ca. 12 m²**
	Opstaldning af ejendommens heste
5	**Ponyboks, ca. 8 m²**
	Opstaldning af ejendommens ponyer
6	**Ponyboks, ca. 8 m²**
	Opstaldning af ejendommens ponyer
7	**Staldgang, ca. 37 m²**
	Adgang til boksene, strigleplads, foder og udmugning [bekræftes]
8	**Løsdrift, ca. 54 m²**
	Løsdrift med dybstrøelse, hestene går frit ud og ind til foldene
9	**Gæsteværelse, ca. 20 m²**
	Gæsteværelse til husstandens private gæster. Ét rum; kun en støttevæg på 1 m ved ydervæggen
10	**Sadelrum, ca. 6 m²**
	Sadler, trenser, seletøj og rideudstyr. Tidligere værksted
11	**Bad, ca. 6 m²**
	Bad og toilet til stalden
12	**Gæsteværelse, ca. 41 m²**
	Ejendommens gamle stuehus. Bruges som gæsteværelse til husstandens private gæster
13	**Skur, ca. 23 m²**
	Åbnede wrapballer opbevares her i tørvejr. Ejendommens eneste udhus (byggesag 2020-1967)

Folde og ridebane mod øst

Sammentælling (rumarealer, ca.)


Hestehold (bokse, staldgang, løsdrift):	155 m²
Sadelrum og bad:	12 m²
Gæsteværelser:	61 m²

Stalden er registreret med 284 m² i BBR. Forskellen skyldes vægge, og at planen ikke er målfast. Skuret (nr. 13) er ikke en del af stalden.


FORELØBIG TEGNING efter mæglerens vejledende plan (ikke målfast). Rumarealer er regnet til vægmidte og er omtrentlige.
Døre, vinduer og porte er ikke vist. Skurets placering og mål er efter situationsplanen.

BYGGESAG: Nældevej 42, 9000 Aalborg		**A3.1**
EMNE: Stald, eksisterende indretning og brug	DATO: 10.10.2026	FORELØBIG
UDFØRT AF: JB	MÅL: 1 : 100 (A3)	


Set fra sydøst

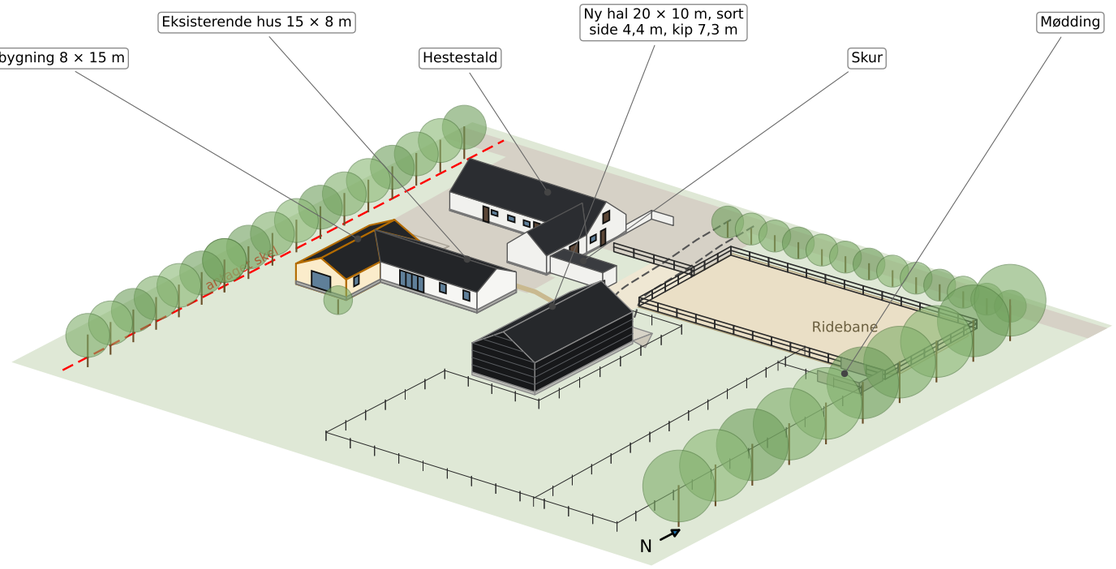


Set fra sydvest

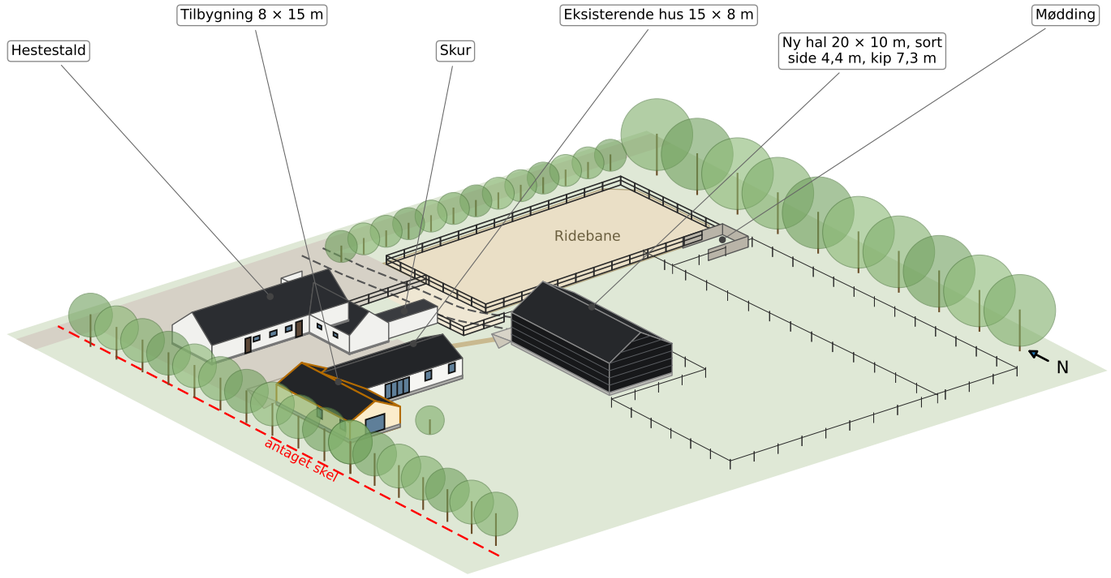

Set fra nordvest

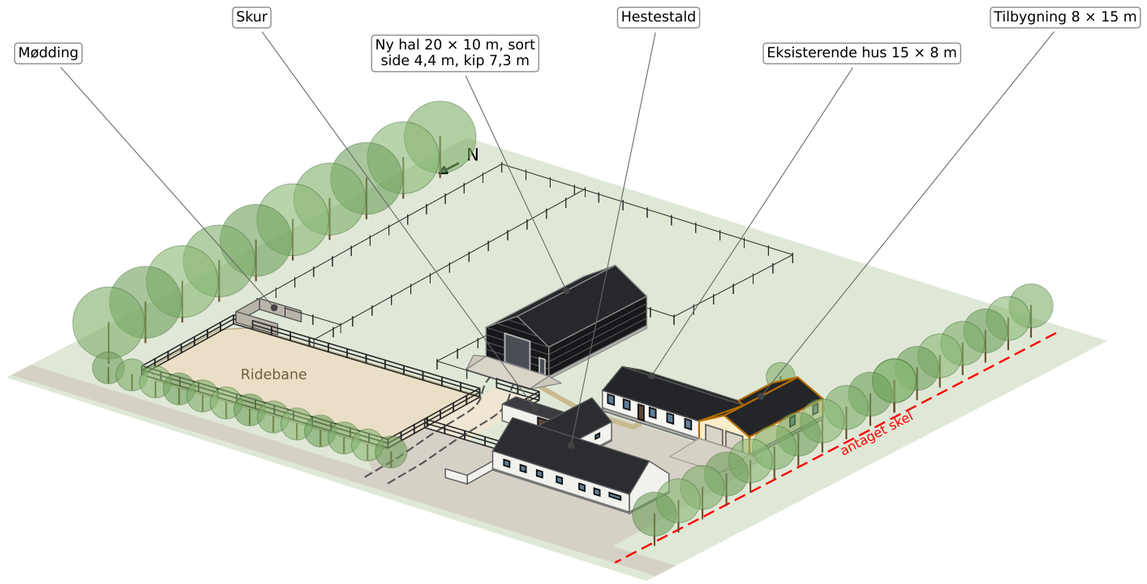

Set fra nordøst

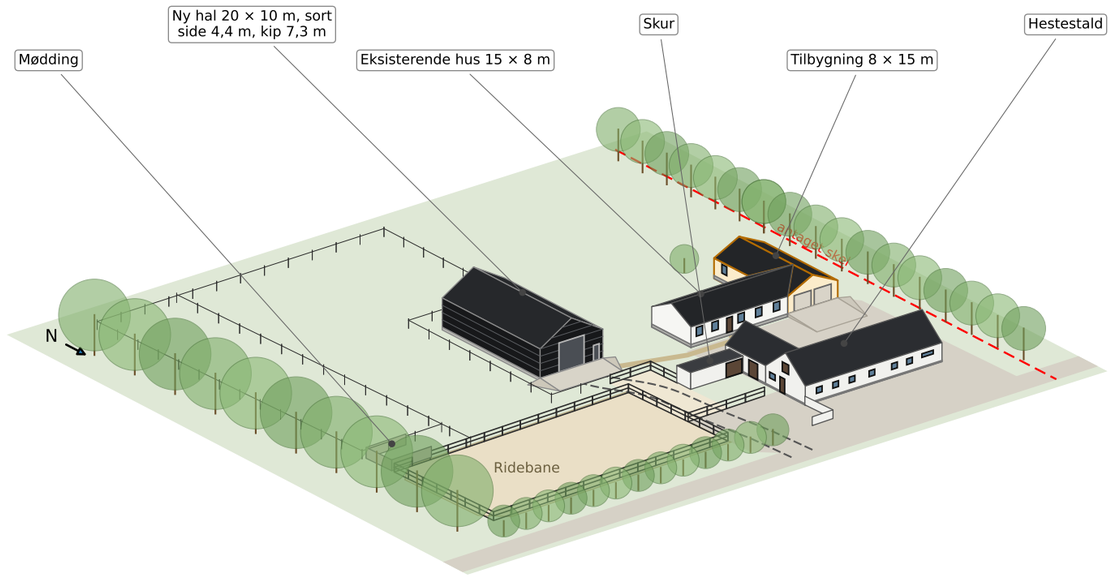

Rumlige skitser fra fire hjørner, Nældevej 42, 9000 Aalborg

FORELØBIGE SKITSER i parallelprojektion, ikke målfaste. Hallens mål er de ønskede. Tagfod og taghældning på hus og tilbygning (2,8 m, 25°, anslået fra foto) og stald (2,6 m, 38°) samt skurets højde er anslået fra fotos og skal måles op.

Farver og åbninger i hus og stald følger mæglerens vejledende plantegning (2024) og ejers fotos og er ikke opmålt. Ridebane, hegn, grusarealer og læbælter efter luftfoto (træhøjder skønnet). Tilbygningen er fremhævet med gul væg.