Aalborg Kommune, Byggeri, BL
Stigsborg Brygge 5, 9400 Nørresundby

By og Land
Byggeri, BL
Stigsborg Brygge 5
9400 Nørresundby

Mandag 9-15
Tirsdag 9-15
Onsdag 9-15
Torsdag 9-17
Fredag 9-14

Init:
NSS

Sagsnr.:
S2022-180624

Ejendomsnummer
421335

Matr.nr.
17K, NØRHOLM BY, NØRHOLM

10. februar 2023

Landzonetilladelse

Nørholmsvej 270, 9000 Aalborg

matr.nr. 17K, NØRHOLM BY, NØRHOLM

På baggrund af din ansøgning modtaget den 03-10-2022 meddeler Aalborg Kommune hermed,

Landzonetilladelse til opførelse af garage 75 m²

Redegørelse
Ejendommen på 4416 m² er beliggende i landzone. Herudover er den ansøgte placering omfattet af Større sammenhængende landskaber og kystnærhedszonen.

Der er foretaget en vurdering efter Habitatbekendtgørelsens § 7. Den ansøgte placering ligger ca. 527 m fra nærmeste Natura 2000-område. I kraft af afstanden vurderer kommunen ikke, at der er risiko for, at projektet i sig selv eller i forbindelse med andre aktuelle planer og projekter kan give anledning til en væsentlig påvirkning af Natura 2000-området. Projektet vurderes således ikke at have negativ betydning for områdets naturindhold.

Det ansøgte projekt vurderes ikke at have væsentlig betydning for varetagelsen af de planmæssige interesser, som skal forvaltes jf. kommuneplanens øvrige udpegninger, som ejendommen er omfattet af.

Naboorientering
Der er ikke gennemført naboorientering efter planlovens § 35, stk. 5, idet det ansøgte efter kommunalbestyrelsens skøn, er af underordnet betydning for naboerne. Der er lagt vægt på at der opføres en garage. Det vurderes at en garage er af underordnet betydning fro naboer, hvorfor der ikke gennemføres naboorientering for denne.

Begrundelse
Der meddeles tilladelse til det ansøgte, da det er vurderet, at det ikke vil medføre nogen væsentlig forringelse af natur-, miljø-, eller landskabelige værdier. Herudover er der lagt afgørende vægt på at den ansøgte garage opføres i tilknytning til ejendommens eksisterende bebyggelse. Der er lagt vægt på garagens størrelse på 75 m² ligger indenfor, hvad der normalvis kan meddeles landzonetilladelse til.

Lovgrundlag
"Hovedformålet med zoneinddelingen er at forhindre spredt bebyggelse i det åbne land og dermed sikre en klar grænse mellem by og land, og at byudvikling sker, hvor der gennem planlægningen er åbnet mulighed for det. Sigtet er at forbeholde landzonen til jordbrugserhvervene og at tilgodese landskabs- og naturværdier, samtidig med at egentlig byudvikling sker, hvor planlægningen åbner mulighed for det. Zoneinddelingen skaber herved en klar grænse mellem by og land, for hermed at fremme bevarelsen af bl.a. natur- og kulturhistoriske værdier, og miljøkonflikter undgås.

Samtidig skal planloven bidrage til at gøre landdistrikterne levedygtige. Med lovændringen i 2017 er planlovens formålsparagraf (planlovens § 1) ændret, og der er gennemført en række generelle lempelser af landzonereglerne for at skabe vækst og udvikling i landdistrikterne.

Hovedreglen er, at der i landzone ikke må foretages udstykning, opføres ny bebyggelse eller ske ændring i anvendelsen af bestående bebyggelser og ubebyggede arealer uden landzonetilladelse fra kommunalbestyrelsen, jf. planlovens § 35, stk. 1. Der er således som udgangspunkt krav om forudgående tilladelse til alle ændringer i det bestående. Loven indeholder dog en række væsentlige undtagelser fra kravet om tilladelse, jf. §§ 36 og 37. "[1]

Gyldighed
Tilladelsen bortfalder, hvis den ikke udnyttes inden 5 år efter, at den er meddelt eller ikke har været udnyttet i 5 på hinanden følgende år, medmindre andet udtrykkeligt fremgår af tilladelsen jf. planlovens § 56, stk. 2.

Offentliggørelse
Afgørelsen vil blive offentliggjort på Aalborg Kommunes hjemmeside www.aalborg.dk/annoncer, torsdag den 16-02-2023 eller snarest muligt derefter, jf. planlovens § 35, stk. 8. Hvis der indgives klage, vil kommunen straks give meddelelse herom.

Klagemuligheder
Tilladelsen kan påklages efter reglerne i vedlagte klagevejledning, hvor klagefristen er 4 uger fra den dag, tilladelsen er offentliggjort. Tilladelsen må ikke udnyttes, før klagefristen er udløbet.

En eventuel klage vil have opsættende virkning for byggeriet, medmindre klagemyndigheden beslutter andet.

Venlig hilsen

Nicolaj Svendsen
Byggesagsbehandler - Team Land

Direkte tlf.: 25202026

Kopi til:

[1] Vejledning om landzoneadministration - Vejledning af 13. juli 2018, opdateret november 2019

Danmarks Naturfredningsforening – CVR: 60804214
Dansk Ornitologisk Forening – CVR: 54752415 samt CVR: 35320296
Friluftsrådet, kreds Himmerland-Aalborg – CVR: 56230718

Du kan altid kontakte Aalborg Kommune sikkert på www.aalborg.dk/kontakt eller via Digital Post på www.borger.dk.
Har du brug for hjælp til Digital Post, kan du ringe til Den Digitale Hotline på 7020 0000.
Læs om dine rettigheder og hvordan vi behandler personoplysninger på www.aalborg.dk/gdpr.

Klagevejledning jf. planlovens kap. 14
Du kan klage over retlige spørgsmål samt kommunens vurdering. Det vil sige, at du f.eks. kan klage, hvis du mener, at kommunen ikke har haft hjemmel til at træffe afgørelsen eller hvis du er uenig i kommunens vurdering. Enhver med retlig interesse i sagens udfald kan klage f.eks. ansøgere og naboer samt visse landsdækkende foreninger og organisationer. Klage til Planklagenævnet over en administrativ afgørelse skal være indgivet skriftligt inden 4 uger efter, at afgørelsen er meddelt. Er afgørelsen offentligt bekendtgjort, regnes klagefristen dog altid fra bekendtgørelsen.
I tilfælde, hvor en afgørelse træffes indirekte og således ikke meddeles og offentliggøres, regnes fristen fra det tidspunkt, hvor klageren har fået kendskab til afgørelsen. Hvis klagefristen udløber på en lørdag eller en helligdag, forlænges fristen til den følgende hverdag.
Klage til Planklagenævnet indgives skriftligt til den myndighed, der har truffet afgørelsen, ved anvendelse af digital selvbetjening (Klageportalen, der findes på www.borger.dk og www.virk.dk) Endvidere skal efterfølgende kommunikation om klagesagen ske ved anvendelse af digital selvbetjening. En klage anses for indgivet, når den er tilgængelig for myndigheden. Det er gebyrpålagt at klage. Læs mere om klageregler og gebyrer på www.naevneneshus.dk.
Planklagenævnet skal som udgangspunkt afvise en klage, som ikke er indgivet ved digital selvbetjening. Nævnet kan undlade at afvise en klage, som ikke er indgivet ved digital selvbetjening, hvis der foreligger særlige forhold, der gør, at klager ikke må forventes at kunne anvende digital selvbetjening.
Hvis du vil indbringe afgørelsen for domstolene, skal dette ske inden 6 måneder fra afgørelsens modtagelse.



Nørholmsvej 270, 9000 Aalborg
Landzonetilladelse til opførelse af garage på 75 m²

Tidspunkt: 16-02-2023 09:38:00
Udskrevet af: Nicolaj Svendsen
Målestoksforhold: 1:10000

Jordstykke

Jordstykke - skel

Papirformat: A3

17d

17c

17k

17g

16r

16l

17h

7000l

17n


16k

El forsyning

Eksisterende Ladestation

Færch & Co.
Halkærvej 22, 9200 Aalborg SV
CVR: 89 30 56 16
Tlf: 98 18 62 20
mail@faerch-co.dk


© GeoDanmark

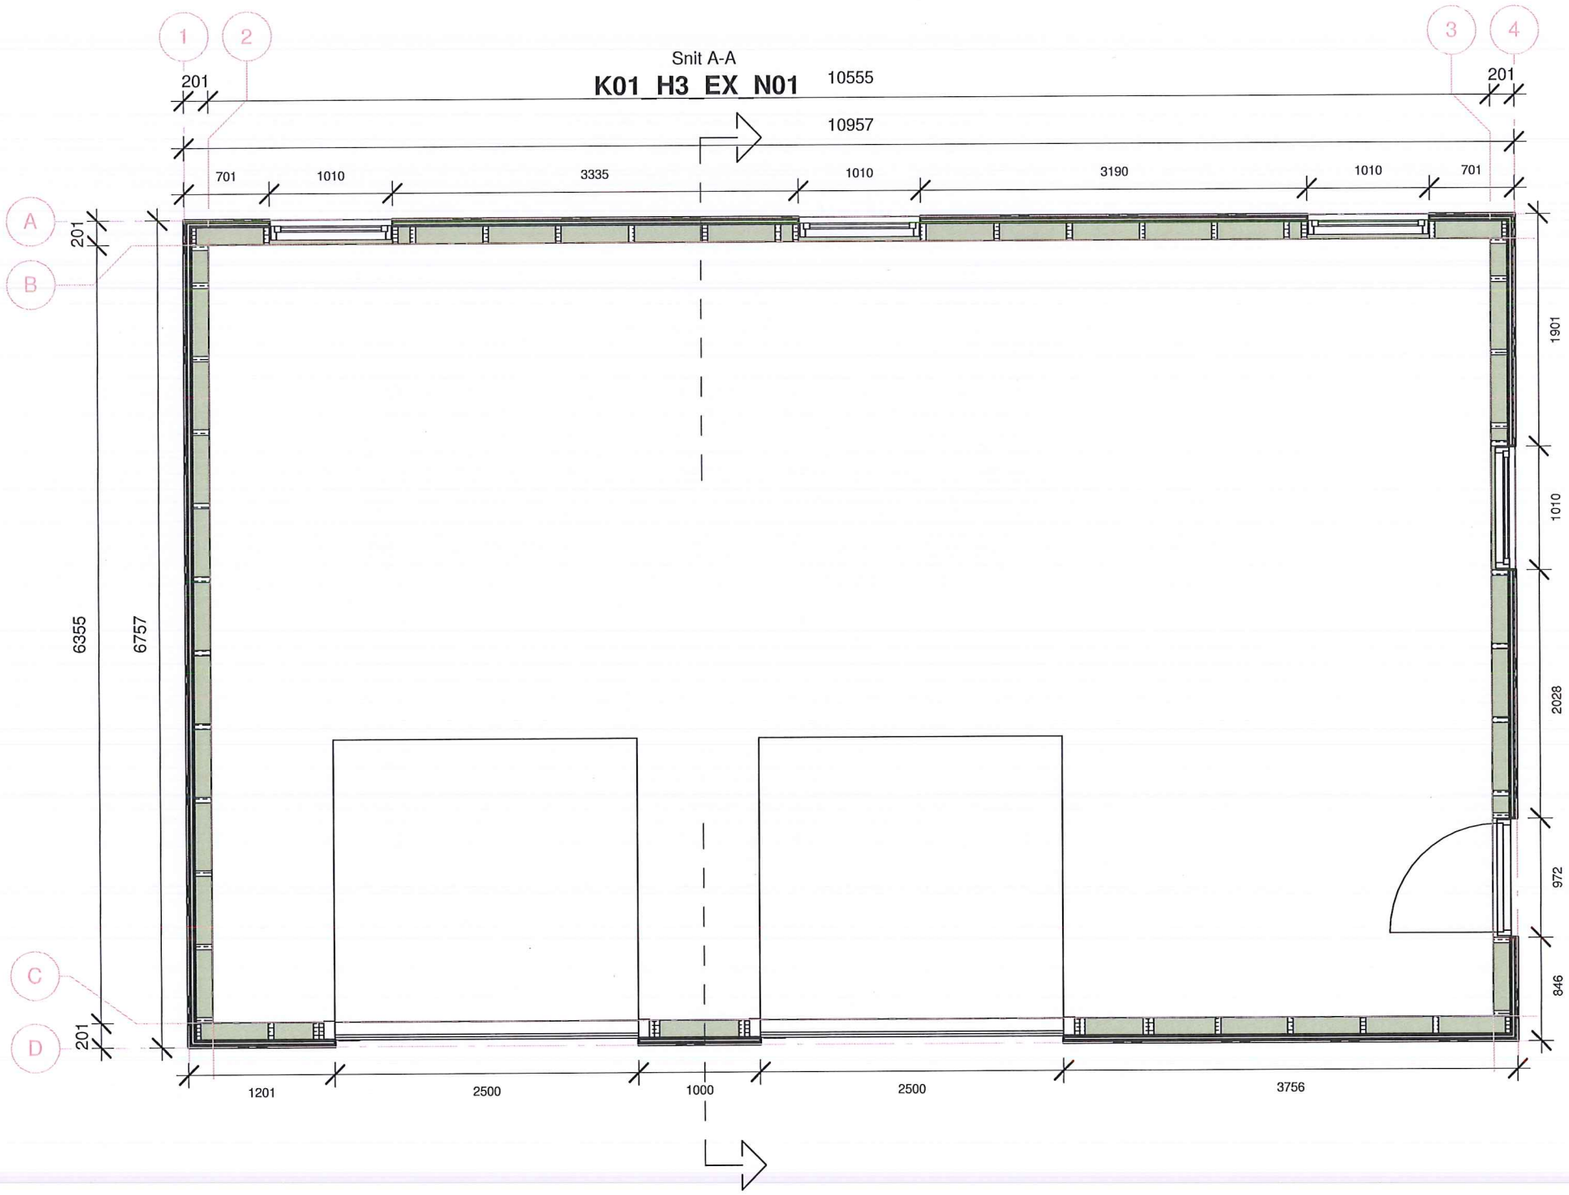


Færch & Co.
BYGGER PÅ TRADITIONER

BYGGESAG: Nørholmsvej 270, Garage	DATO:07.10.2021	K01_H1_EST_N02
EMNE: Stue, terræn	MÅL: 1 : 50	
UDFØRT AF: JTM	REV:	

Snit A-A
K01_H3_EX_N01

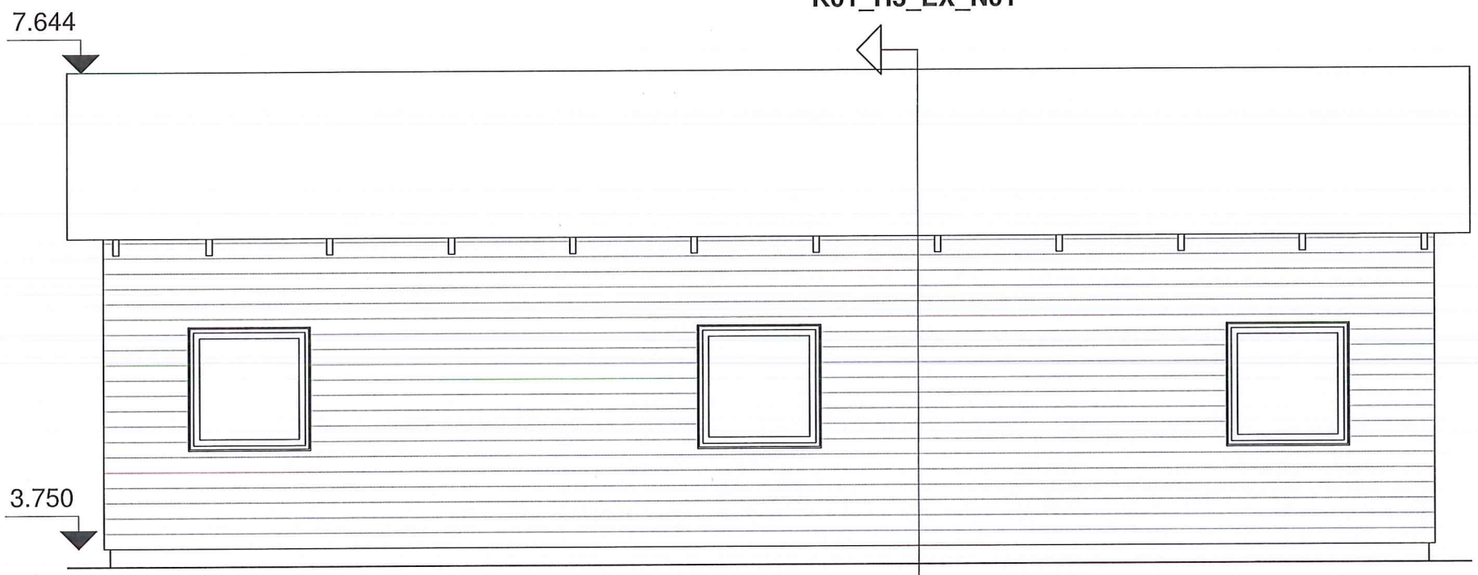


Facade nord

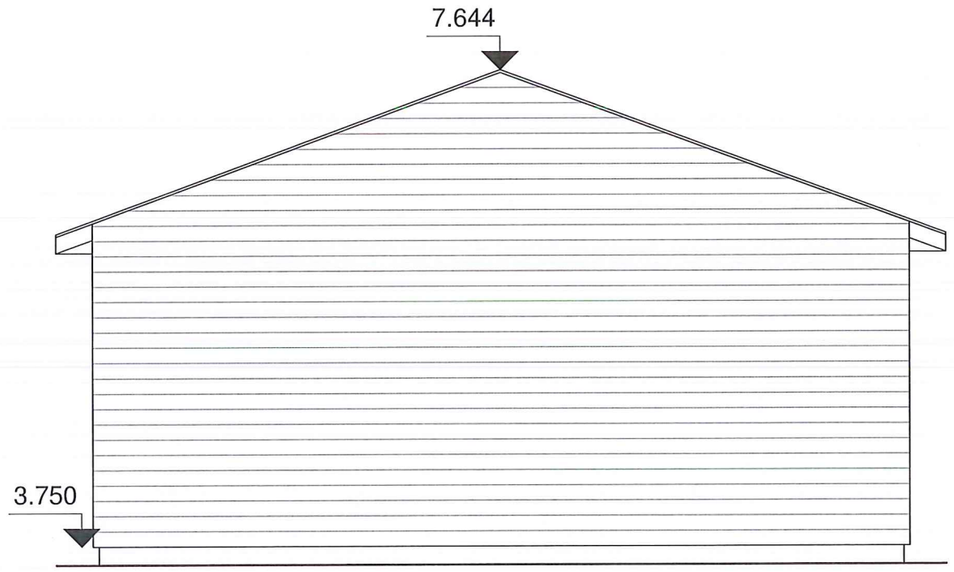


Facade vest

Snit A-A
K01_H3_EX_N01

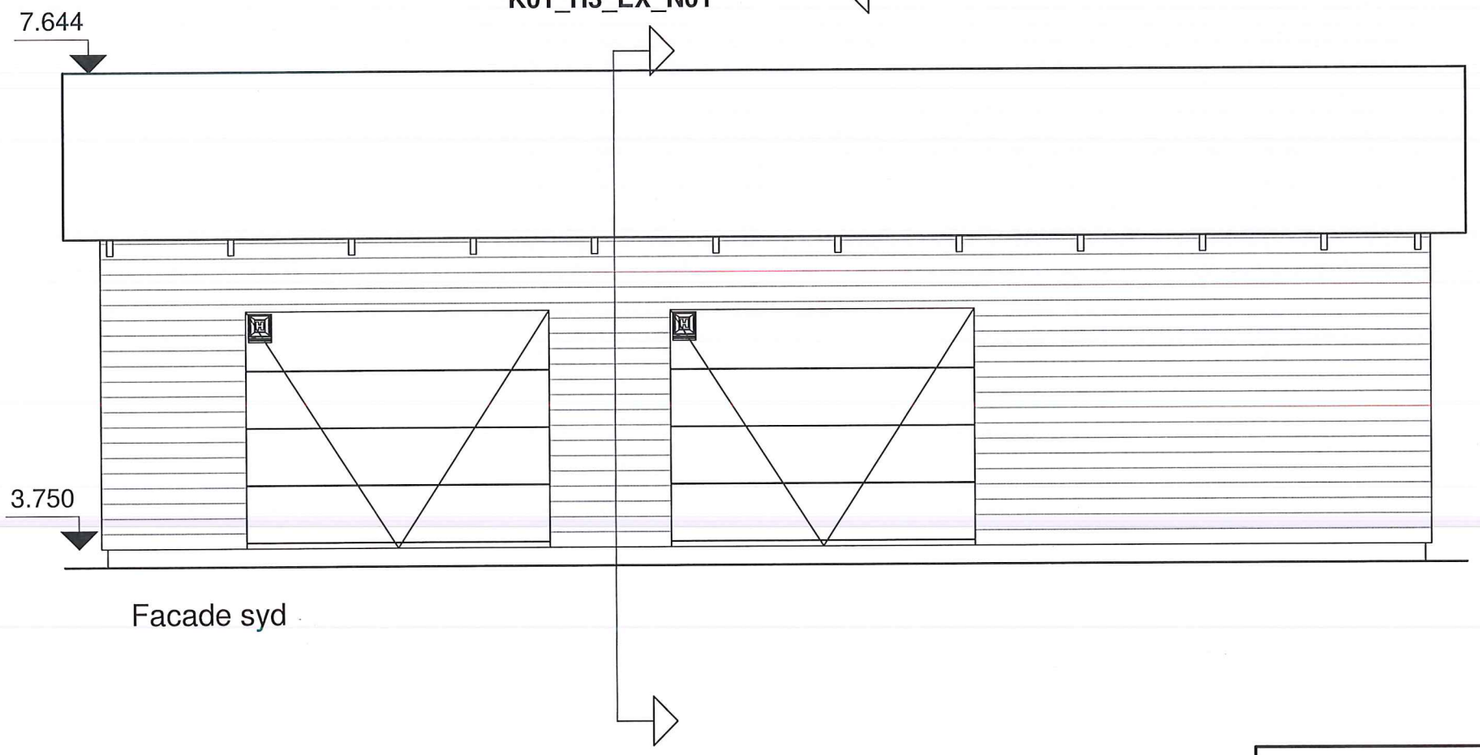


Facade syd

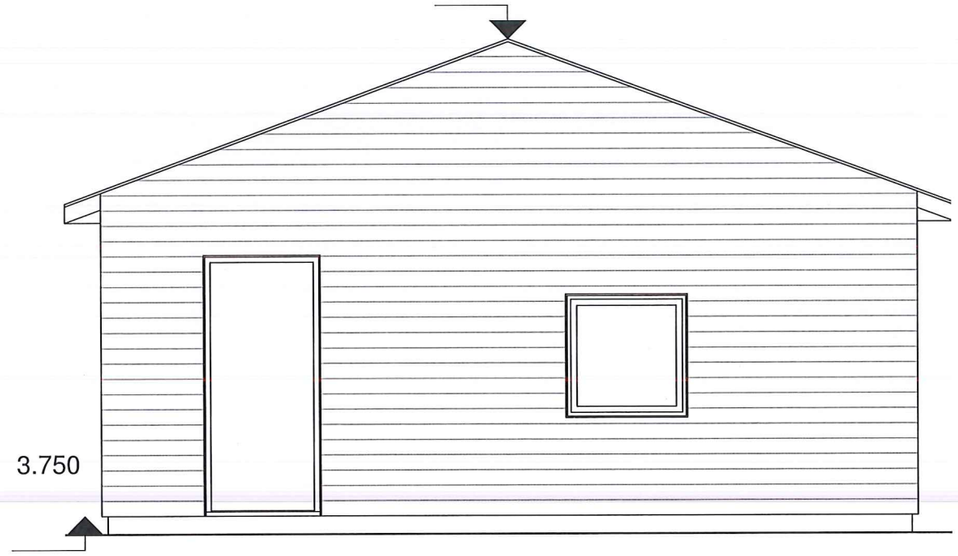

Facade øst


Færch & Co.
BYGGER PÅ TRADITIONER

BYGGESAG: Nørholmsvej 270, Garage	DATO:07.10.2021	**K01_H2_EX_N01**
EMNE: Facader	MÅL: 1 : 50	
UDFØRT AF: JTM	REV:	

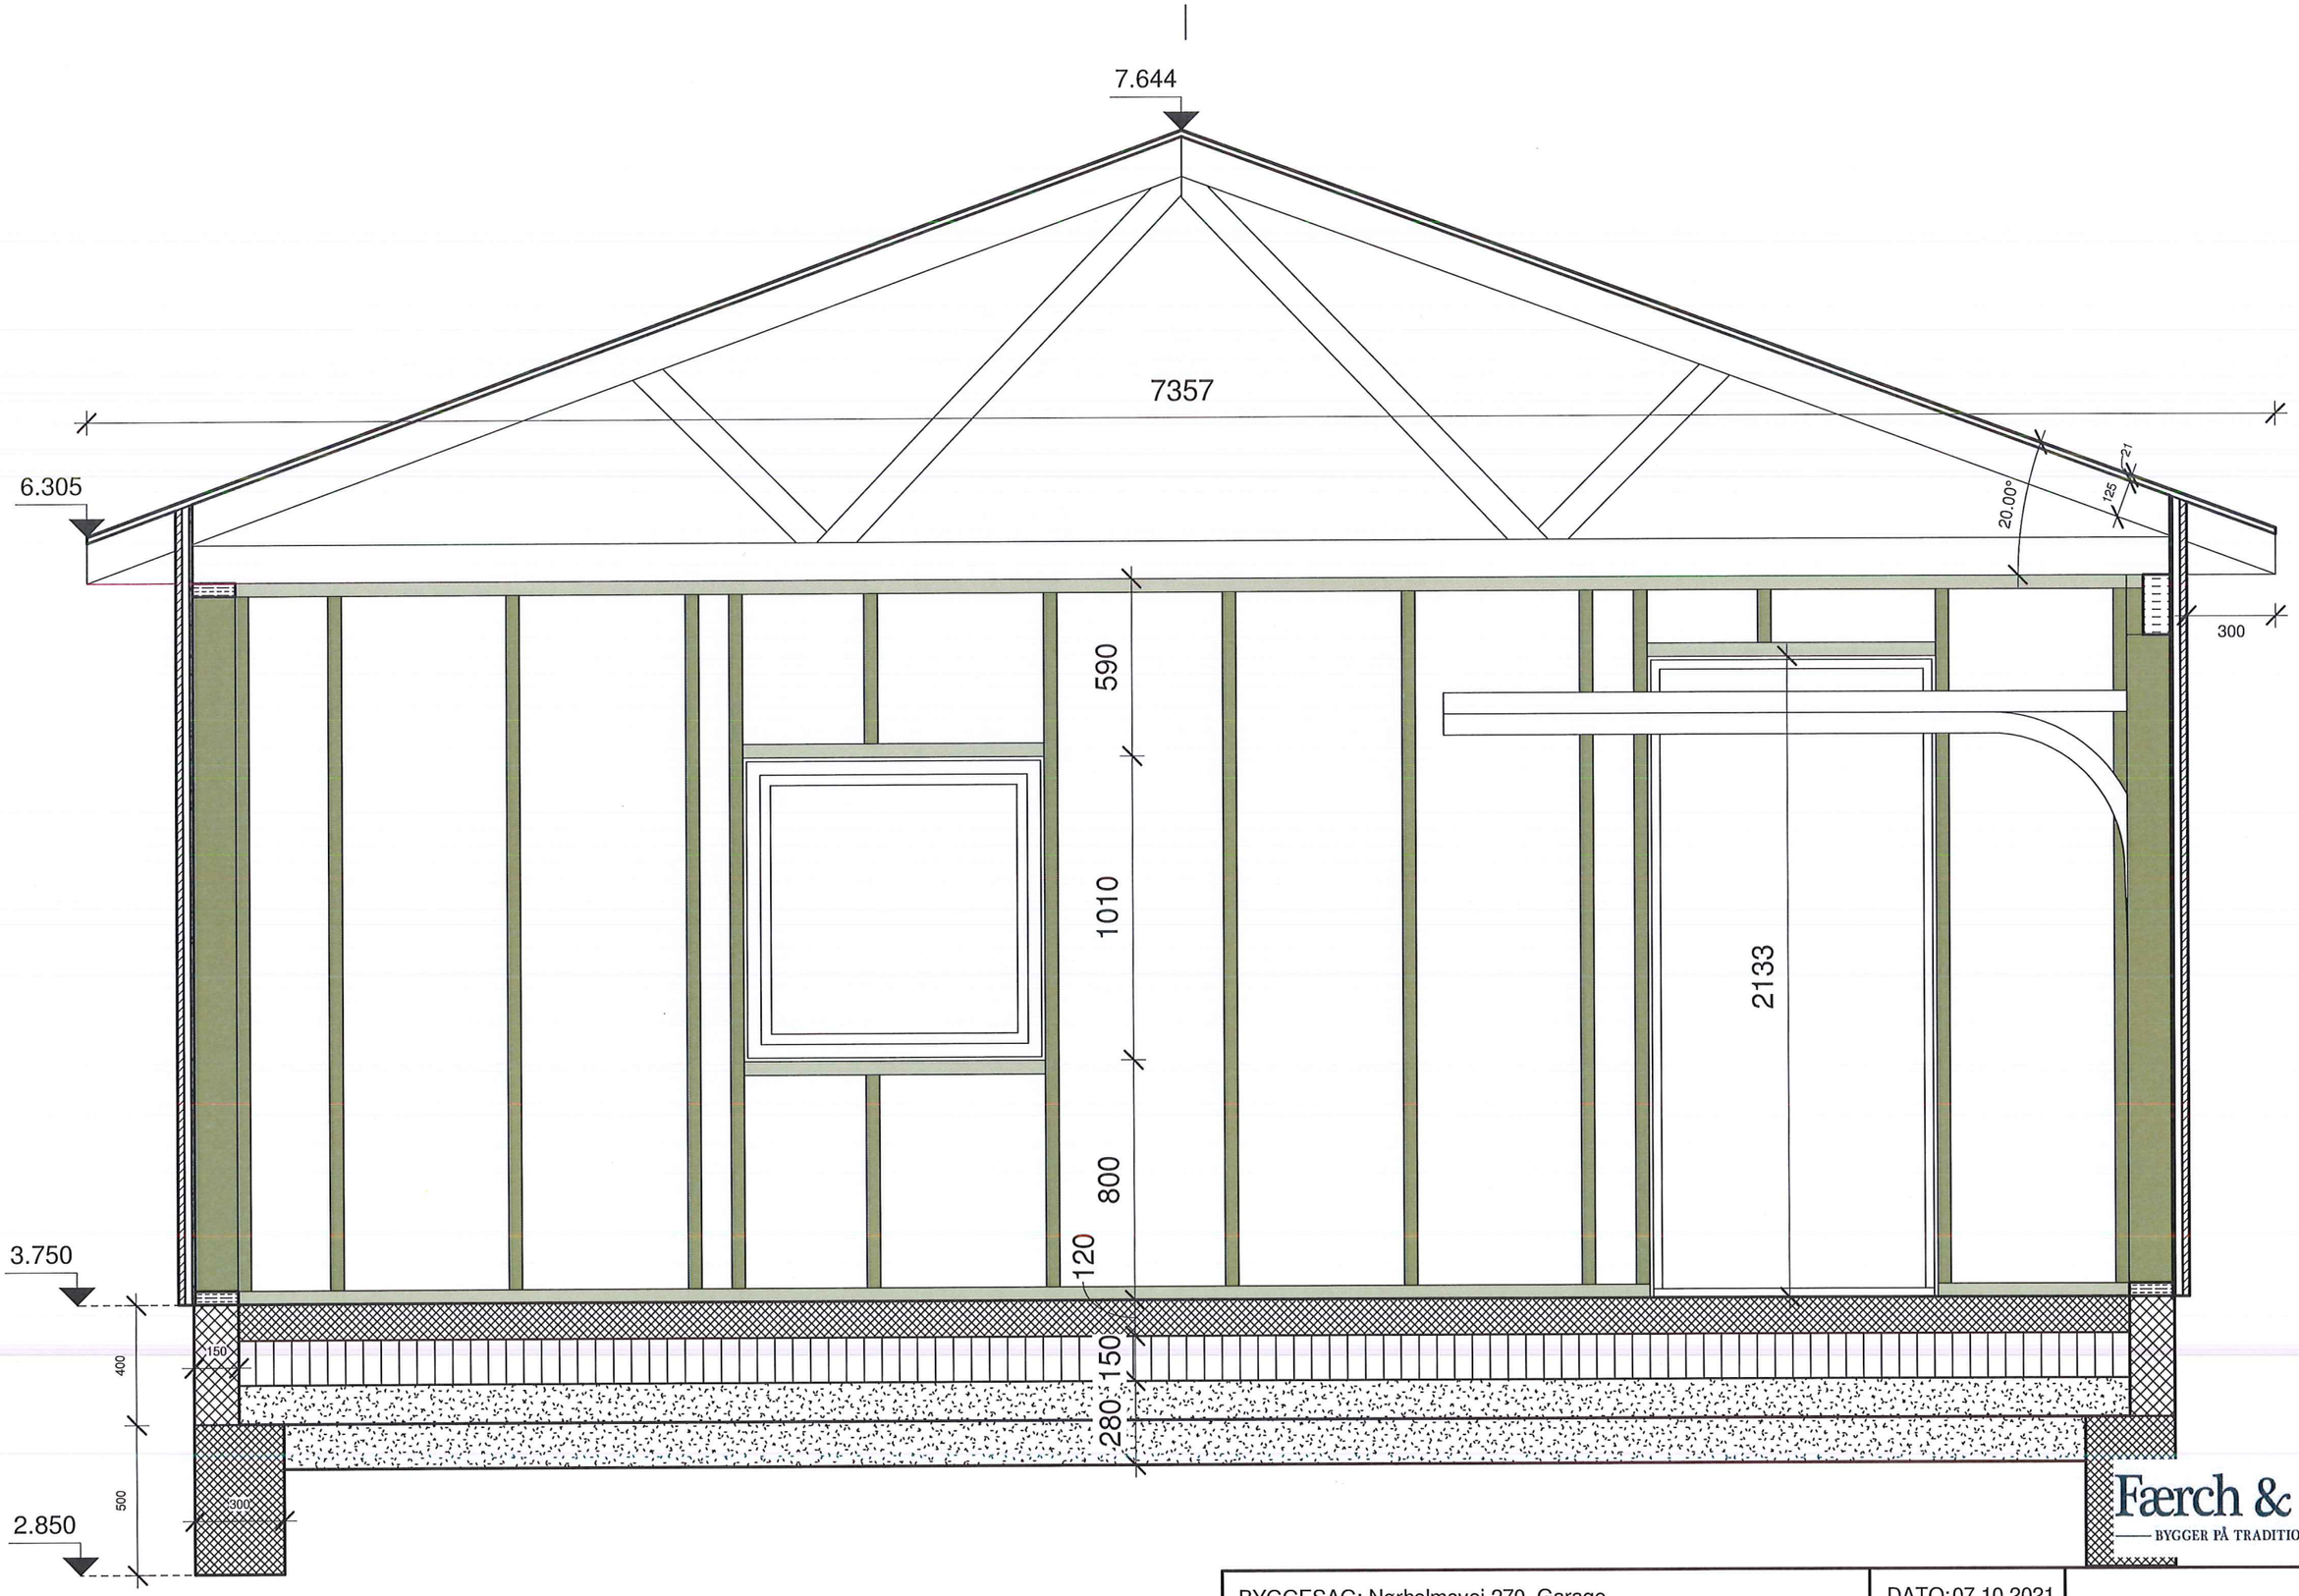

Færch & Co.
BYGGER PÅ TRADITIONER


BYGGESAG: Nørholmsvej 270, Garage	DATO: 07.10.2021	K01_H3_EX_N01
EMNE: Snit A-A	MÅL: 1 : 20	
UDFØRT AF: JTM	REV:	

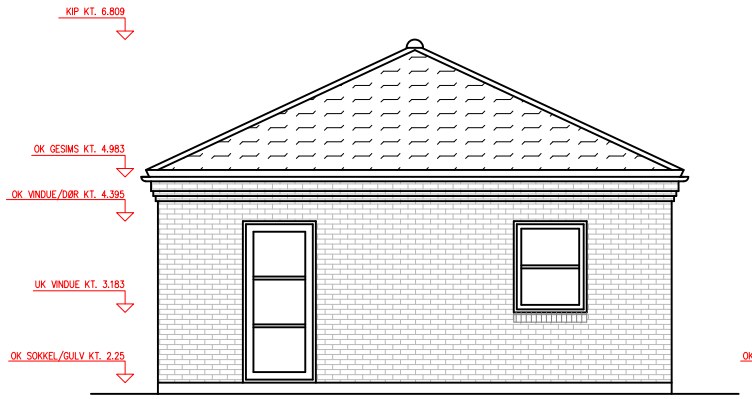


FACADE MOD NORD



FACACDE MOD ØST

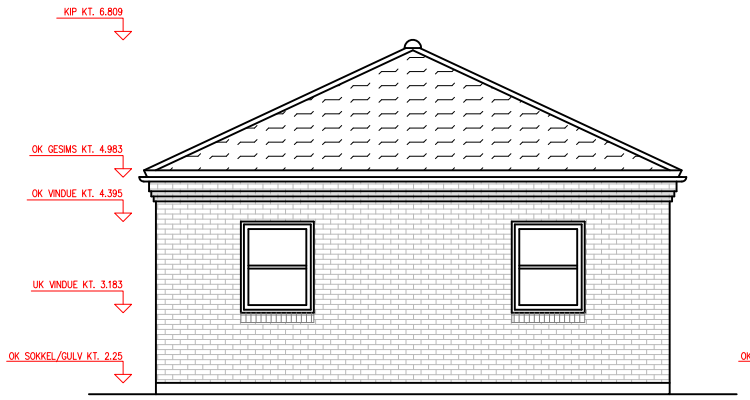

FACADE MOD SYD

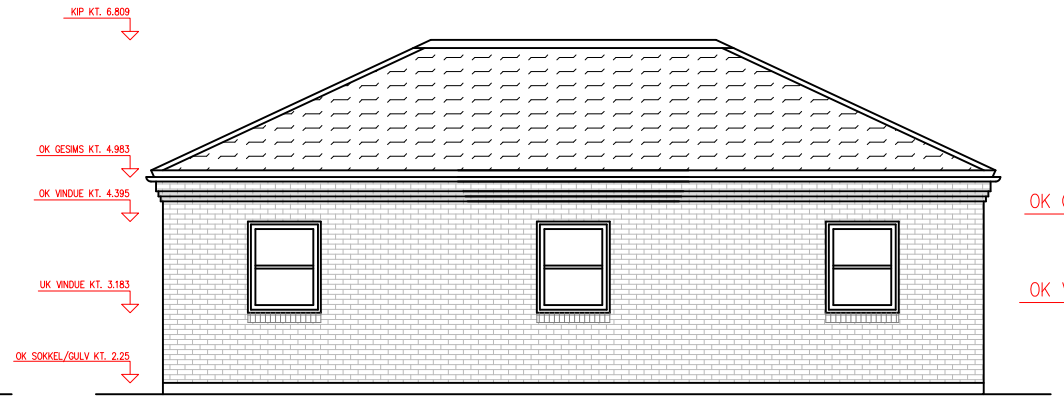

FACADE MOD VEST

TAGKONSTRUKTION:
SORTE TAGSTEN
38x73 MM. T-1 TAGLÆGTER.
25x50 MM. TRYGIMP. AFSTANDSLISTER
HUNTONIT UNDERTAG, OPLAGT IHT. LEV. ANVISNINGER.
25° GITTERSPÆR PR. 1000 MM. DIM AF LEVERANDØR.
SPÆR FASTGØRES TIL MURREM MED 90x90 MM. BMF VINKLER
MURREM 45x95 MM. TØMMER
SPÆR FORANKRES TIL SOKKEL PR. 3 M.
VINDKRYDS PÅ SPÆRHOVED UDFØRES MED 2X40 MM. BMF BÅND
ZINK TAGRENDER OG NEDLØB.
VENTILATION AF TAGRUM UDFØRES IHT. TEGL 36
VEJLEDNING VEDRØRENDE OPLÆGNING AF TEGLTAGE


LOFTER:
120 MM. MINERALULD KL. 37
DAMPSPÆRRESYSTEM SOM DAFA
22x95 MM FORSKALLINGSBRÆDDER PR. 300 MM
25 MM TROLDTEX LOFT

YDERVÆGGE:
UDV. 108 MM. MASSIV FACADESTEN TIL VANDSKURING
UDFØRES MED KVARTSTENSFORBANDT
MIN. 8 STK. BINDERE PR. M2.
NEDERSTE SKIFTE UDFØRES MED VENTILATION I HVER TREDIE STUDSFUGE.
125 MM. MURBATTS KL.37
100 MM LETBETON ELEMENTVÆG
SØJLER I VÆG HE100-B OG HE140-B VARMGALVANISERET


DØRE OG VINDUER:
DVC. GODKENDT TRÆ/ALU.
ISOLERET LEDHEJSEPORTE

GULVKONSTRUKTION:
120 MM. BETON 20 MN/M². M. GULVVARME
OG ARMERINGSNET 150x150x6
150 MM. POLYSTYREN S-150
AFRETTET SAND

FUNDAMENTER:
MURPAP.
2 RÆKKER 330 MM LECABLOKKE
STRIBEFUNDAMENTER STØBT I JORDRENDER
FØRT TIL BÆREDYGTIG DYBDE BETON 20 MN/M2.
2 STK. Y12 I TOP OG BUND
20 MM. RANDISOLERING+RADONSIKRING
NÅR DER ER FORETAGET GEOTEKNISKE UNDERSØGELSER
UDFØRES FUNDAMENTER IHT. BÆREEVNEN.

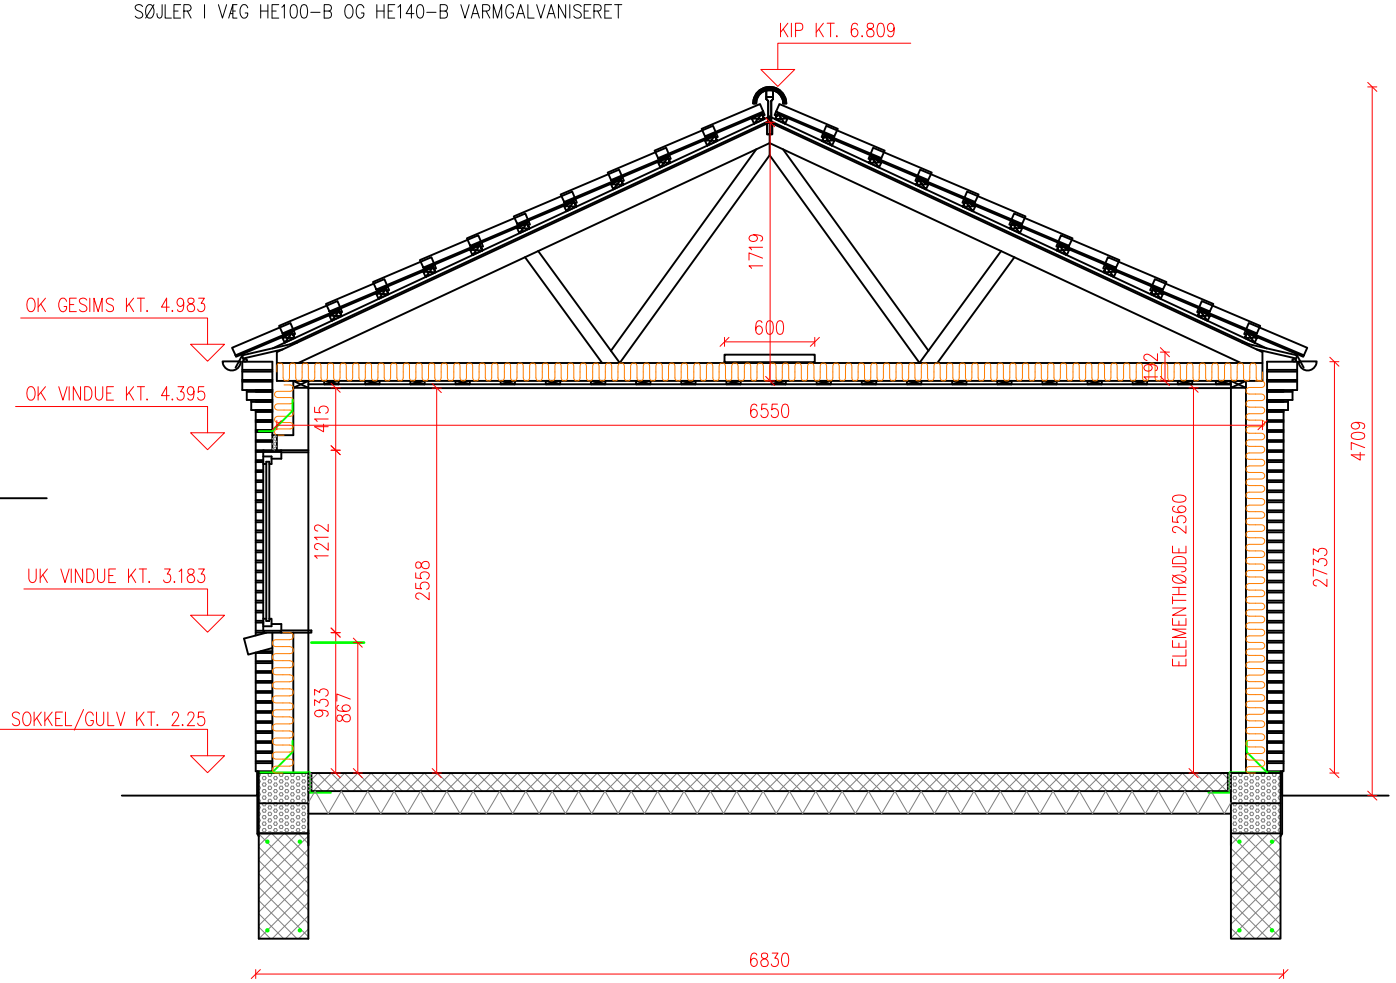

TVÆRSNIT 1:50

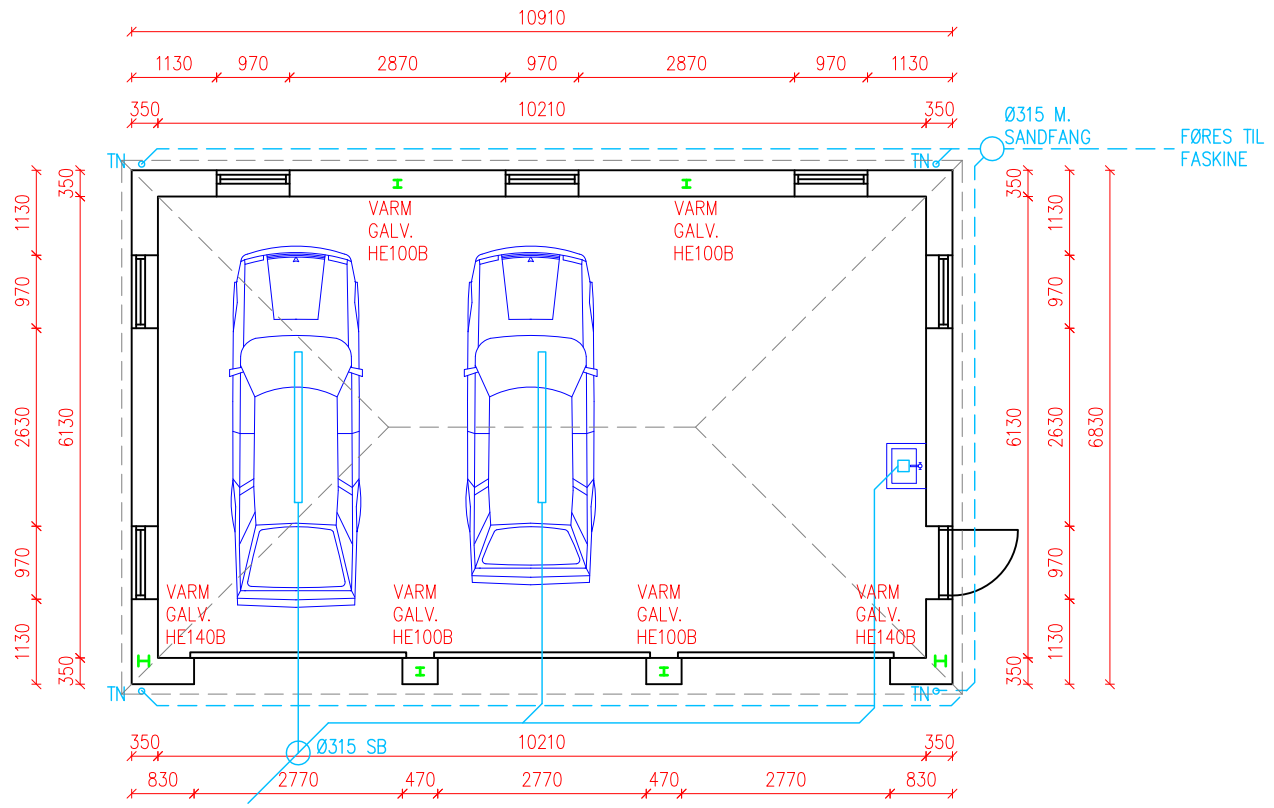

GRUNDPLAN 75 M2

SIGNATUR
TN = TAGNEDLØB
– – = REGNVANDSLEDNING
——— = SPILDEVANDSLEDNING

NOTE:
DER TAGES FORBEHOLD FOR: JORDBUNDSFORHOLD
IKKE OPLYSTE DEKLARATIONER
-OG SERVITUTTER

VVS – KLOAK OG EL SKAL UDFØRES AF AUTORISEREDE.
ALLE BÆRENDE STÅLKONSTRUKTIONER
-SKAL UDFØRES AF CERTIFICERET SVEJSER.

dato: 14.08.2013	sign.: KL	SAG NR.: 13029LAMP	tegn.nr. PL04_D
rev.: 03.07.2013	konf.:		
emne: GARAGETEGNING			mål: 1=100
kunde: MARTIN LAMPE HANSEN LUNDEN 11, 8940 RANDERS			Tlf. _ _
byggeplads: NØRHOLMSVEJ 212 9000 AALBORG			Tlf. _ _

BYGGETEKNISK RÅDGIVNING & PROJEKTERING
V/ Morten Madsen, Liljevej 25, 9800 Hjørring
Tlf. 96230131
Fax. 96230132
Mail: mail@cad-tegnestuen.dk