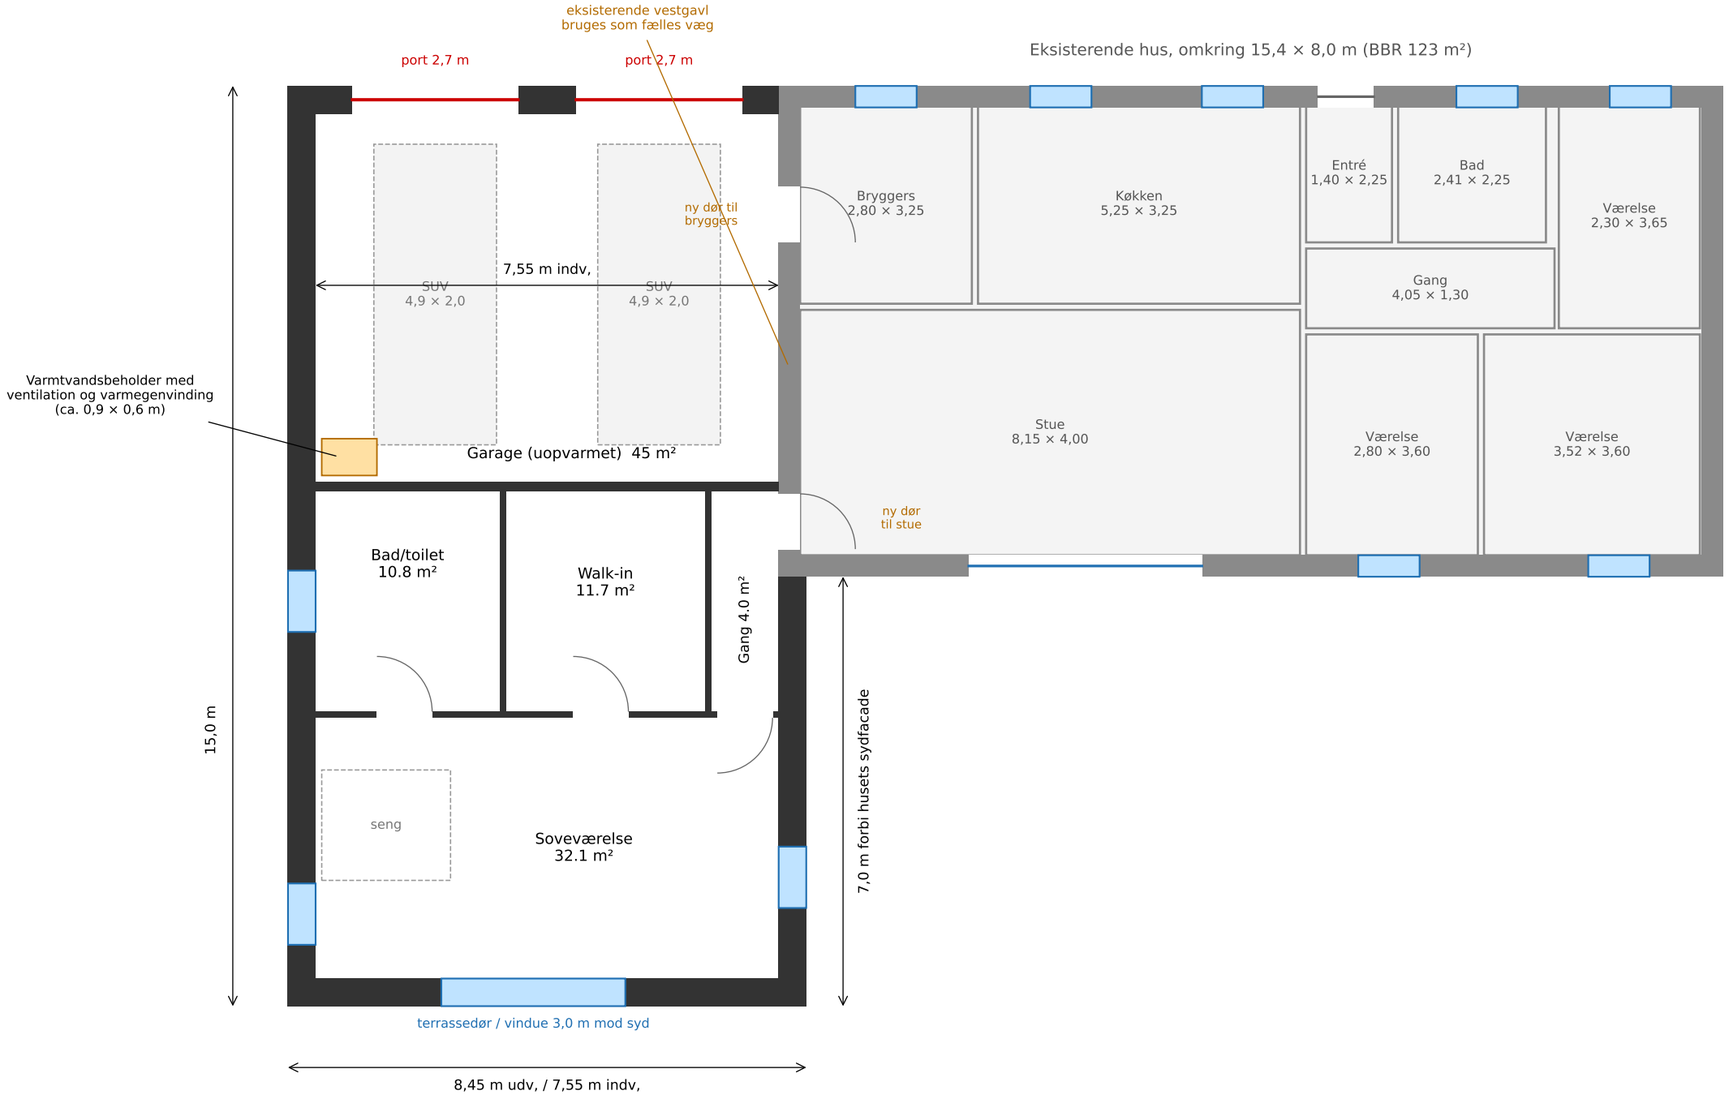

Tilbygning og eksisterende hus, plan, Nældevej 42, 9000 Aalborg

Målestok 1:100 (A3) · Tilbygning 15,0 m lang, 7,55 m bred indvendigt, 123 m² brutto, heraf omkring 71 m² opvarmet bolig

FORELØBIG SKITSE. Det eksisterende hus er tegnet efter ejendomsmæglerens vejledende plantegning fra 2024 (ikke målfast) og skal måles op. Vægtykkelser i tilbygningen er antaget:

ydervæg 45 cm, væg garage/bolig 15 cm, indervægge 10 cm. Brandadskillelse mellem garage og bolig (herunder døren til bryggerset) er ikke dimensioneret. Bryggersets vindue i vestgavlen forsvinder. Langs huset bruges husets eksisterende vestgavl som fælles væg.

BYGGESAG: Nældevej 42, 9000 Aalborg		**A2.1**
EMNE: Hus med tilbygning, plan	DATO: 10.10.2026	FORELØBIG
UDFØRT AF: JB	MÅL: 1 : 100 (A3)	