Ansøgning om landzonetilladelse: ny hal og tilbygning til stuehus

Nældevej 42, 9000 Aalborg. Matr.nr. 1cc, 1rp og 57b Restrup Hgd., Sønderholm. BFE-nr. 1416157 m.fl.

Til Aalborg Kommune, By og Land, Byggeri, att. Kirstine Reese. [dato].

Ansøgere og ejere: [navne], Nældevej 42, 9000 Aalborg. Telefon [nr.], e-mail [adresse].

1. Hvad ansøgningen omfatter

Ansøgningen følger op på mødet den [dato] og jeres efterfølgende mail med gennemgang af praksis. Den har to dele, som vi beder kommunen behandle samlet, fordi de tilsammen viser, hvordan ejendommens bebyggelse kommer til at se ud:

Del A: Ny hal	Hal på 200 m² til maskiner og udstyr til ejendommens drift og hestehold og til privat opbevaring. Vi søger landzonetilladelse efter planlovens § 35, stk. 1. Hallen opføres først
Del B: Tilbygning	Tilbygning på 123 m² til stuehuset, så boligen bliver ca. 246 m². Vi mener ikke, at den kræver landzonetilladelse, jf. planlovens § 36, stk. 1, nr. 10, og beder kommunen bekræfte det. Tilbygningen opføres senere

Byggetilladelse til begge dele søges særskilt, når landzoneforholdene er afklaret.

2. Ejendommen

Areal	39.130 m² (ca. 3,9 ha): matr.nr. 1cc (19.977 m²), 1rp (5.516 m²) og 57b (13.637 m²). Stuehus, stald og skur ligger på 1cc, ridebanen på 1rp
Zone og notering	Landzone. [Noteret som landbrugsejendom / ikke landbrugsnoteret: bekræftes]
Anvendelse	Bolig med privat hestehold: [antal] heste, stald med 4 hestebokse, 2 ponybokse og løsdrift, ridebane på ca. 20 × 39 m og folde
BBR-bygning 4	Stuehus, 123 m², opført 1992, ombygget 2024. Én boligenhed
BBR-bygning 2	Bygning til træning og opstaldning af heste, 284 m². Indretning og brug fremgår af bilag A3.1
Øvrige bygninger	Skur på ca. 23 m² op ad staldens østside, opført efter byggesag S2021-530504 (2020-1967). Der er ingen garage, carport eller maskinhus på ejendommen
Forsyning	Privat vandforsyning, jordvarme, privat fællesvej. Spildevand: mekanisk rensning med udledning

3. Planforhold og udpegninger

Vi har slået begge placeringer op i Plandata og Danmarks Arealinformation den 10. oktober 2026. Hvor intet andet er nævnt, gælder oplysningen både hal og tilbygning:

Plangrundlag	Landzone. Ingen lokalplan og ingen kommuneplanramme
Kommuneplanens retningslinjer	Større sammenhængende landskab. Grønt Danmarkskort: potentielt naturområde og potentiel økologisk forbindelse (Tostrup og Hasseris Ådal samt Restrup og Sønderholm Skove). Hallens placering ligger desuden i et område, der kan blive udsat for oversvømmelse; det gør tilbygningens ikke
Landskabskarakter	Nørholm Fjordlandskab, som for naboejendommen Nældevej 30 (kommunens afgørelse S2023-8926 af 18. januar 2024)
Ikke udpeget som	Bevaringsværdigt landskab, lavbundsareal, værdifuldt kulturmiljø, værdifuldt landbrugsområde, skovrejsningsområde eller geologisk bevaringsværdi
Kystnærhedszonen	Ejendommen ligger i kystnærhedszonen, uden for udviklingsområde. Afstanden til Limfjorden er ca. 1,9 km
Skovbyggelinje	Begge placeringer ligger inden for skovbyggelinjen fra skoven mod øst, ligesom ejendommens eksisterende bygninger. Hallen ligger ca. 35 m fra skovbrynet, tilbygningen ca. 80 m. Forbuddet i naturbeskyttelseslovens § 17 gælder ikke for byggeri, der har fået landzonetilladelse, jf. § 17, stk. 2, nr. 5
Øvrige linjer	Uden for sø- og åbeskyttelseslinje, kirkebyggelinje og fredninger. Ingen beskyttede sten- og jorddiger på stedet
Beskyttet natur (§ 3)	Nærmeste er en sø ca. 170 m fra hallen og ca. 210 m fra tilbygningen. Nærmeste beskyttede vandløb ca. 300 m
Natura 2000	Nærmeste område er nr. 15, Nibe Bredning, Halkær Ådal og Sønderup Ådal (habitat-, fuglebeskyttelses- og Ramsarområde), ca. 1,8 km mod nord
Bilag IV-arter	Kommunen har i sine afgørelser for Nældevej 9 (S2024-1080) og Nældevej 37 (S2025-2936) oplyst kendskab til spidssnudet frø, odder, strandtudse, stor vandsalamander og flagermus inden for 2 km. Se afsnit A2

Del A: Ny hal på 200 m²

A1. Det ansøgte

Bygning	Hal 20,0 × 10,0 m = 200 m², én etage, sadeltag 30° med kip nord-syd. Sidehøjde 4,0 m over soklen, kiphøjde 7,3 m over terræn
Materialer	Stålrammer på gennemgående betonsokkel med overkant ca. 0,4 m over terræn, i samme højde som stuehusets sokkel. Facader og tag i sorte, matte sandwichpaneler, som de sorte tage på stuehus og stald
Åbninger	Port 4,0 × 4,0 m og en gangdør i nordgavlen, som vender mod ejendommens egne bygninger og ridebanen. Ingen åbninger i de øvrige facader
Placering	I folden umiddelbart øst for haven, 11,3 m fra stuehuset og 11,4 m fra skuret ved stalden, parallelt med stald og stuehus. Se bilag A0.1 og A0.2
Ejendommens drift og hestehold, ca. 150 m²	Traktor med frontlæsser, ladtrailer med kapel til hø, halm og wrap, hestetrailer, balleflytter til wrapballer, halmballe-elevator, møgtrailer, to plænetraktorer og slæbeharve til ridebanen, samt et rum på 20 m² til foder, hesteudstyr og værktøj til maskinerne. Maskinerne bruges til foder og strøelse (ca. 25 rundballer om året), udmugning, kørsel til møddingen og pasning af folde, ridebane og ejendommens 3,9 ha
Privat opbevaring, ca. 50 m²	Samlet i hallens sydvestlige hjørne: et rum på 20 m², plads til en trailer og en tosøjlet lift til hjulskift og vedligehold af husstandens egne biler
Toilet	Et toilet med håndvask på 1,5 × 1,8 m i rummet til foder og værktøj, til brug for dem, der arbejder i hallen, i stalden og på ridebanen. Hverken bad eller køkken
Opvarmning og afløb	Uopvarmet hal. Toilettet tilsluttes ejendommens spildevandsanlæg [afklares]; vi søger særskilt om tilslutningen
Tagvand	Tagvand fra hallen (ca. 210 m² tagflade) ledes i lukket rør via en forsinkelsesbrønd til ridebanens eksisterende omfangsdræn og pumpebrønd (ca. 200 l/min). Vi søger særskilt om tilladelse, hvis tilslutningen kræver det
Forplads	Foran port og dør lægges fliser 50 × 50 cm, som ejendommens øvrige belægning, som en rampe fra gulvhøjde ved gavlen skrået ned til kørevejen, ca. 4 m lang, med fald ud til siderne
Matrikler og skel	Hallen ligger hen over skellet mellem ansøgernes egne matr.nr. 1cc og 1rp, ca. 7 m af bredden på 1cc og ca. 3 m på 1rp. Der er ca. 38 m til nærmeste skel mod nabo. Skellene er vist på bilag A0.1
Adgang	Ad ejendommens eksisterende kørevej fra Nældevej øst om stalden. Der etableres ikke ny overkørsel

Plantegningen (bilag A1.1) viser, hvad hver maskine og hver funktion fylder. De eksisterende bygninger kan ikke rumme maskinerne: stalden er i brug til hestene rum for rum, som vist på bilag A3.1, løsdriften bruges med dybstrøelse, skuret er fyldt med åbnede wrapballer, og ingen af bygningerne har en port, en traktor kan køre ind ad. Maskiner og trailere står i dag udendørs.

Hesteholdet er privat. Vi er bekendt med, at et privat hestehold ikke er erhvervsmæssig landbrugsdrift efter planloven, og søger derfor landzonetilladelse efter § 35, stk. 1, til hele hallen. Der drives ikke erhverv fra hallen, og der indrettes ikke bolig.

A2. Begrundelse

Behovet

- Ejendommen er på 3,9 ha med stald, ridebane og folde. Pasningen af hestene og arealerne kræver traktor, trailere til hø, halm og heste, balleflytter, møgtrailer, plænetraktorer og ridebaneharve, som i dag står udendørs. Hver maskine har en fast opgave, og plantegningen viser, at hallen ikke rummer mere end det.

- Kommunen har i to afgørelser i vores område fundet, at et privat hestehold begrunder en bygning til maskinerne. I sag S2022-171976 (Nibevej 384, 13. februar 2023) fik en landbrugsejendom på 1,87 ha med tre heste tilladelse til en lade på 98 m² til traktor, brakpudser, halm, hø, træningsvogne, seletøj og strøelse; ejendommen brugte ca. 25 rundballer hø om året, som vi. Kommunen lagde vægt på, at et mindre hestehold er hjemmehørende i landzonen, og at laden var passende til ejendommens størrelse. I sag S2025-326 (Nørholmsvej 149, 16. juni 2025, ca. 900 m herfra) fik en landbrugsejendom på 2,5 ha med privat hobbyhestehold i 4 hestebokse tilladelse til et udhus på 148 m², hvoraf 104 m² til traktor, ATV, slagleklipper, ballespyd, harve og tromle til vedligehold af ejendommen og 44 m² til privat værksted. Kommunen fandt bygningen passende for en ejendom på over 2,5 ha, hvor de øvrige udhuse var små, og lagde igen vægt på, at heste er hjemmehørende i landzonen.
- Vores ejendom er halvanden gang så stor som Nørholmsvej 149 og dobbelt så stor som Nibevej 384, har flere heste og flere maskiner, og vores eneste udhus er et skur på 23 m².

Størrelsen i forhold til kommunens praksis

- Vi er bekendt med kommunens praksis, som den er gengivet i afgørelserne S2024-1080 og S2025-10959: der gives normalt landzonetilladelse til nye udhuse og garager på 50-100 m², og ved den konkrete vurdering indgår ejendommens størrelse, omfanget af eksisterende udhuse og placeringen. På alle tre punkter står vi stærkt: ejendommen er på 3,9 ha, det eneste udhus er et skur på 23 m², og hallen ligger 11 m fra stuehuset inde i den samlede bebyggelse.
- Kommunen har godkendt samme størrelse og samme opdeling som vores i sag S2025-10959 (Duedal 93, 21. maj 2026): en uopvarmet hal på 150,7 m² til traktor, rendegraver, minilæsser, havetraktor og andre maskiner til vedligehold af en landbrugsejendom på 1,65 ha uden erhvervsmæssig landbrugsdrift, og samtidig en garage på 50 m² ved siden af. Kommunen lagde afgørende vægt på, at der ikke var anden udhusbebyggelse på ejendommen, at behovet var dokumenteret, og at bygningen havde en passende størrelse i forhold til ejendommens størrelse og behov for større maskiner til vedligehold af arealet. Vores hal er delt på samme måde: ca. 150 m² til pasning af ejendommen og hesteholdet og ca. 50 m² privat, svarende til den garage på op til 50 m², der kan opføres ved et enfamiliehus i landzone uden tilladelse efter § 36, stk. 1, nr. 8. Vores ejendom er mere end dobbelt så stor, og vi har heste, som Duedal 93 ikke havde.
- Vi samler det hele under ét tag i stedet for at bygge to bygninger. I sag S2023-4703 (Nørholmsvej 222, 20. april 2023) godkendte kommunen en samlet bygning på 198 m² på en ejendom på 6,3 ha, 120 m² maskinhus og 78 m² udhus, og lagde afgørende vægt på, at sammenbygningen undgår spredt bebyggelse og påvirker landskabet mindre. Det gælder også her.
- Det private er samlet i hallens sydvestlige hjørne og er vist som blå felter på bilag A1.1, så opdelingen kan kontrolleres.

Toilettet

- Arbejdet i hallen, i stalden og på ridebanen er snavset: heste, gødning, foder, olie og maskiner. Et toilet med håndvask i hallen betyder, at man kan vaske hænder og gå på toilettet i arbejdstøj og støvler uden at gå gennem boligen. Kommunen har godkendt toilet i et udhus med opbevaring, værksted og garage i sag S2024-7549 (Restrup Kærvej 16, 21. november 2024).
- Toilettet er ikke begyndelsen på en bolig. Der indrettes hverken bad, køkken eller opholdsrum, rummene er uden vinduer og uopvarmede, og vi accepterer vilkår om, at hallen ikke må bruges til beboelse eller overnatning.

Placering og landskab

- Hallen ligger i direkte tilknytning til ejendommens samlede bebyggelse, 11 m fra stuehus og skur, og nås ad den eksisterende kørevej. Det er inden for de ca. 20 m, kommunen efter sin praksis regner som tilknytning (S2025-6024, Munkbækvej 16, 1. oktober 2025), og bygninger og færdselsarealer udgør fortsat én enhed. I sag S2024-19470 (Nældevej 55, 7. november 2024) lagde kommunen afgørende vægt på, at en carport til traktor, havetraktor og wrapballer til hesteholdet lå ved ejendommens tilkørselsarealer højst 22 m fra boligen.
- I Nørholm Fjordlandskab bør ny bebyggelse efter kommuneplanens retningslinje knyttes til de eksisterende bebyggelser langs vejene og understøtte strukturen af mindre gårde og husmandssteder, og det åbne, flade kystlandskab bør bevares. Hallen lægges inde i en eksisterende gårdbebyggelse ved Nældevej, mellem stuehus, stald og skov, og ikke ud i det åbne land. Naboejendommen Nældevej 30 har samme udpegninger, og kommunen fandt dér (S2023-8926), at et udhus i tilknytning til bebyggelsen ikke havde væsentlig betydning for dem.

- Set fra Nældevej og fra fjorden mod nord ligger hallen bag stald, ridebane og læbælte. Mod vest skærmer læbæltet langs skellet og mod øst skoven. Hallen slører derfor ikke landskabssammenhængene i det større sammenhængende landskab. De rumlige skitser i bilag B1 viser det fra fire sider.

- Kiphøjden på 7,3 m over terræn er under bygningsreglementets 8,5 m. Hallen i sag S2025-10959 er 6,7 m til kip; forskellen hos os er soklen på 0,4 m, som følger stuehusets og hensynet til oversvømmelsesudpegningen, og en sidehøjde på 4,0 m, som porten på 4,0 m og traktoren med frontlæsser kræver. Facader og tag er sorte og matte, uden reflekser. Vi planter et læbælte af hjemmehørende arter syd for hallen, hvor den står frit, og holder det i mindst 3 m højde.

Kystnærhedszonen

- Hallen opføres inde i en bestående bebyggelse ca. 1,9 km fra kysten, bag eksisterende bygninger og beplantning set fra fjorden, og den ændrer ikke kystlandskabet. Vi mener derfor, at den har helt underordnet betydning for de nationale planlægningsinteresser i kystområderne, jf. planlovens § 35, stk. 3. Kommunen har givet landzonetilladelse til udhuse, garager og carporte i samme del af kystnærhedszonen på Nældevej 30 (S2023-8926), Nældevej 55 (S2024-19470) og Nældevej 9 (S2024-1080) samt på Nørholmsvej 149 (S2025-326).

Natur

- Hallen opføres på en afgræsset fold tæt ved bygninger, kørearealer og ridebane. Der fældes ingen træer og fjernes ingen hegn eller diger. Med 1,8 km til nærmeste Natura 2000-område og hallens begrænsede omfang kan den hverken alene eller sammen med andre planer og projekter påvirke området.

- Bilag IV-arter: Byggefeltet er en tæt afgræsset hestefold uden vandhuller, grøfter, gamle træer eller bygninger, og der er daglig færdsel af mennesker og heste. Det er ikke egnet som yngle- eller rasteområde for padder, odder eller flagermus. Nærmeste sø ligger ca. 170 m væk, med ejendommens bygninger imellem. Der fældes ingen træer og nedrives ingen bygninger, så flagermus mister ikke levesteder, og en bygning på 200 m² inde i bebyggelsen spærrer ikke for dyrs vandring. Kommunen nåede samme resultat for ridebanen på Nældevej 37 (S2025-2936), som ligger 300 m herfra i samme landskab.

- Skovbrynet berøres ikke: der er ca. 35 m fra hallen til skoven, og hallen ligger ikke mellem skoven og det åbne land, men ind mod ejendommens bygninger. Den tager derfor ikke udsynet til skoven fra vej eller nabo. Hele ejendommens bebyggelse ligger inden for skovbyggelinjen, så hallen kan ikke placeres uden for den.

- Den potentielle økologiske forbindelse følger ådalen og skovene. Hallen optager 200 m² af en fold midt i bebyggelsen og spærrer ikke for forbindelsen.

Oversvømmelse

- Hallen er et uopvarmet maskinhus uden beboelse. Soklens overkant og hallens gulv lægges ca. 0,4 m over terræn, i samme højde som stuehusets sokkel [terrænkote indsættes], og kommunen er velkommen til at stille vilkår om sokkelhøjde. Terrænet ændres ikke uden om hallen, og tagvandet ledes til ejendommens eksisterende dræn og pumpe, så der ikke ledes vand mod naboer.

Naboer

- Hallen har ingen åbninger mod naboer. Nærmeste bygning på en naboejendom ligger ca. 50 m fra hallen mod sydøst [afstand til nabobeboelse bekræftes], og der er ca. 38 m til nærmeste skel mod nabo. Naboerne har skriftligt erklæret, at de ikke har indvendinger mod byggeriet (bilag B2).

Matrikler

- Matr.nr. 1rp ligger omgivet af 1cc og rummer ridebanen og en del af foldene. Alle tre matrikler ejes af ansøgerne og drives som én ejendom. [Afklares: om 1rp og 1cc er noteret som én samlet fast ejendom. Er de ikke det, lægger vi matriklerne sammen ved landinspektør, før hallen opføres, og accepterer det som vilkår.]

A3. Vilkår, vi kan acceptere

At hallen ikke bruges til erhverv, beboelse eller overnatning. At der ikke er udendørs oplag af maskiner, trailere og redskaber. At facader og tag holdes i mørke, ikke-reflekterende farver. At der plantes og vedligeholdes afskærmende beplantning af hjemmehørende arter syd for hallen i mindst 3 m højde, og at de eksisterende læbælter bevares. Vilkårene kan tinglyses på ejendommen.

Del B: Tilbygning til stuehuset

B1. Det ansøgte

Bygning	Tilbygning på 123 m² brutto mod vest på stuehuset, én etage. 15,0 m lang og 8,0 m bred langs huset; syd for huset 8,45 m, fordi tilbygningens østvæg står uden på husets gavl. Den går 7,0 m forbi husets sydfacade
Indhold	Garage til to biler (45 m²), bad (11 m²), garderobe (12 m²), gang (4 m²) og soveværelse (32 m²). Opvarmet bolig ca. 71 m². Intet køkken
Sammenbygning	Tilbygningen bruger husets vestgavl som fælles væg og får døre til stuen og til bryggerset. Den er en udvidelse af den eksisterende bolig
Udseende	Samme stil som huset: hvide vægge, sort bølgepladetag med samme taghældning og kiphøjde (ca. 4,7 m over terræn), samme grå sokkel (ca. 0,4 m) og sorte vinduer i husets mål. Se bilag A2.1-A2.3
Samlet bolig	123 m² + 123 m² = ca. 246 m² bruttoetageareal, inklusive den integrerede garage
Placering	På matr.nr. 1cc, ca. 4,9 m fra skellet mod vest (matr.nr. 1cb). Garageportene vender mod gårdspladsen; garagens gulv ligger i sokkelhøjde, og gruset føres jævnt op til portene
Afløb	Det nye bad tilsluttes ejendommens spildevandsanlæg [afklares]
Tidsplan	Hallen opføres først. Tilbygningen opføres derefter, senest [år]

B2. Hvorfor tilbygningen ikke kræver landzonetilladelse

Efter planlovens § 36, stk. 1, nr. 10, kræves der ikke landzonetilladelse til til- og ombygning af et helårshus, hvorved husets samlede bruttoetageareal ikke overstiger 500 m²:

- Huset er et fritliggende helårshus med én boligenhed, opført 1992.
- Det samlede areal bliver ca. 246 m², under halvdelen af grænsen på 500 m², også når garagen regnes med.
- Tilbygningen er sammenbygget med huset og deler væg og tag med det. Der indrettes ikke en ekstra bolig; tilbygningen har intet køkken.

Vi beder kommunen bekræfte, at tilbygningen er omfattet af § 36, stk. 1, nr. 10. Mener kommunen, at den kræver landzonetilladelse, beder vi om, at denne ansøgning også behandles som ansøgning om det.

B3. Forholdet til omgivelserne

- Tilbygningen ligger op ad huset inde i ejendommens bebyggelse, bag læbæltet mod vest, og har samme højde, form og farver som huset. Den ændrer ikke bebyggelsens fremtræden i landskabet.
- Den opføres på eksisterende græsplæne og grus. Der fældes ingen træer. Placeringen ligger ikke i det område, der kan blive udsat for oversvømmelse.
- Vi sikrer selv, at tilbygningen overholder bygningsreglementets afstands- og højdekrav, og at ejendommens jordvarmeslanger i haven mod vest respekteres eller lægges om.

B4. Rækkefølge

Vi ønsker at bygge hallen først og tilbygningen senere. Vi beder kommunen oplyse, om tilbygningen kan indgå i samme byggetilladelse, eller om vi skal søge byggetilladelse til den, når vi er klar.


Bilag

A0.1	Situationsplan 1:500 med hal, tilbygning og matrikelskel
A0.2	Situationsplan på luftfoto
A1.1	Hal, plan og indretning 1:100

A1.2	Hal, facader 1:100
A1.3	Hal, snit 1:50
A2.1	Hus med tilbygning, plan 1:100
A2.2	Hus med tilbygning, facader 1:100
A2.3	Tilbygning, snit 1:50
A3.1	Stald, eksisterende indretning og brug 1:100
B1	Rumlige skitser fra fire hjørner
B2	Naboernes skriftlige erklæring [vedlægges]

Med venlig hilsen

[navne]

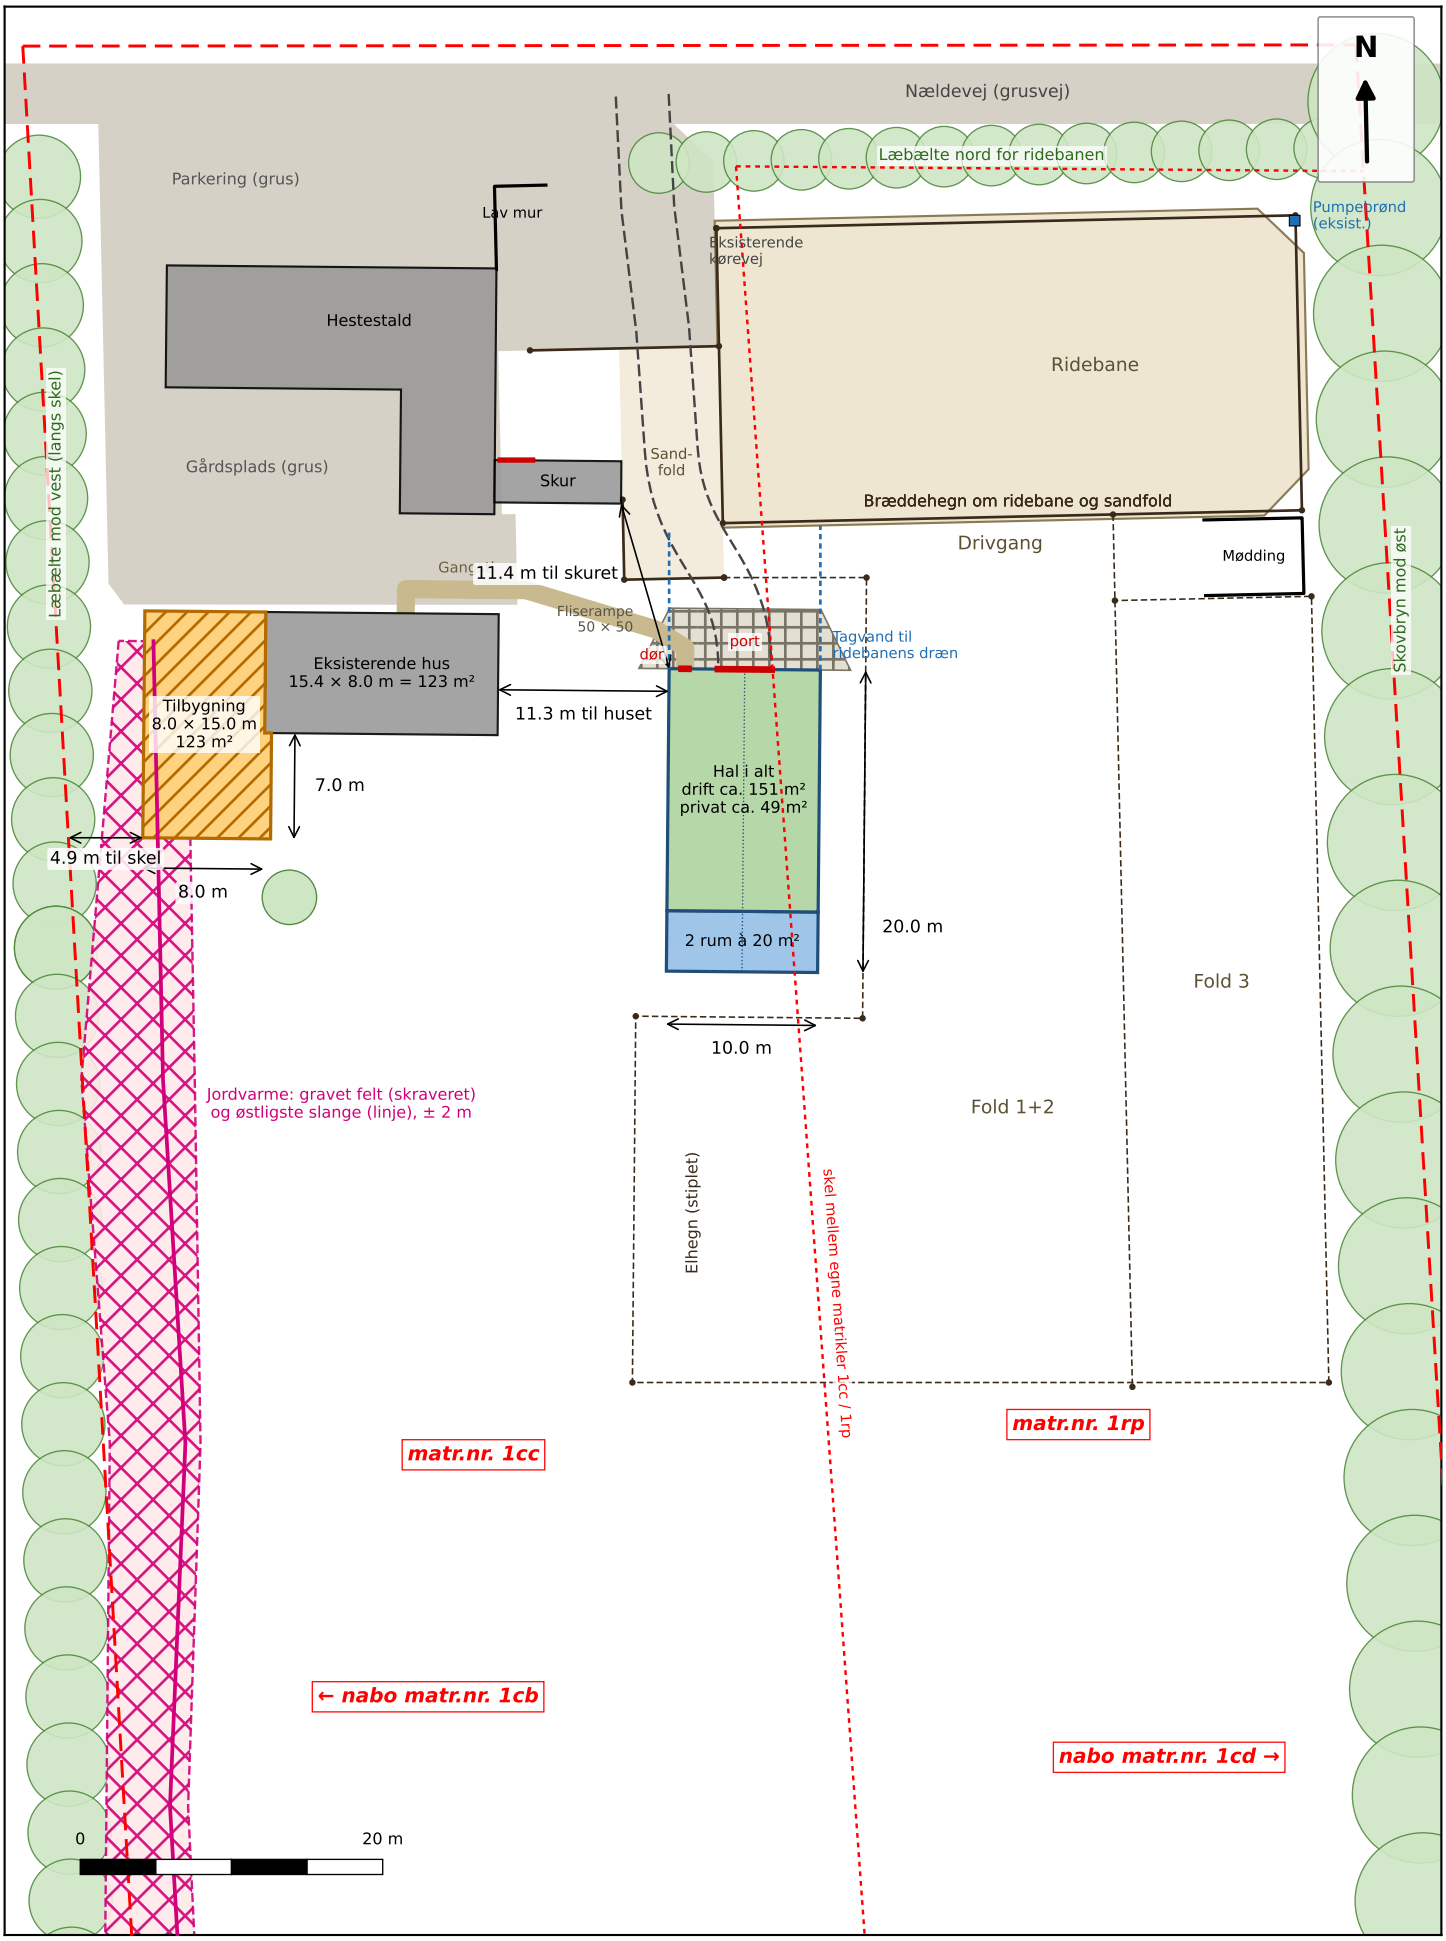

Situationsplan, Nældevej 42, 9000 Aalborg

Målestok 1:500 (A4) · Tilbygning til hus og ny hal 20 × 10 m

Matrikelskel (rødt) er tegnet efter matriklen.dk, ca. ± 1 m, og er ikke indmålt. Jordvarmezonen er anslået. Husets mål følger ejendomsmæglerens plan (2024).

Bygningsomrids og vej: © OpenStreetMap-bidragydere (GeoDanmark).

BYGGESAG: Nældevej 42, 9000 Aalborg		**A0.1**
EMNE: Situationsplan	DATO: 11.10.2026	
UDFØRT AF: JB	MÅL: 1 : 500 (A4)	LANDZONEANSØGNING




Situationsplan, Nældevej 42, 9000 Aalborg

Målestok 1:500 (A4) · Tilbygning til hus og ny hal 20 × 10 m

Matrikelskel (rødt) er tegnet efter matriklen.dk, ca. ± 1 m, og er ikke indmålt. Jordvarmezonen er anslået. Husets mål følger ejendomsmæglerens plan (2024).

Bygningsomrids og vej: © OpenStreetMap-bidragydere (GeoDanmark). Luftfoto: Apple Kort, kun arbejdskort.

BYGGESAG: Nældevej 42, 9000 Aalborg		**A0.1**
EMNE: Situationsplan	DATO: 11.10.2026	
UDFØRT AF: JB	MÅL: 1 : 500 (A4)	LANDZONEANSØGNING

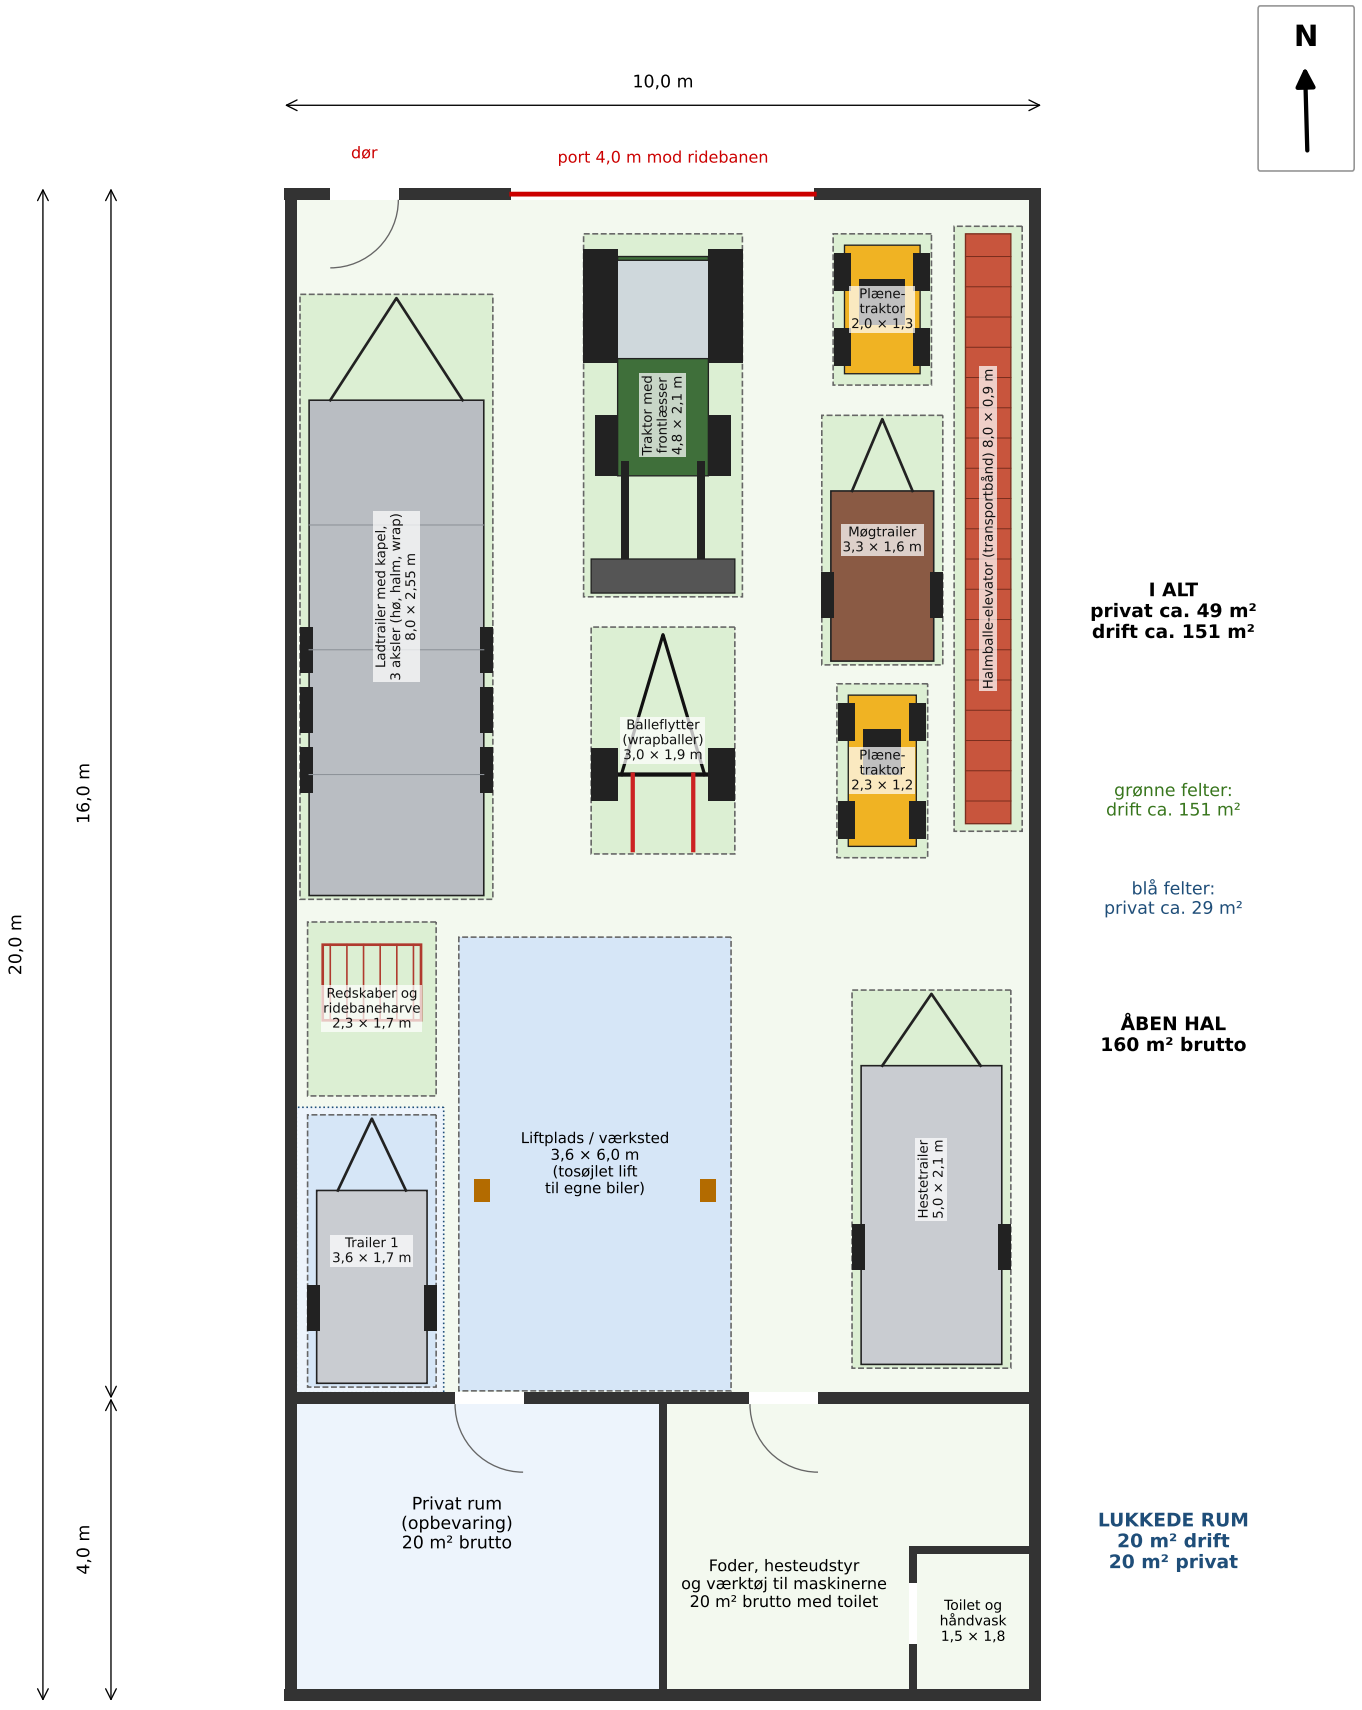

Hal, plan og indretning, Nældevej 42, 9000 Aalborg

Målestok 1:100 (A4) · Udvendigt 10,0 × 20,0 m = 200 m² · Sidehøjde 4,0 m over sokkel, taghældning 30°, kip nord-syd

Maskiner og trailere er tegnet efter fotos af de faktiske maskiner; målene i de stiplede felter er anslået og kan afvige lidt.


Grønne felter: ejendommens drift og hestehold. Blå felter: privat (lift, trailer 1 og det vestlige rum). Rammernes søjler er ikke vist.

BYGGESAG: Nældevej 42, 9000 Aalborg		**A1.1**
EMNE: Ny hal, plan og indretning	DATO: 11.10.2026	LANDZONEANSØGNING
UDFØRT AF: JB	MÅL: 1 : 100 (A4)	


Ny hal, facader

Vægge: sorte, matte sandwichpaneler, vandrette, 1 m høje. Tag: sorte sandwichpaneler, 30°. Sokkel: beton 0,4 m over terræn; gulv i soklens overkant. Sidehøjde 4,0 m over sokkel. Højder i meter over terræn.


Facade mod nord (port og dør mod ridebanen)

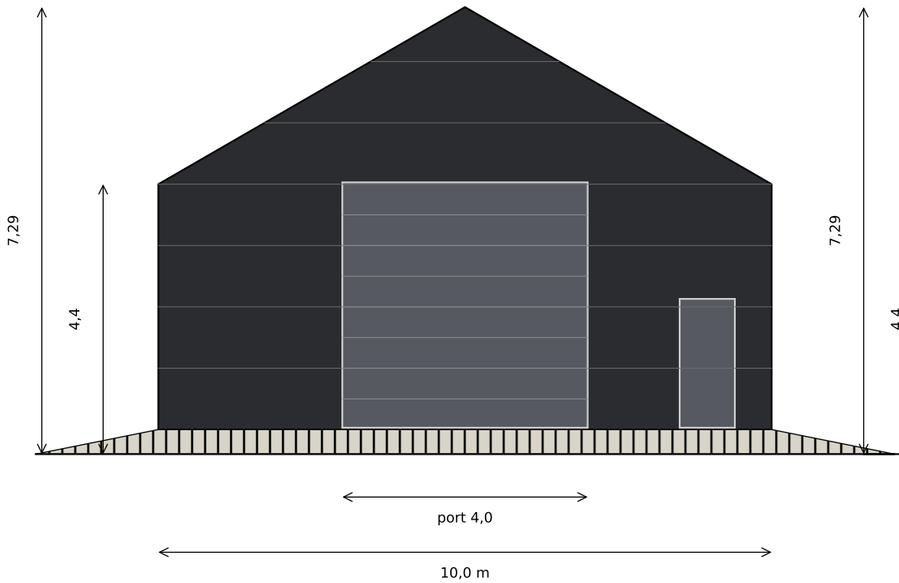


Facade mod øst

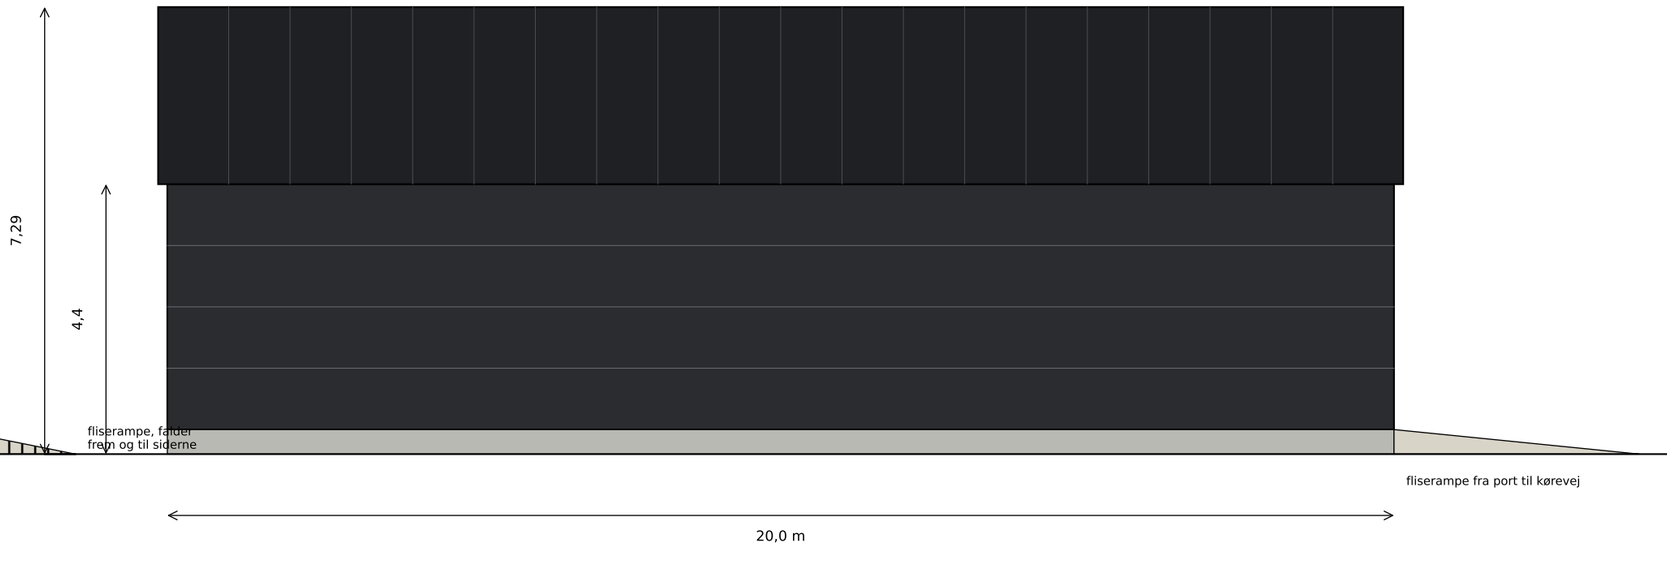

Facade mod syd (ingen åbninger)

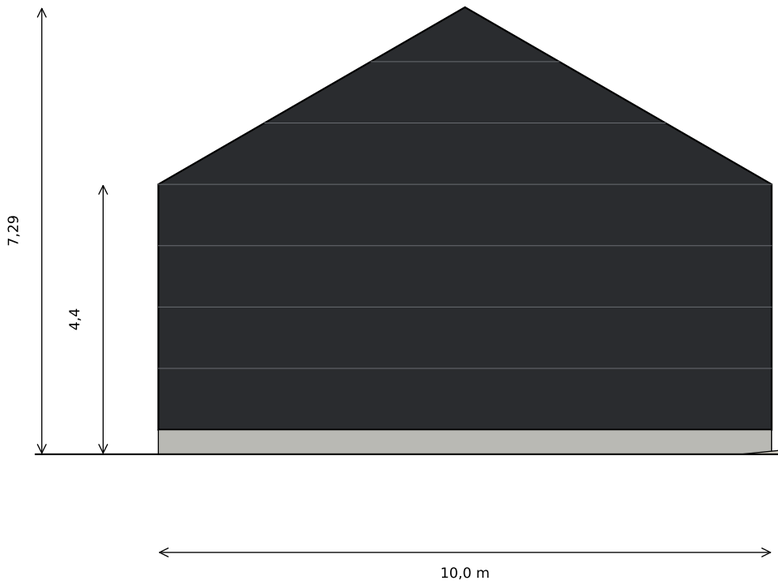


Facade mod vest

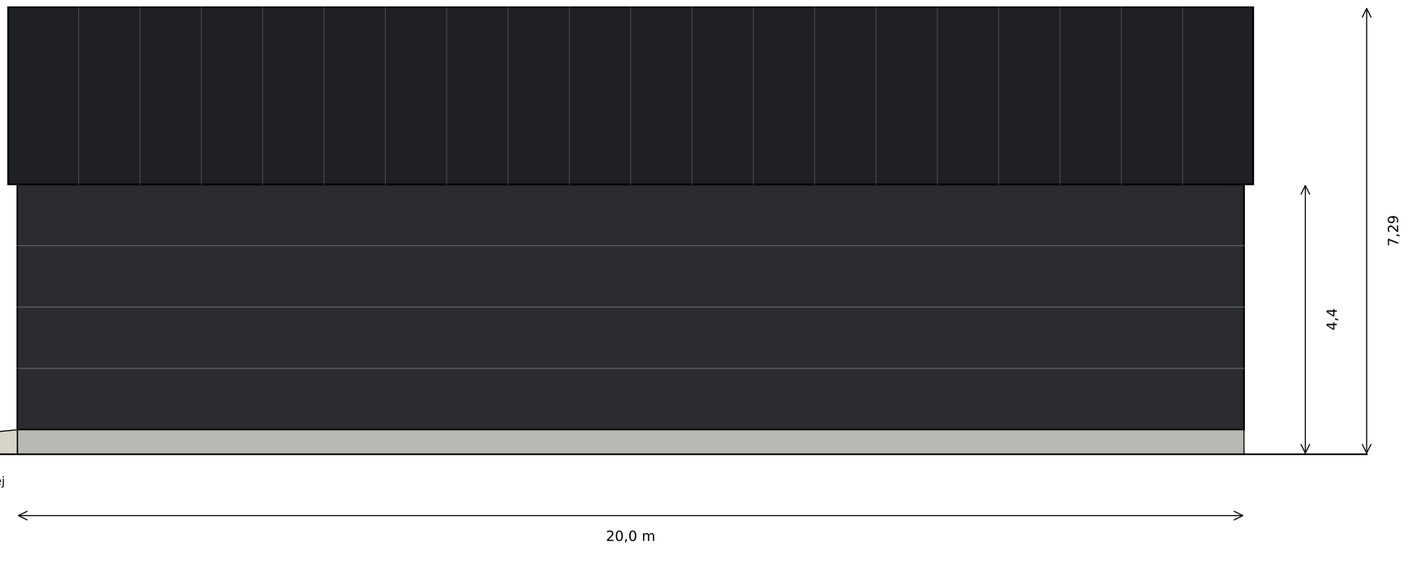

Terræn er forudsat vandret. Panelernes dækbredde (FALK 1060 WB er 1,06 m) og portens endelige højde fastlægges i byggeansøgningen.

BYGGESAG: Nældevej 42, 9000 Aalborg		**A1.2**
EMNE: Ny hal, facader	DATO: 11.10.2026	
UDFØRT AF: JB	MÅL: 1 : 100 (A3)	LANDZONEANSØGNING

Snit A-A gennem en mellemramme (set mod nord)

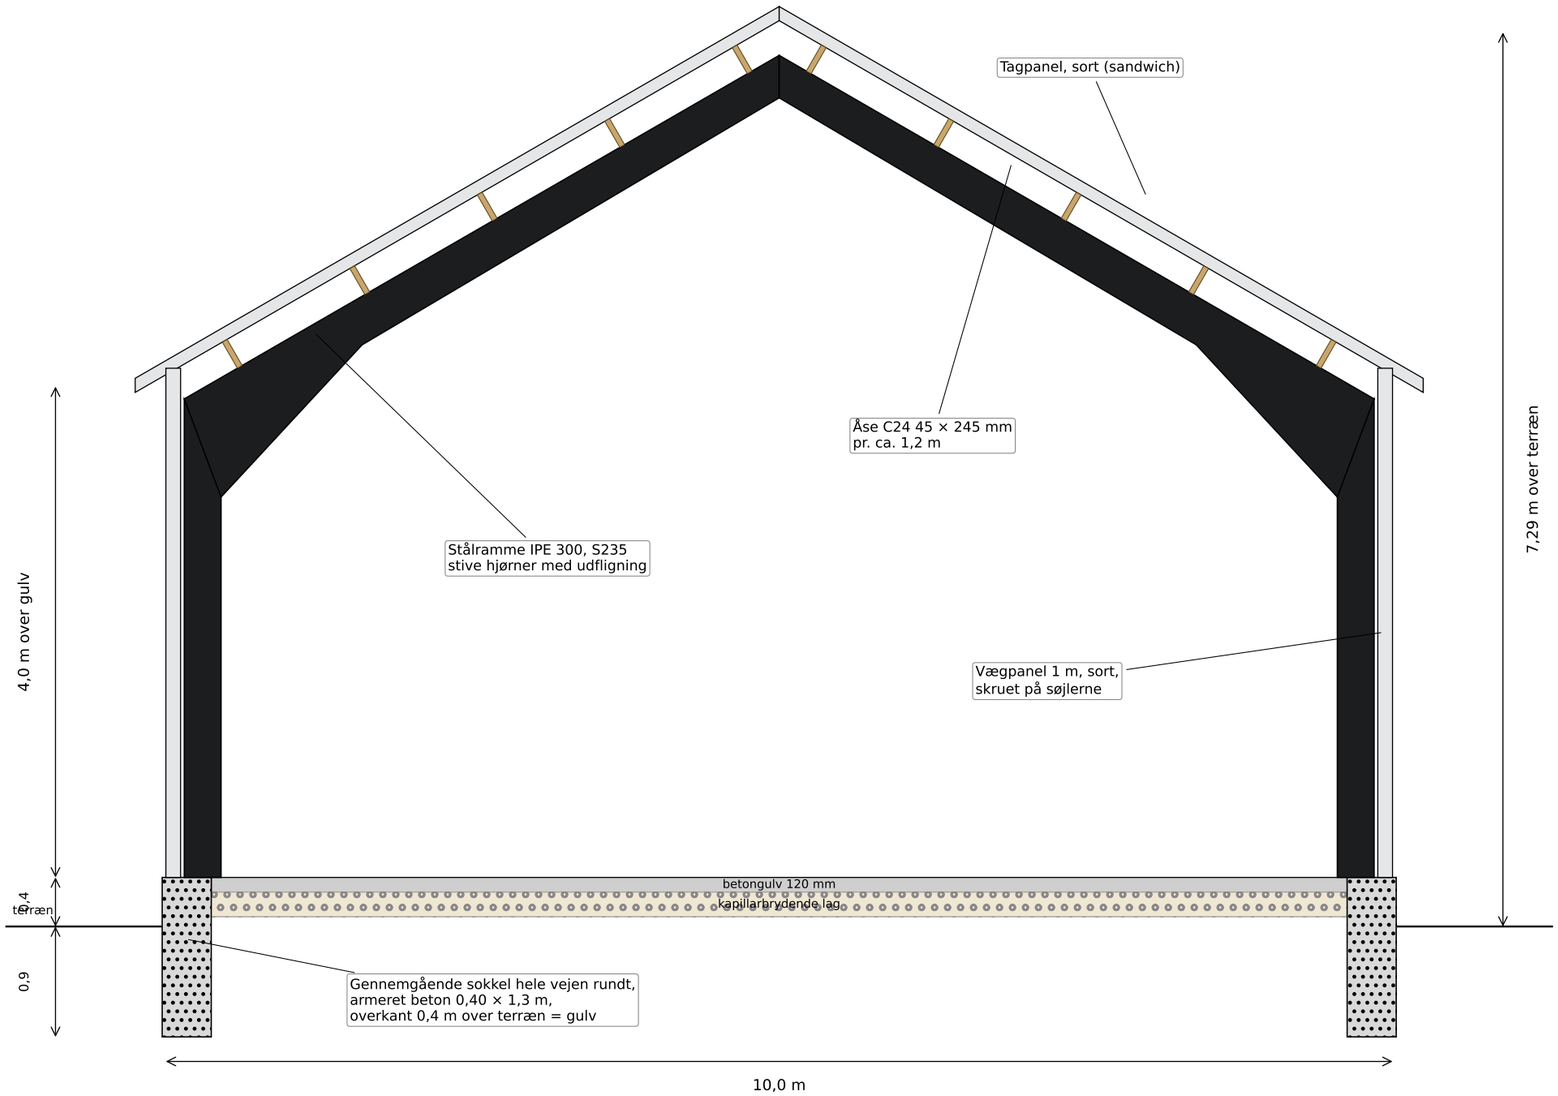

OVERSLAGSBEREGNING, hovedresultater

Ramme: IPE 300 S235, rammeafstand 5,0 m

Sne: s_k = 1,0 kN/m², μ = 0,8 (jævn) og 1,2 (ophobning vest)

Vind: q_p = 0,78 kN/m²

Største moment i rammehjørne: 52,3 kNm

Største moment i kip: 19,7 kNm

Udnyttelse tværsnit / søjle / spær: 0,50 / 0,56 / 0,56

Nedbøjning kip (sne): 7 mm (krav 50 mm)

Udbøjning tagfod (vind): 25 mm (krav 27 mm)

Fundament: gennemgående sokkel 0,40 × 1,3 m

Reaktioner pr. rammefod (regningsmæssige):

tryk 54,5 kN, løft 16,4 kN, vandret 18,9 kN


Åse: C24 45 × 245 mm ved 5 m spænd

Vægkryds: træk 20,4 kN i diagonal

Ikke eftervist: kipning, samlinger, gavlrammer, port,


jordens bæreevne. Se docs/hal-statik-overslag.md.

Momentkurve, K2 (sneophobning på vestlig tagflade)
største moment 52,3 kNm

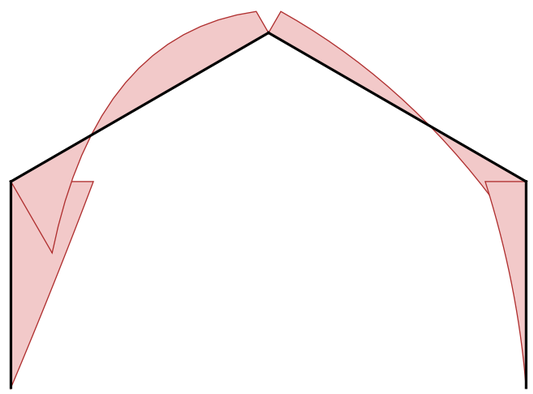

Overslagsberegning. Profiler, åse og fundamenter er vejledende og fastlægges af den projekterende i byggeansøgningen.

BYGGESAG: Nældevej 42, 9000 Aalborg		**A1.3**
EMNE: Ny hal, snit A-A og overslag	DATO: 11.10.2026	LANDZONEANSØGNING
UDFØRT AF: JB	MÅL: 1 : 50 (A3)	

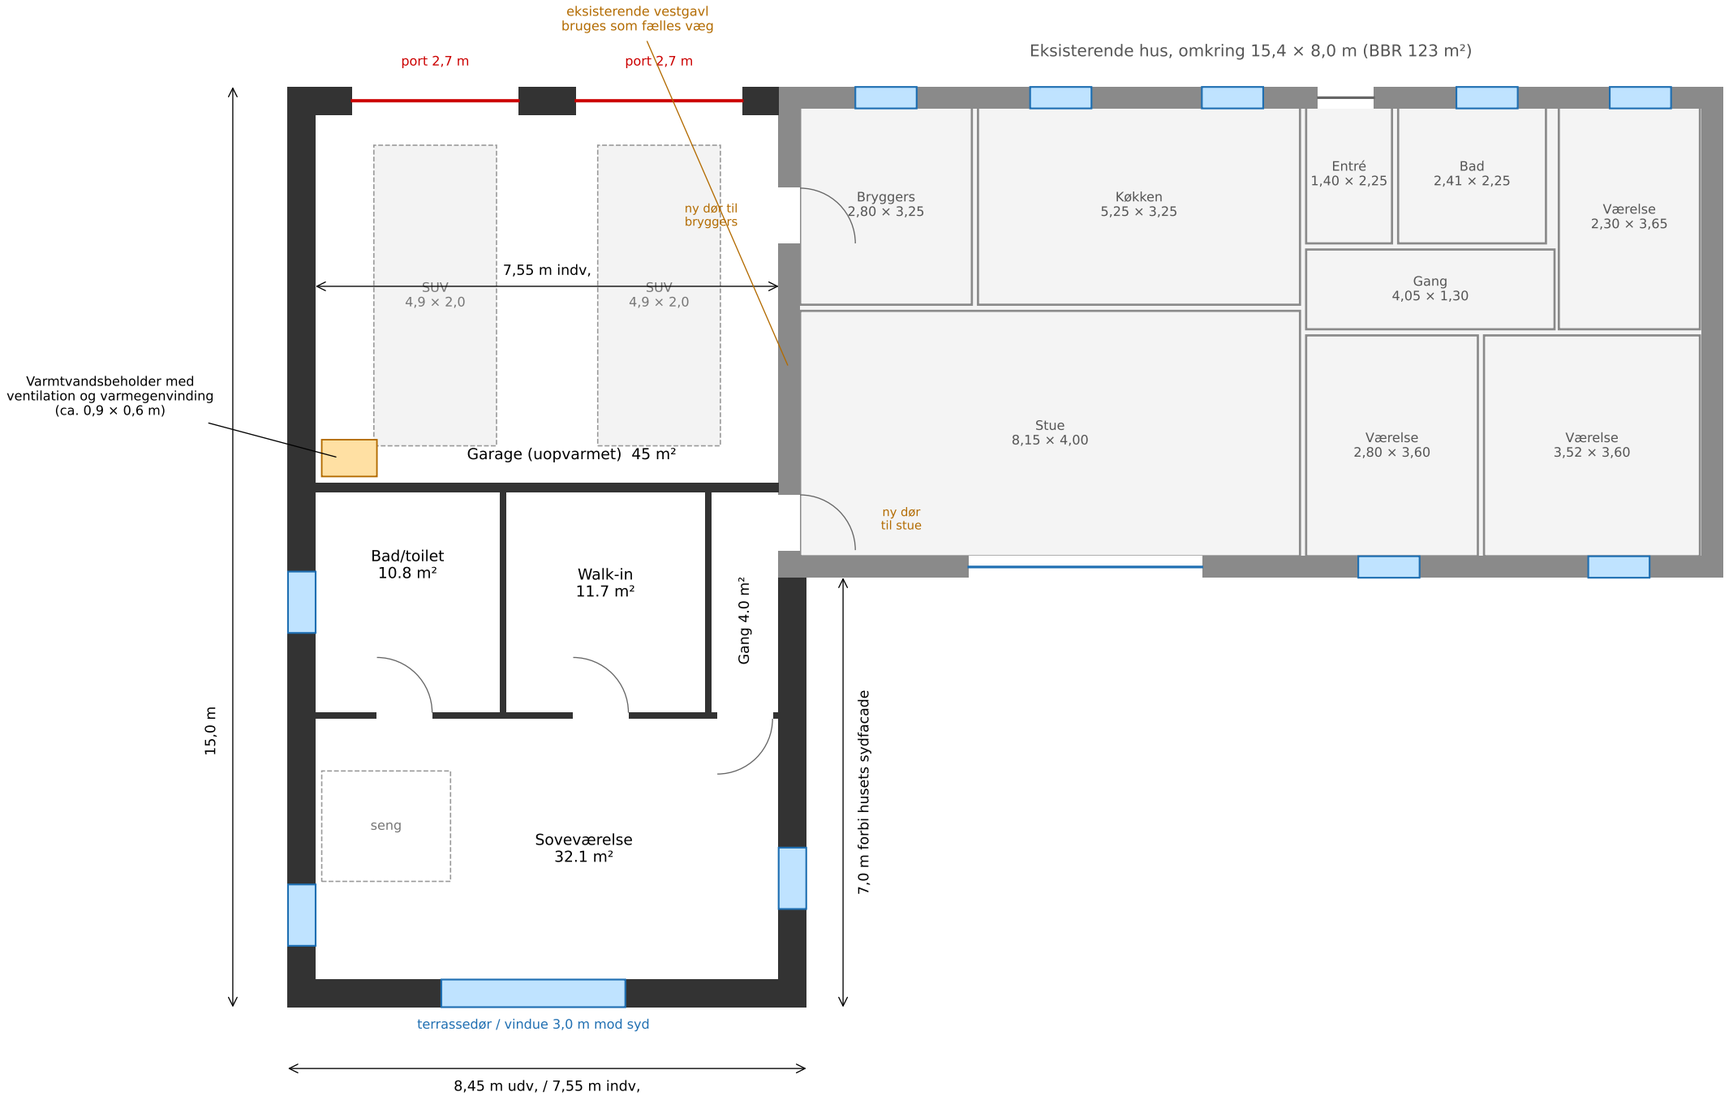

Tilbygning og eksisterende hus, plan, Nældevej 42, 9000 Aalborg

Målestok 1:100 (A3) · Tilbygning 15,0 m lang, 7,55 m bred indvendigt, 123 m² brutto, heraf omkring 71 m² opvarmet bolig

Det eksisterende hus er tegnet efter ejendomsmæglerens vejledende plantegning fra 2024 og måles op før byggeansøgningen. Vægtykkelser i tilbygningen er foreløbige:


ydervæg 45 cm, væg garage/bolig 15 cm, indervægge 10 cm. Brandadskillelse mellem garage og bolig (herunder døren til bryggerset) fastlægges i byggeansøgningen. Bryggersets vindue i vestgavlen forsvinder. Langs huset bruges husets eksisterende vestgavl som fælles væg.

BYGGESAG: Nældevej 42, 9000 Aalborg		**A2.1**
EMNE: Hus med tilbygning, plan	DATO: 11.10.2026	LANDZONEANSØGNING
UDFØRT AF: JB	MÅL: 1 : 100 (A3)	

Hus med tilbygning, facader


Tilbygningen (gul) udføres i samme stil som huset: hvide vægge, sort bølgepladetag, sorte vinduer i husets standardmål. På tegningen er den fremhævet med gul væg. Grå sokkel ca. 0,4 m som på huset. Højder i meter over terræn.

Facade mod nord

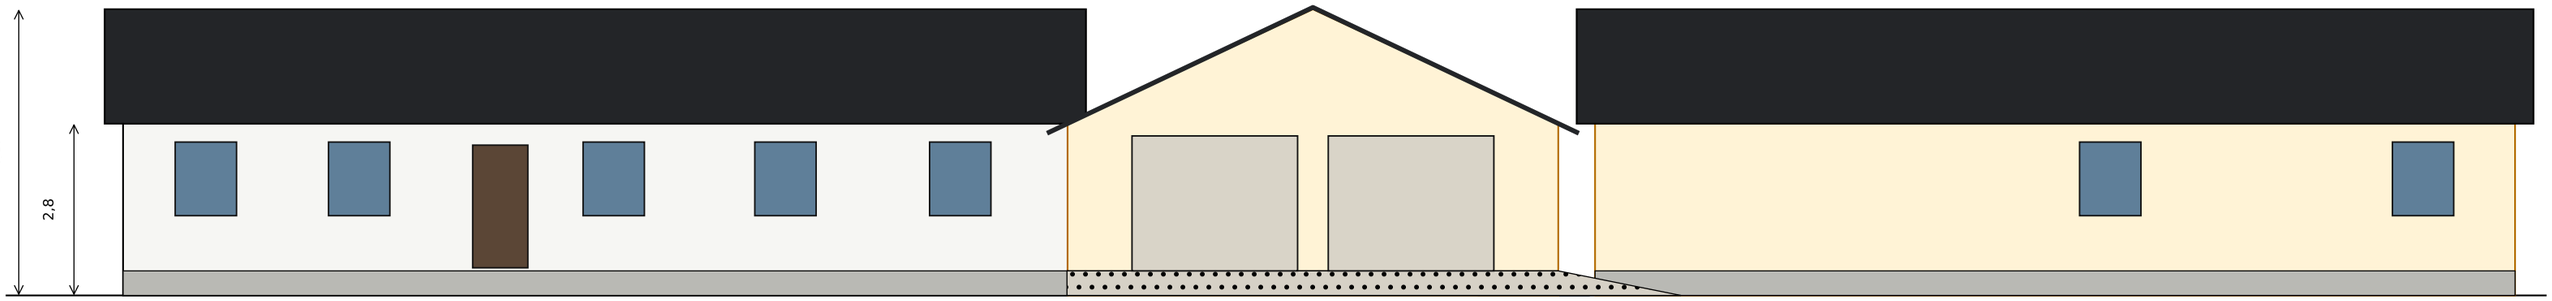

Facade mod vest (tilbygning)

Facade mod syd

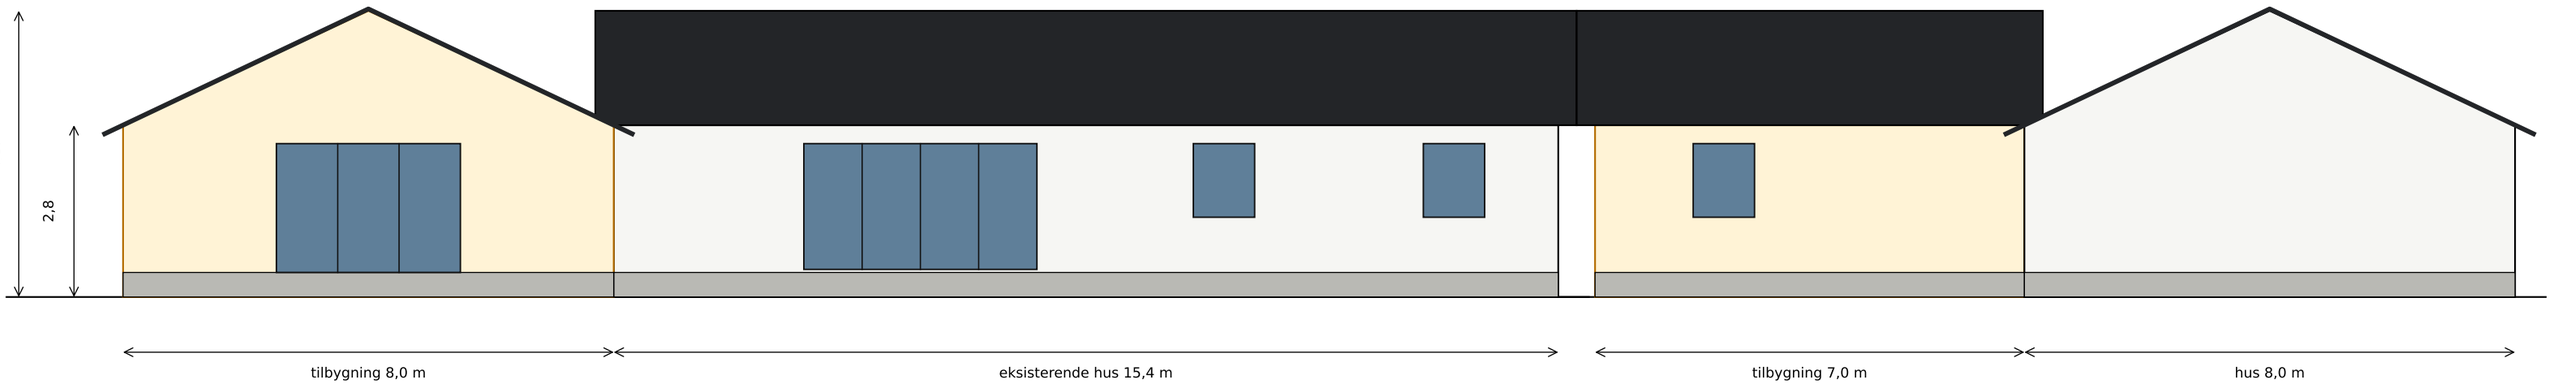

Facade mod øst


Husets højder (tagfod 2,8 m over terræn, sokkel 0,4 m, 25°) og åbninger er anslået fra fotos og ejendomsmæglerens plan og måles op før byggeansøgningen.

Stald og skur er ikke vist. Springet på 45 cm i tilbygningens østvæg er ikke vist.

BYGGESAG: Nældevej 42, 9000 Aalborg		**A2.2**
EMNE: Hus med tilbygning, facader	DATO: 11.10.2026	
UDFØRT AF: JB	MÅL: 1 : 100 (A3)	LANDZONEANSØGNING

Snit B-B gennem soveværelset (set mod nord)

Tal på stængerne: normalkraft i kN for sne på hele taget (K1). Rød = tryk, blå = træk.

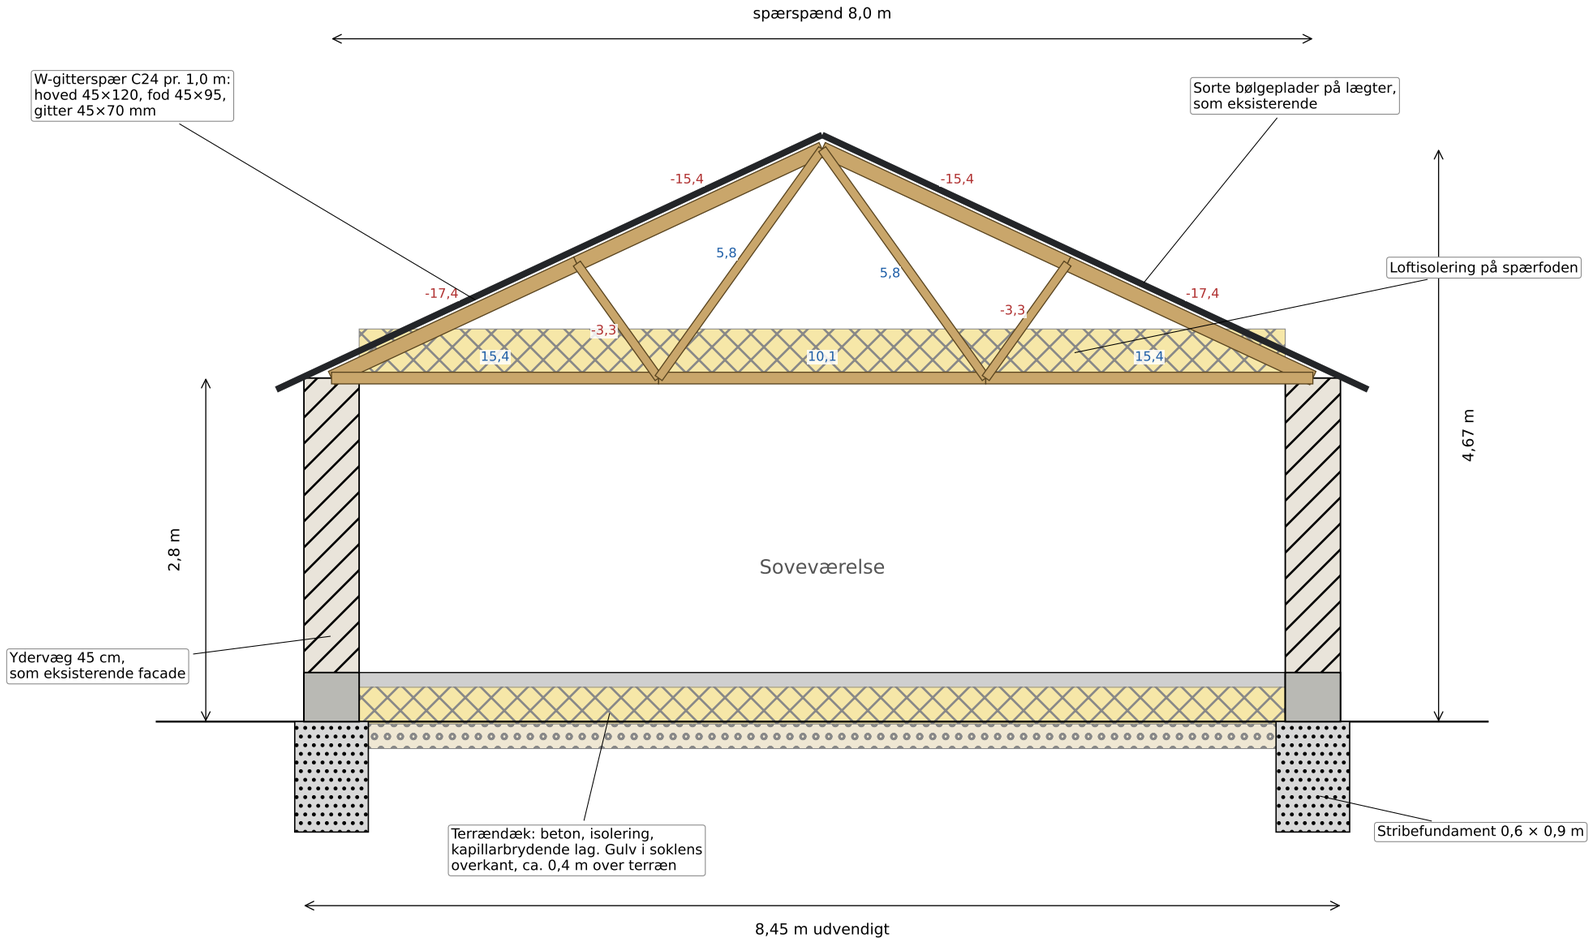

OVERSLAGSBEREGNING, hovedresultater

Spær: W-gitterspær C24, spænd 8,0 m, afstand 1,0 m

Sne: s_k = 1,0 kN/m², μ = 0,8 og 1,2 (ophobning vest)

Egenlast tag 0,35 og loft 0,35 kN/m², opbevaring 0,5 kN/m²

Udnyttelse spærhoved: 0,88

Udnyttelse spærfod: 0,80

Udnyttelse gitterstænger: 0,28

Lodret last pr. spær: 9,8 kN (9,8 kN/m væg)

Løft fra vind pr. spær: 1,4 kN

Linjelast på fundament: ca. 17,8 kN/m

Ikke eftervist: tandpladesamlinger, bæring på husets gavl, skotrender, stabilitet, jordens bæreevne.


Se docs/tilbygning-statik-overslag.md.

Overslagsberegning. Spær dimensioneres og leveres af spærfabrik. Vægopbygning, gulv og fundament er principielle og fastlægges i byggeansøgningen.

BYGGESAG: Nældevej 42, 9000 Aalborg		**A2.3**
EMNE: Tilbygning, snit B-B og overslag	DATO: 11.10.2026	LANDZONEANSØGNING
UDFØRT AF: JB	MÅL: 1 : 50 (A3)	

Stald, BBR-bygning 2: eksisterende indretning og brug

Alle rum er i brug: stald, sadelrum og bad til hesteholdet og vestenden med det gamle stuehus til gæsteværelser. Der er ingen ledige rum til maskiner, trailere eller opbevaring.

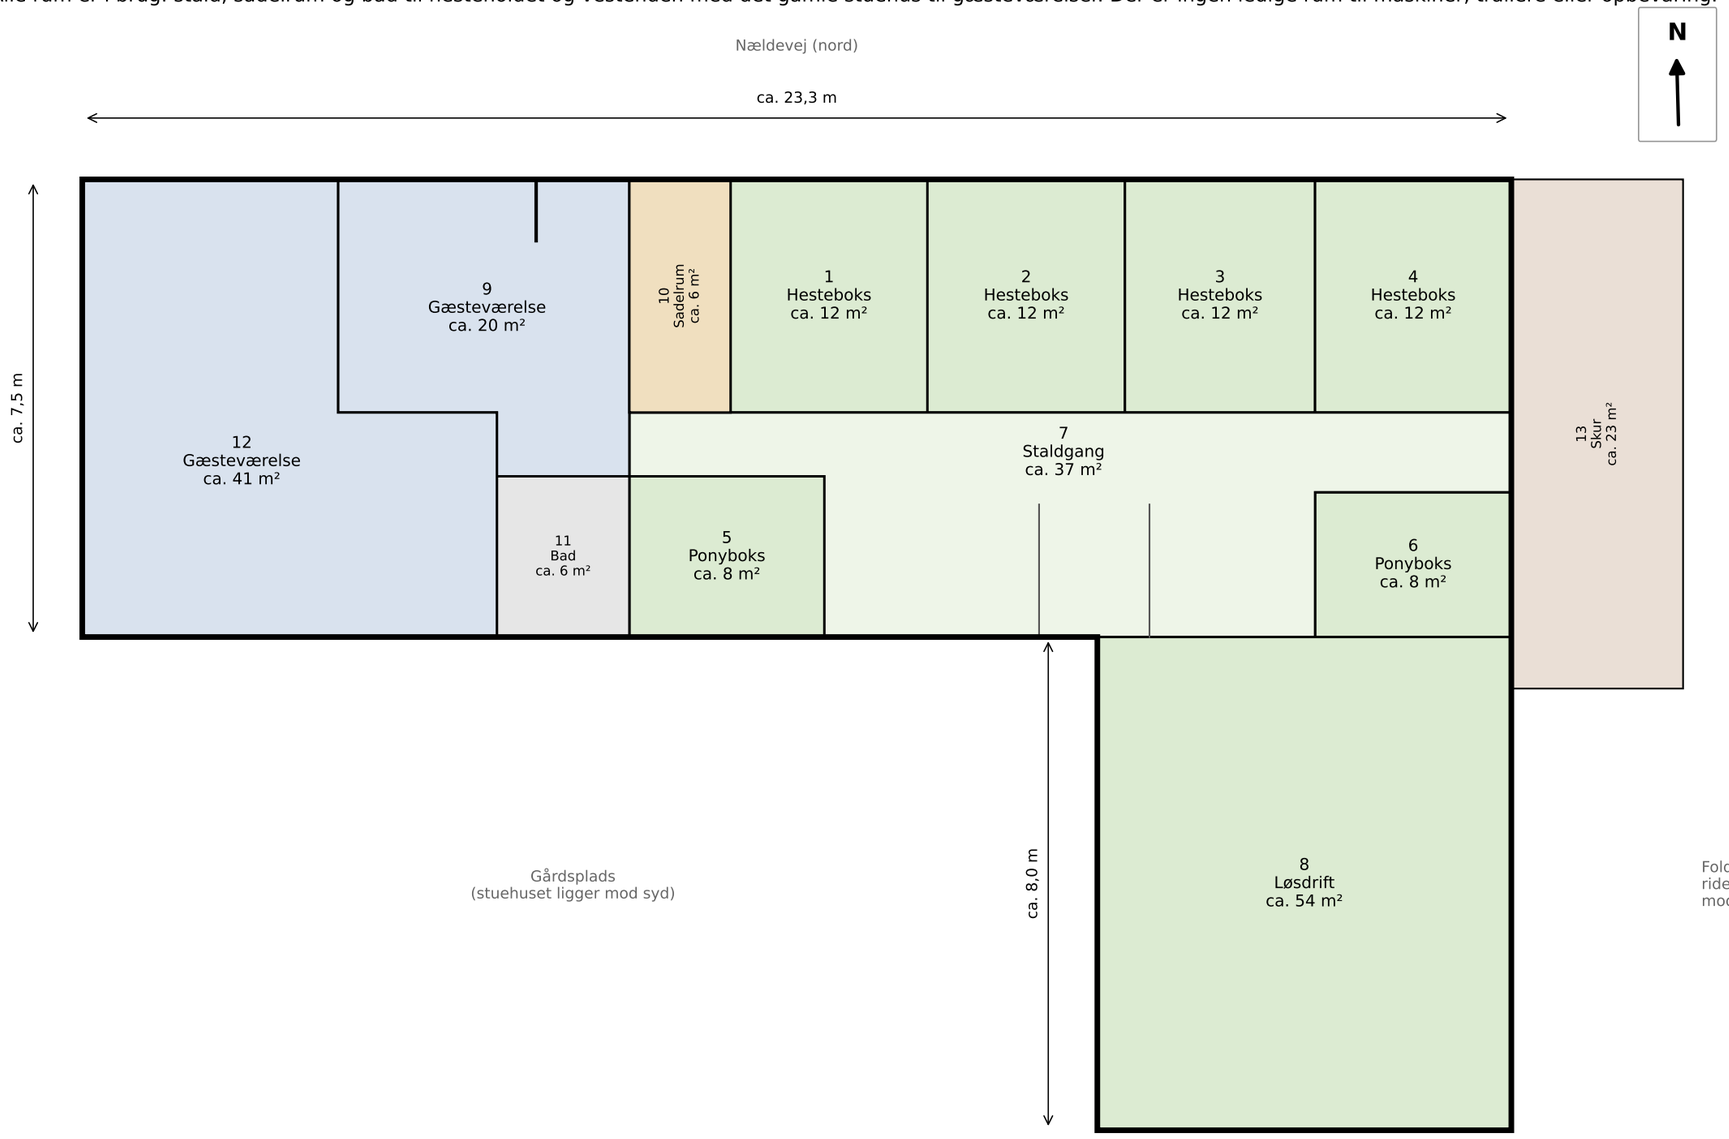

Nr.	Rum, areal og brug
1	**Hesteboks, ca. 12 m²**
	Opstaldning af ejendommens heste
2	**Hesteboks, ca. 12 m²**
	Opstaldning af ejendommens heste
3	**Hesteboks, ca. 12 m²**
	Opstaldning af ejendommens heste
4	**Hesteboks, ca. 12 m²**
	Opstaldning af ejendommens heste
5	**Ponyboks, ca. 8 m²**
	Opstaldning af ejendommens ponyer
6	**Ponyboks, ca. 8 m²**
	Opstaldning af ejendommens ponyer
7	**Staldgang, ca. 37 m²**
	Adgang til boksene, strigleplads, foder og udmugning [bekræftes]
8	**Løsdrift, ca. 54 m²**
	Løsdrift med dybstrøelse, hestene går frit ud og ind til foldene
9	**Gæsteværelse, ca. 20 m²**
	Gæsteværelse til husstandens private gæster. Ét rum; kun en støttevæg på 1 m ved ydervæggen
10	**Sadelrum, ca. 6 m²**
	Sadler, trenser, seletøj og rideudstyr. Tidligere værksted
11	**Bad, ca. 6 m²**
	Bad og toilet til stalden
12	**Gæsteværelse, ca. 41 m²**
	Ejendommens gamle stuehus. Bruges som gæsteværelse til husstandens private gæster
13	**Skur, ca. 23 m²**
	Åbnede wrapballer opbevares her i tørvejr. Ejendommens eneste udhus (byggesag 2020-1967)

Folde og ridebane mod øst

Sammentælling (rumarealer, ca.)


Hestehold (bokse, staldgang, løsdrift):	155 m²
Sadelrum og bad:	12 m²
Gæsteværelser:	61 m²

Stalden er registreret med 284 m² i BBR. Forskellen skyldes vægge, og at planen ikke er målfast. Skuret (nr. 13) er ikke en del af stalden.


Tegnet efter ejendomsmæglerens vejledende plan (ikke målfast). Rumarealer er regnet til vægmidte og er omtrentlige.
Døre, vinduer og porte er ikke vist. Skurets placering og mål er efter situationsplanen.

BYGGESAG: Nældevej 42, 9000 Aalborg		**A3.1**
EMNE: Stald, eksisterende indretning og brug	DATO: 11.10.2026	LANDZONEANSØGNING
UDFØRT AF: JB	MÅL: 1 : 100 (A3)	


Set fra sydøst

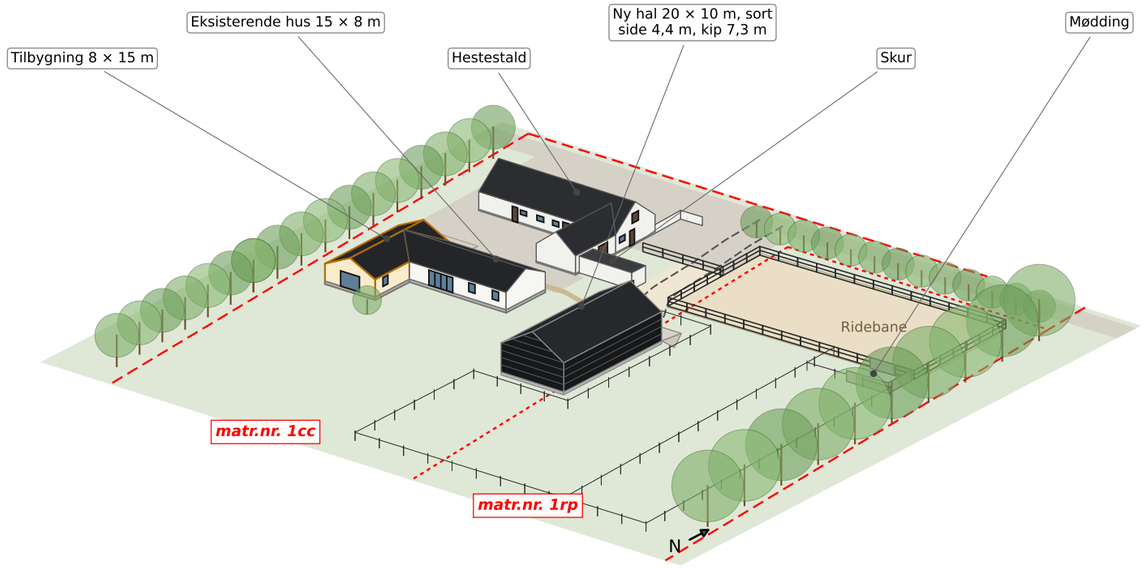


Set fra sydvest

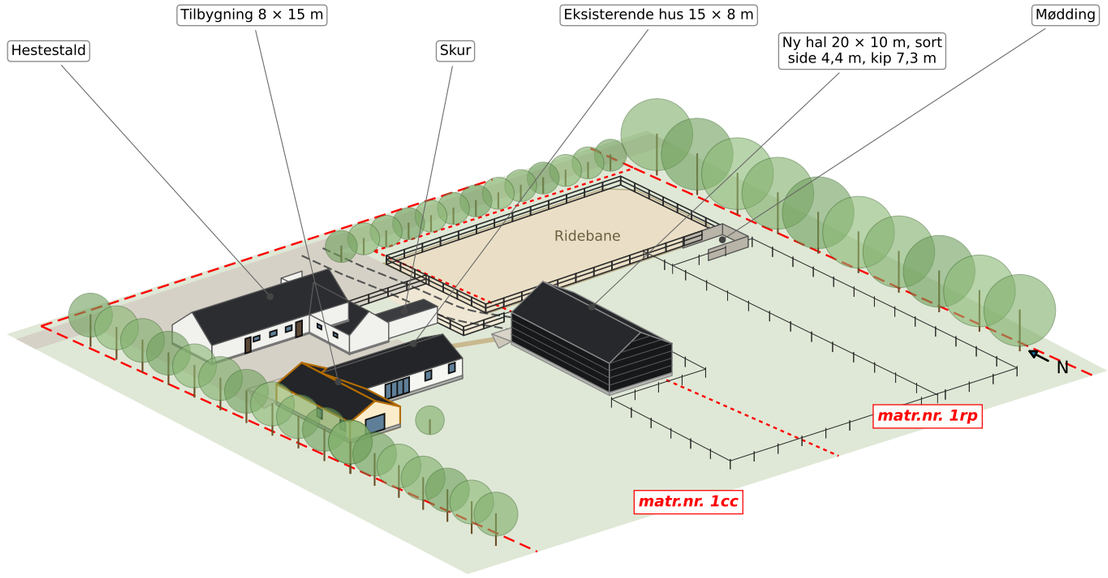

Set fra nordvest

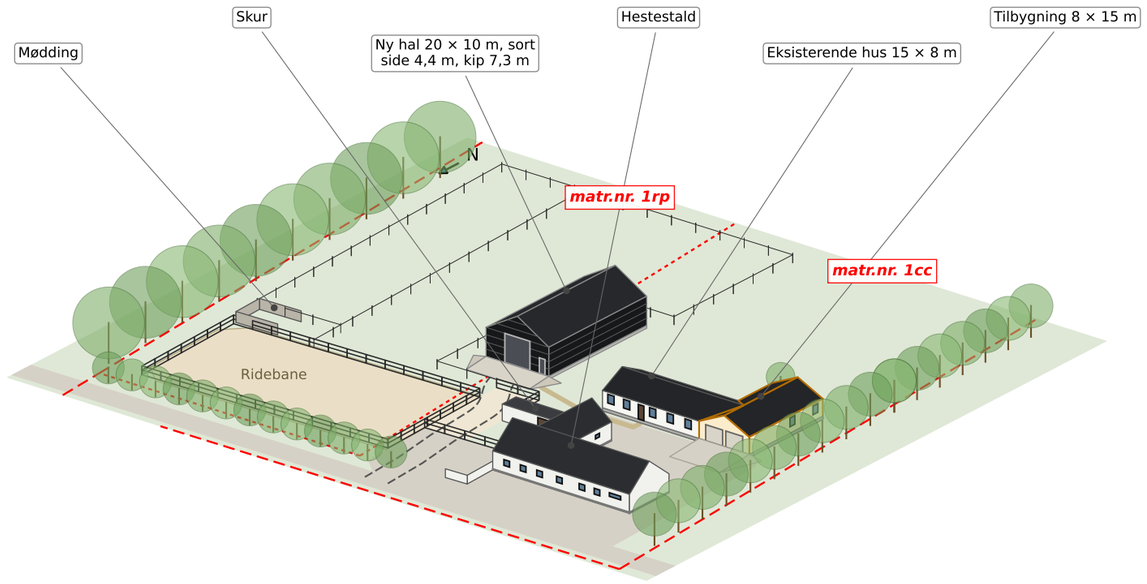

Set fra nordøst

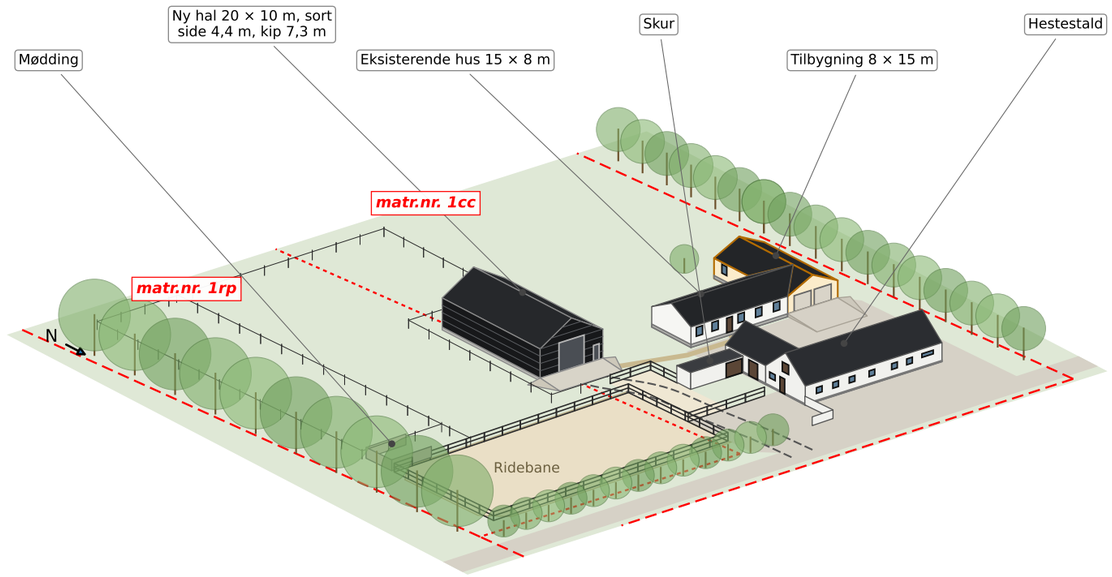

Rumlige skitser fra fire hjørner, Nældevej 42, 9000 Aalborg

Rumlige skitser i parallelprojektion, ikke målfaste. Hallens mål er de ansøgte. Tagfod og taghældning på hus og tilbygning (2,8 m, 25°) og stald (2,6 m, 38°) samt skurets højde er anslået fra fotos.

Farver og åbninger i hus og stald følger ejendomsmæglerens plantegning (2024) og fotos. Ridebane, hegn, grusarealer og læbælter er tegnet efter luftfoto. Tilbygningen er fremhævet med gul væg; den udføres hvid som huset.