
Snit A-A gennem en mellemramme (set mod nord)

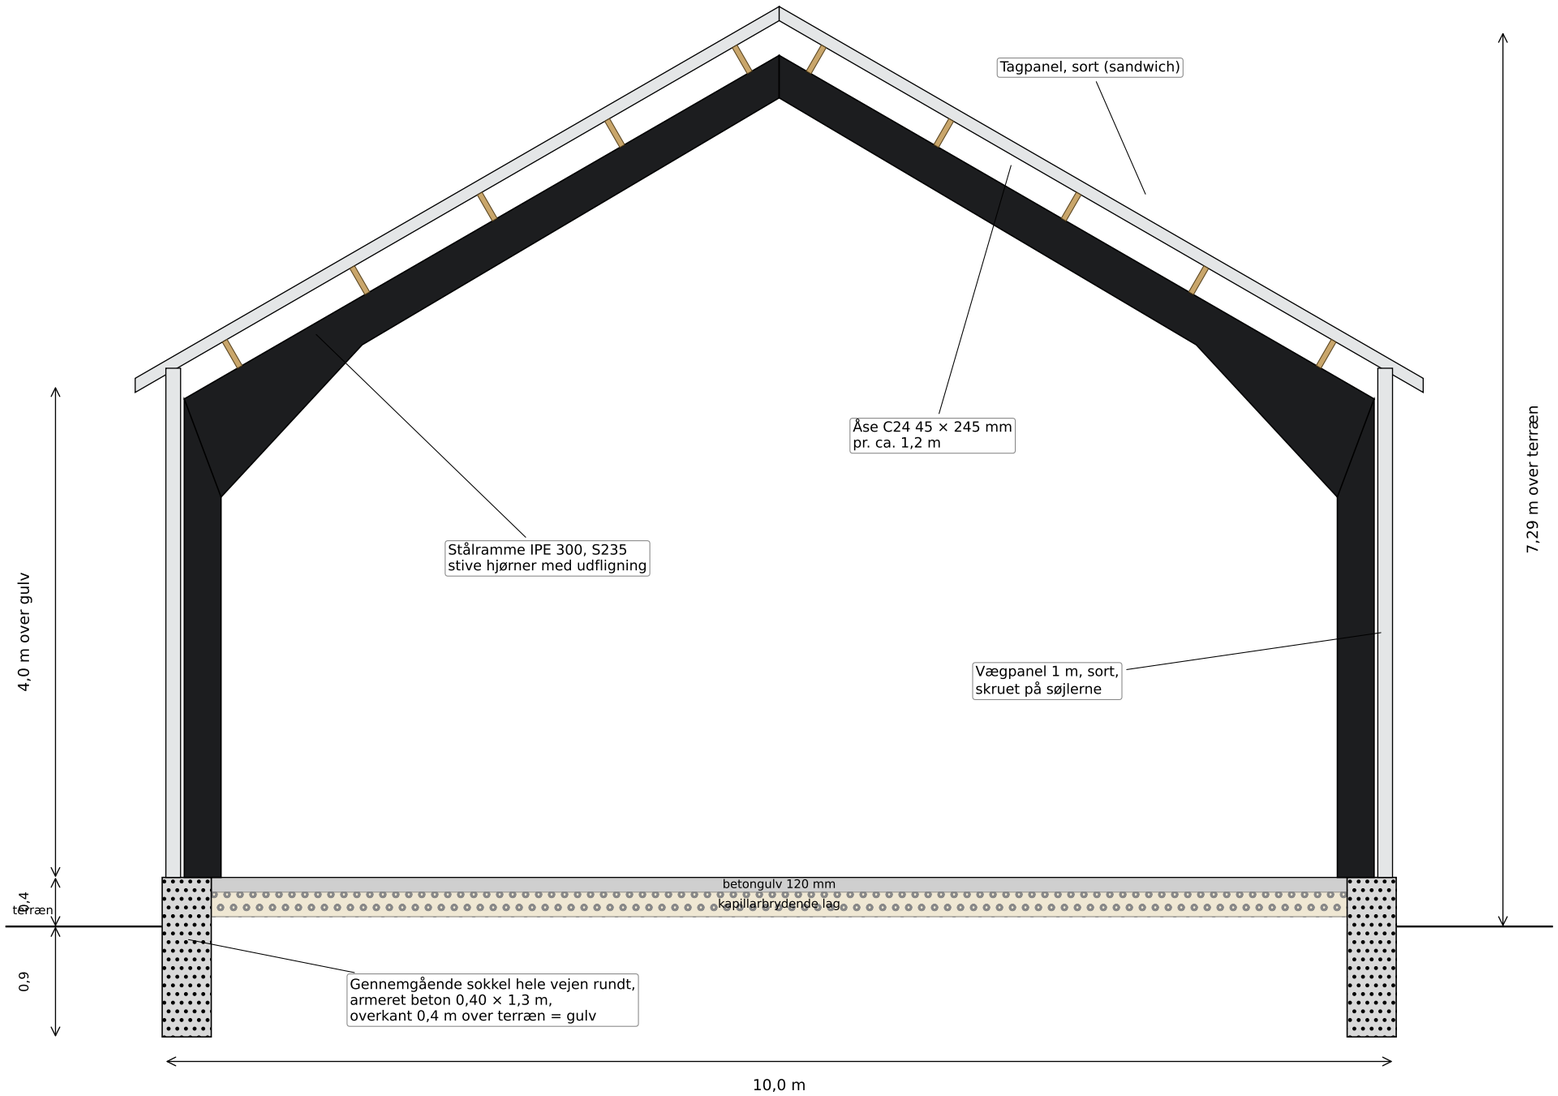

OVERSLAGSBEREGNING, hovedresultater

Ramme: IPE 300 S235, rammeafstand 5,0 m

Sne: s_k = 1,0 kN/m², μ = 0,8 (jævn) og 1,2 (ophobning vest)

Vind: q_p = 0,78 kN/m²

Største moment i rammehjørne: 52,3 kNm

Største moment i kip: 19,7 kNm

Udnyttelse tværsnit / søjle / spær: 0,50 / 0,56 / 0,56

Nedbøjning kip (sne): 7 mm (krav 50 mm)

Udbøjning tagfod (vind): 25 mm (krav 27 mm)

Fundament: gennemgående sokkel 0,40 × 1,3 m

Reaktioner pr. rammefod (regningsmæssige):

tryk 54,5 kN, løft 16,4 kN, vandret 18,9 kN


Åse: C24 45 × 245 mm ved 5 m spænd

Vægkryds: træk 20,4 kN i diagonal

Ikke eftervist: kipning, samlinger, gavlrammer, port,

jordens bæreevne. Se docs/hal-statik-overslag.md.

Momentkurve, K2 (sneophobning på vestlig tagflade)
største moment 52,3 kNm

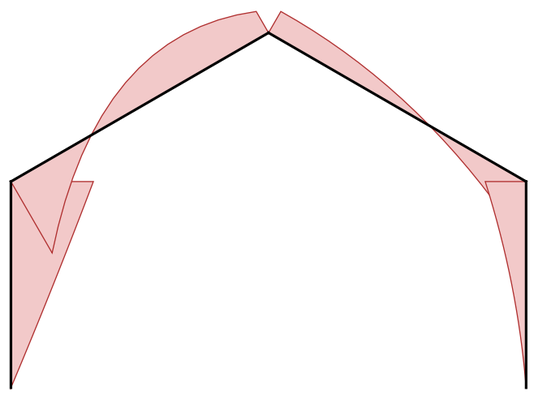

Overslagsberegning. Profiler, åse og fundamenter er vejledende og fastlægges af den projekterende i byggeansøgningen.

BYGGESAG: Nældevej 42, 9000 Aalborg		**A1.3**
EMNE: Ny hal, snit A-A og overslag	DATO: 11.10.2026	LANDZONEANSØGNING
UDFØRT AF: JB	MÅL: 1 : 50 (A3)	